
Solar Energy System Wiring Diagram


990kW Solar Energy System with 1256kW PV

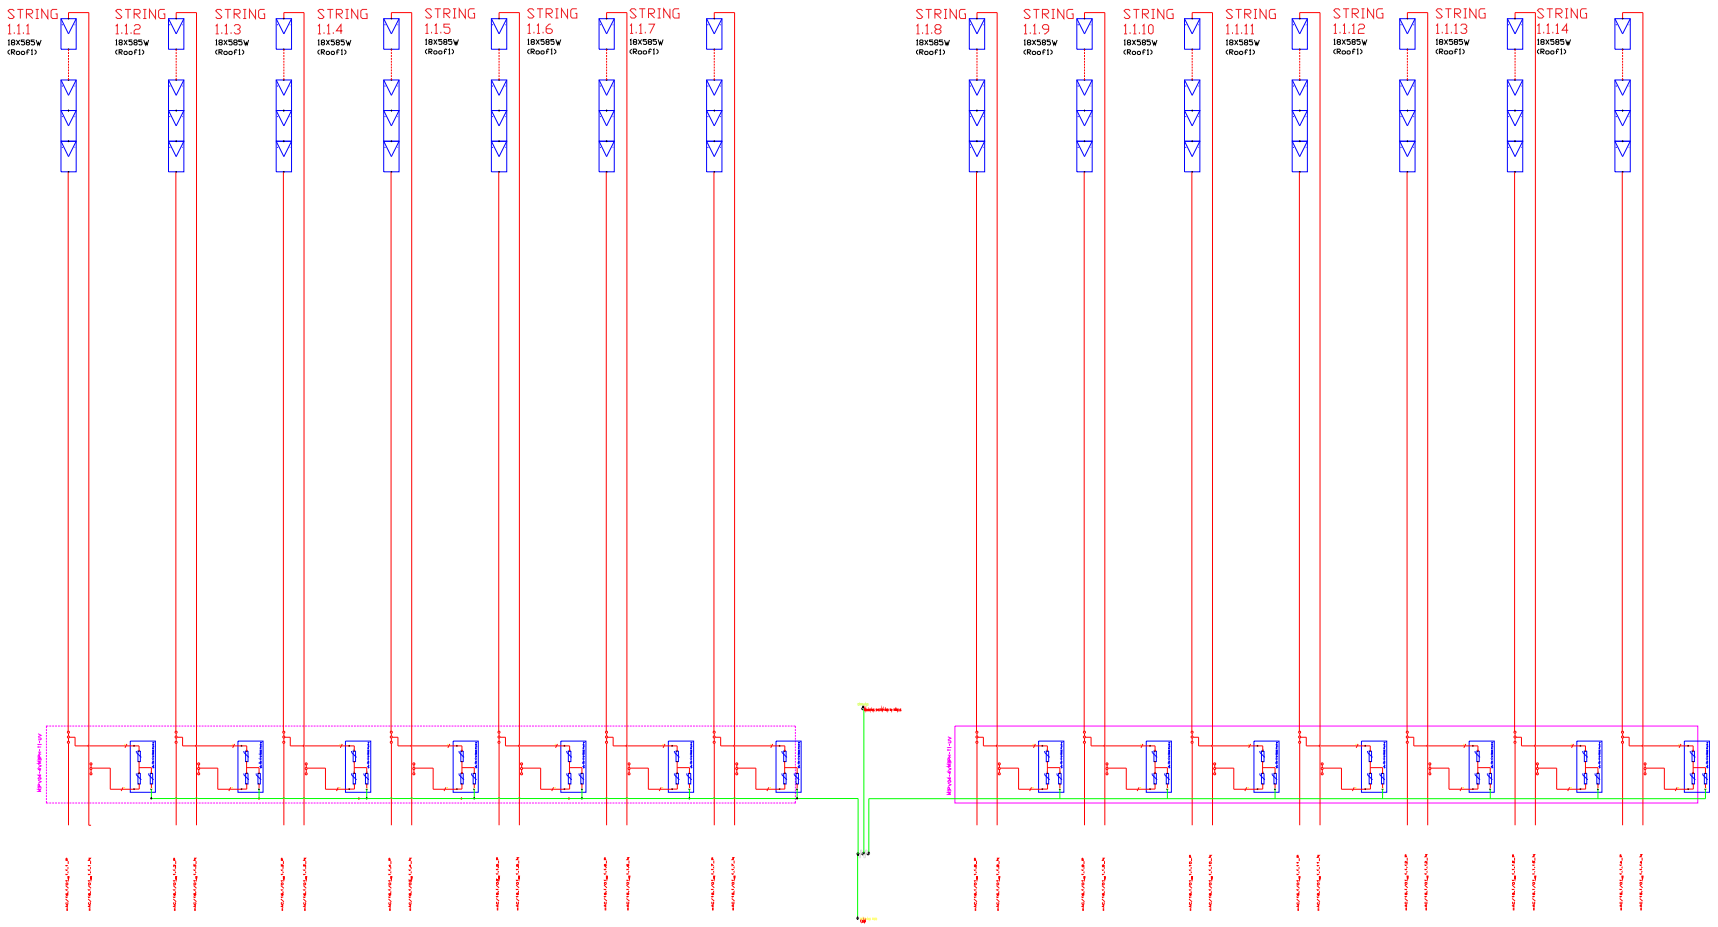


REVISIONS

	Rooftop Solar System at Al-Falah-Industrial Campus
	AL-FALAH INDUSTRIAL CAMPUS, DUBAI, UAE
	Building A
SIZE	FSCM NO / DRAWING NUMBER 1 / REV 1
SCALE	SHEET 1

REVISIONS				

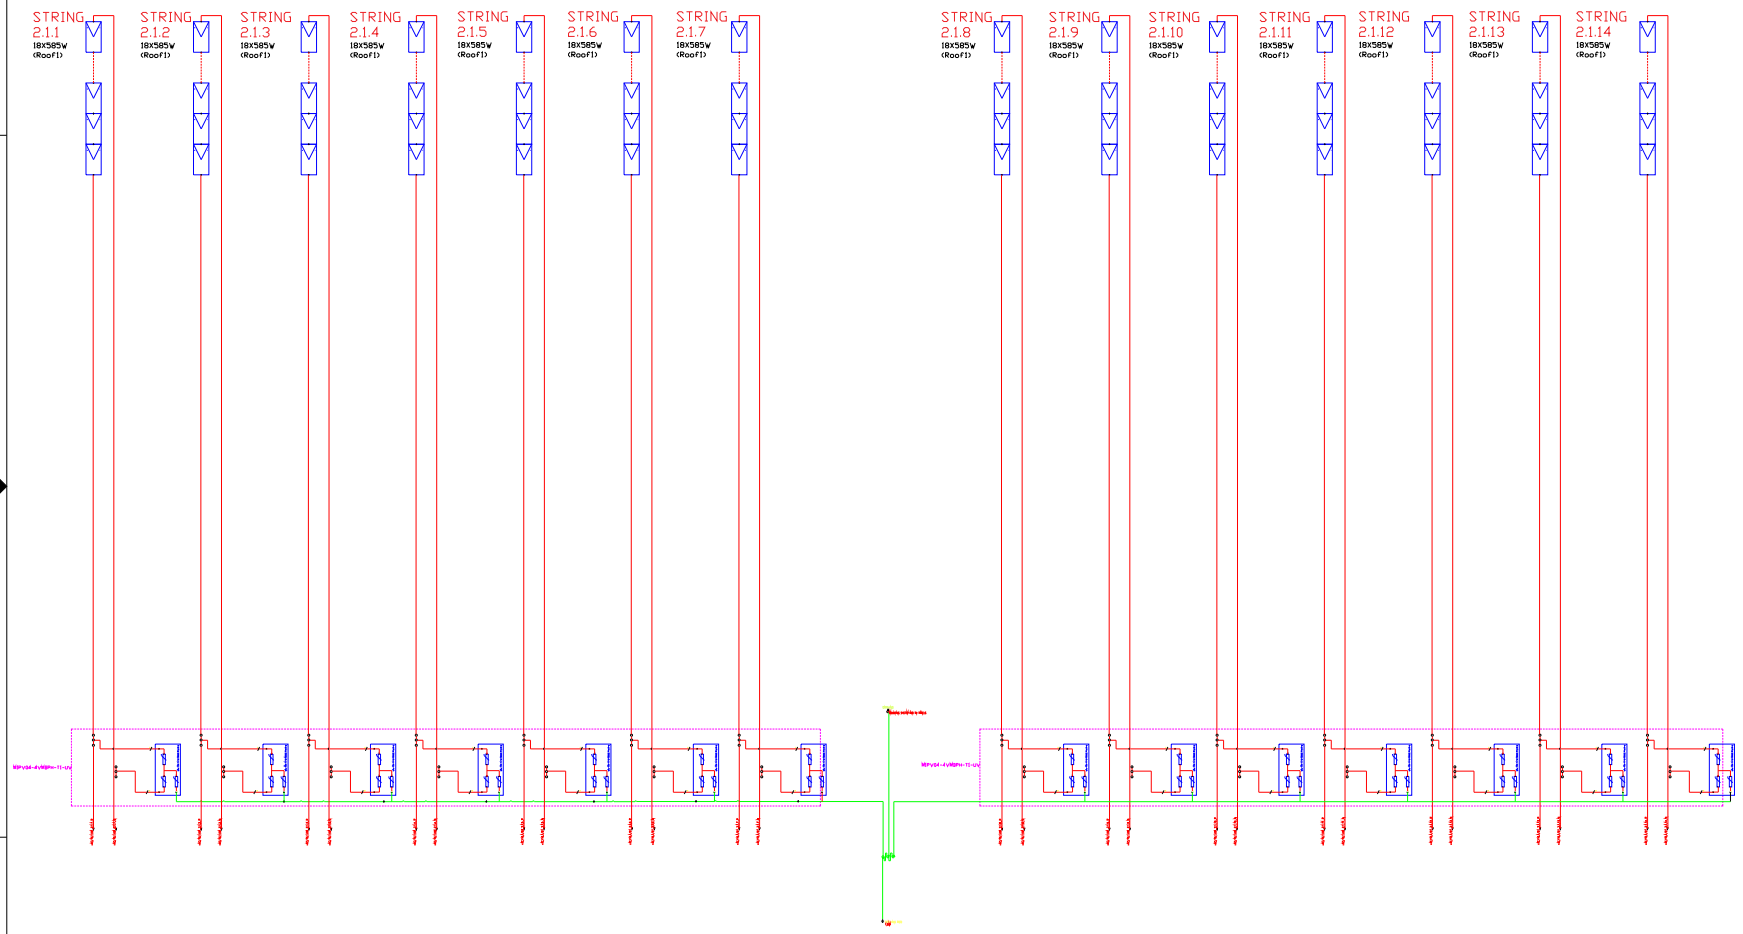

	Rooftop Solar System at Al-Falah-Industrial Campus			
	AL-FALAH INDUSTRIAL CAMPUS, DUBAI, UAE			
	Building A			
	SIZE	FSCM NO	DRAWING NUMBER 2	REV 1
	SCALE		SHEET 1	

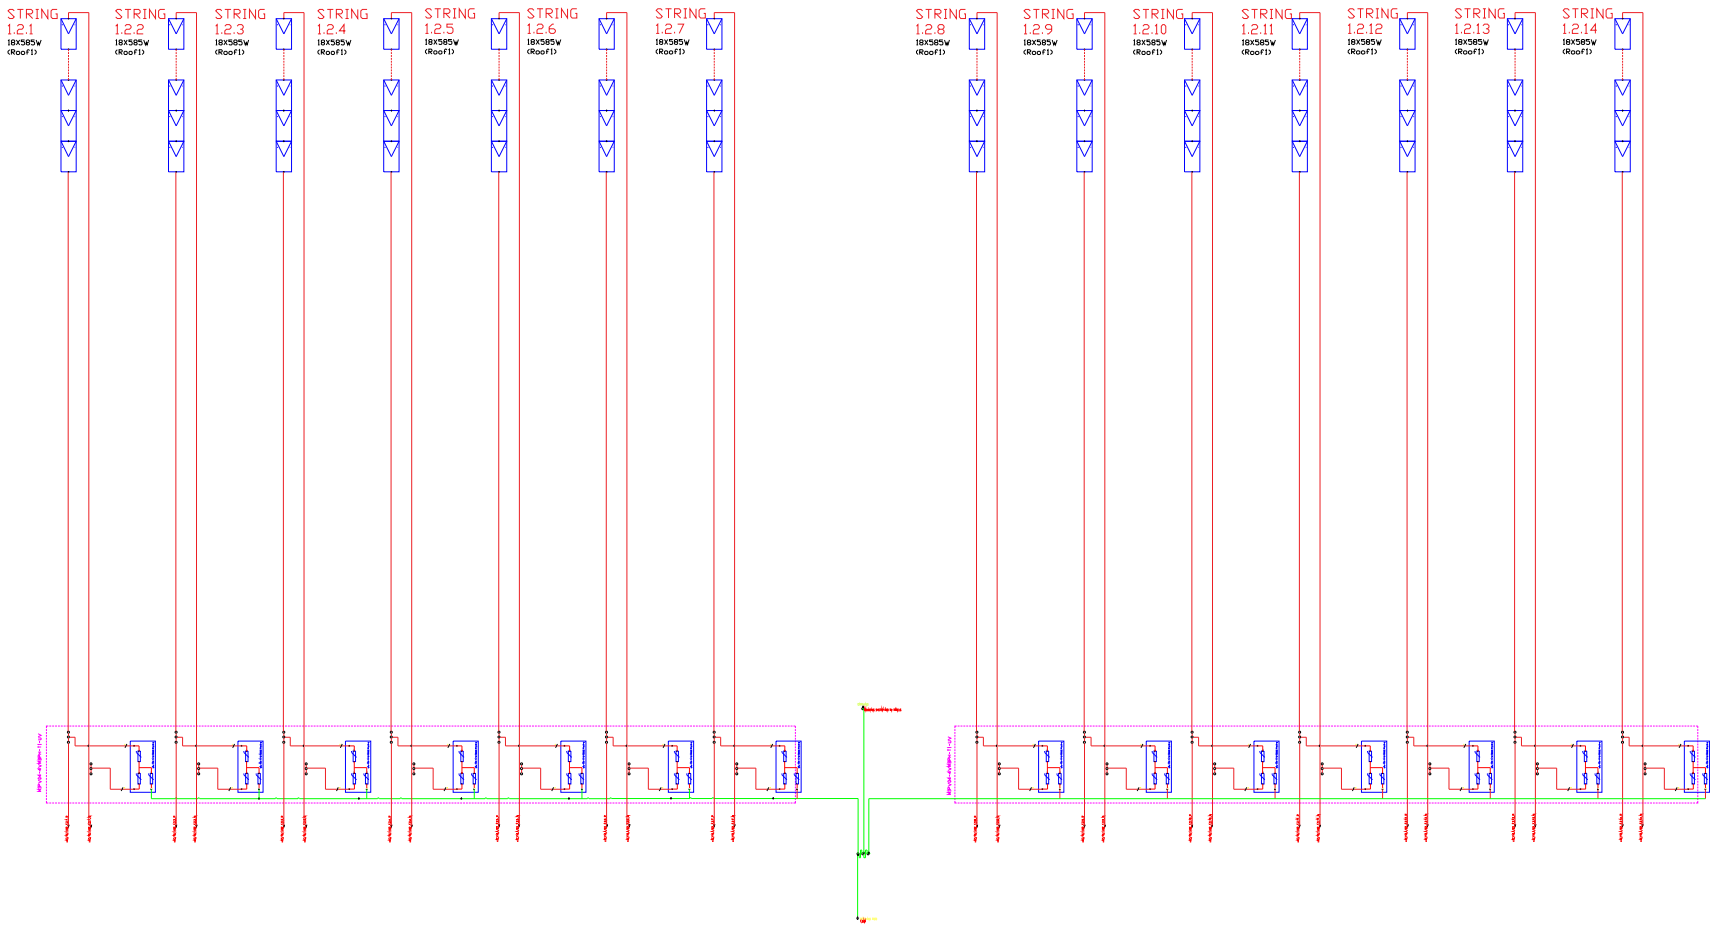


REVISIONS

Rooftop Solar System at Al-Falah-Industrial Campus

AL-FALAH INDUSTRIAL CAMPUS, DUBAI, UAE

Building B


SIZE	FSCM NO	DRAWING NUMBER	REV
		3	1
SCALE		SHEET 1	

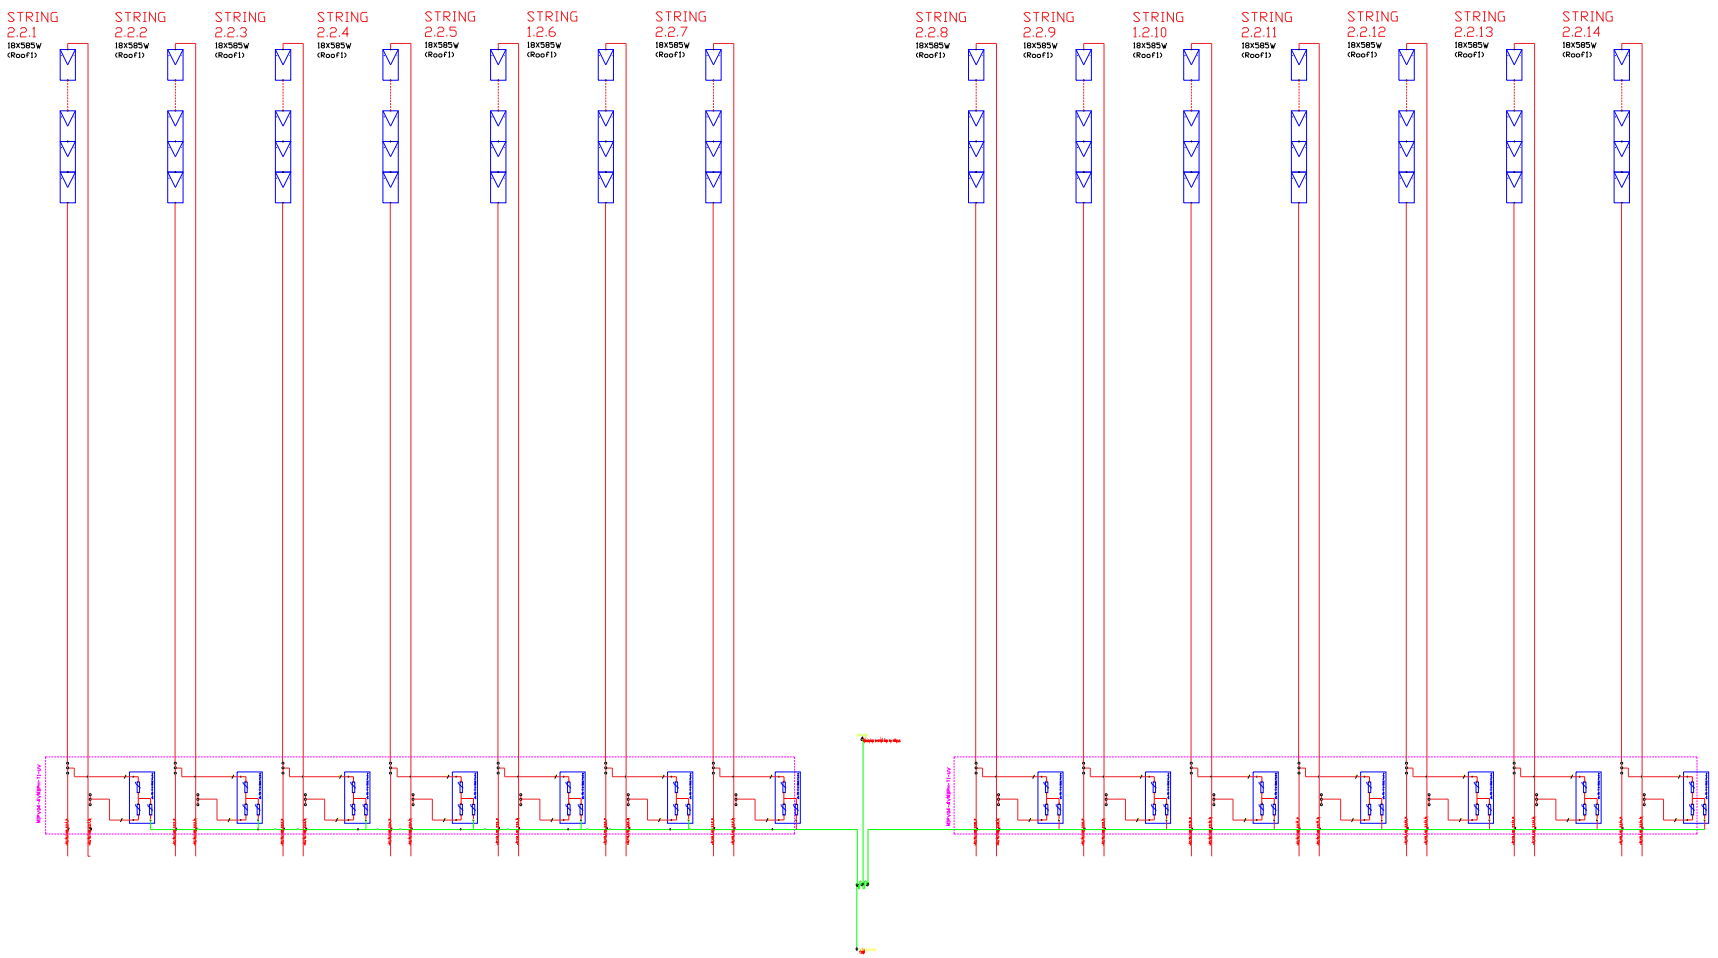

REVISIONS


	Rooftop Solar System at Al-Falah-Industrial Campus
	AL-FALAH INDUSTRIAL CAMPUS, DUBAI, UAE
	Building B
SIZE	FSCM NO / DRAWING NUMBER 4 / REV 1
SCALE	SHEET 1

REVISIONS				

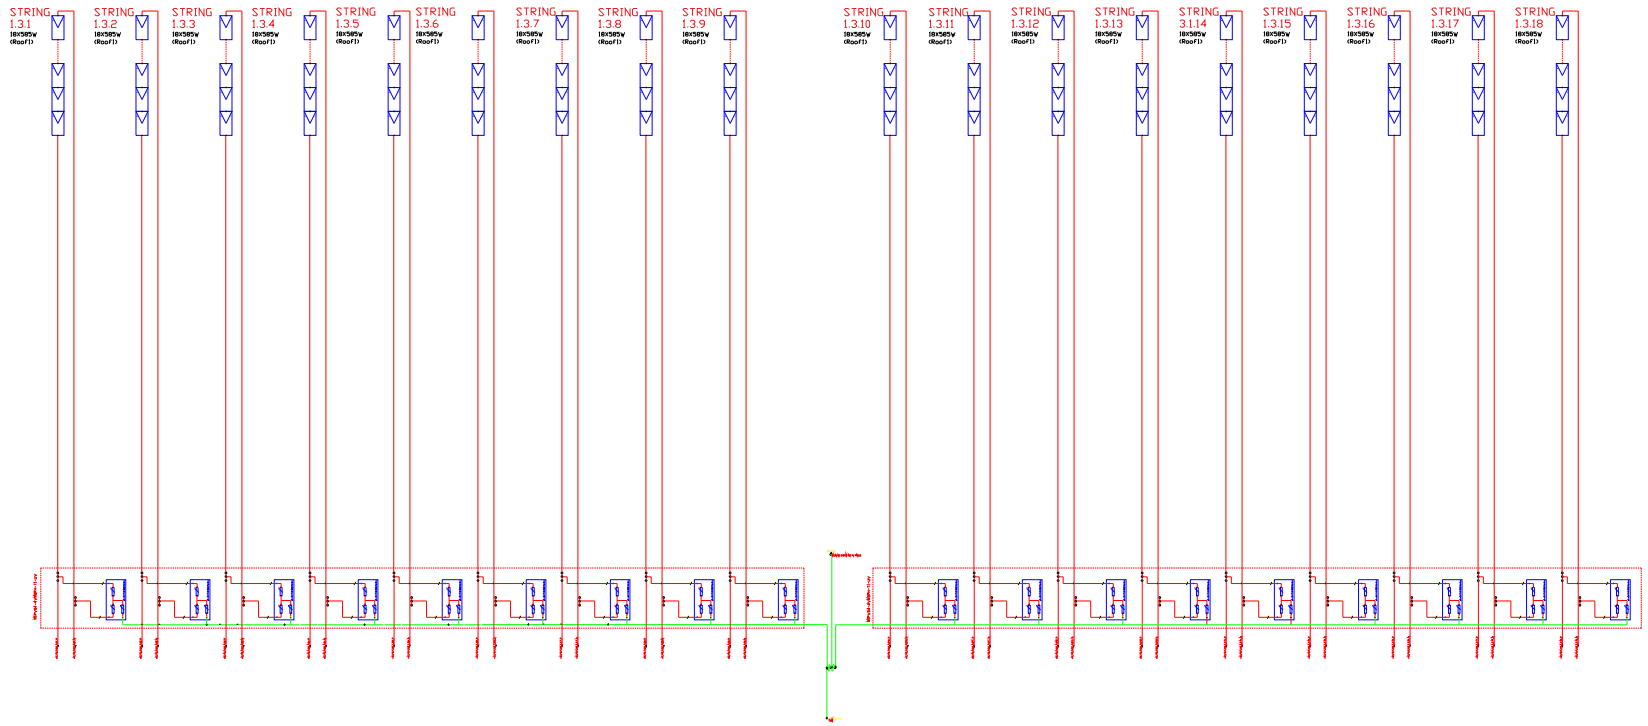


	Rooftop Solar System at Al-Falah-Industrial Campus			
	AL-FALAH INDUSTRIAL CAMPUS, DUBAI, UAE			
	Building C			
	SIZE	FSCM NO	DRAWING NUMBER 5	REV 1
	SCALE		SHEET 1	

REVISIONS				

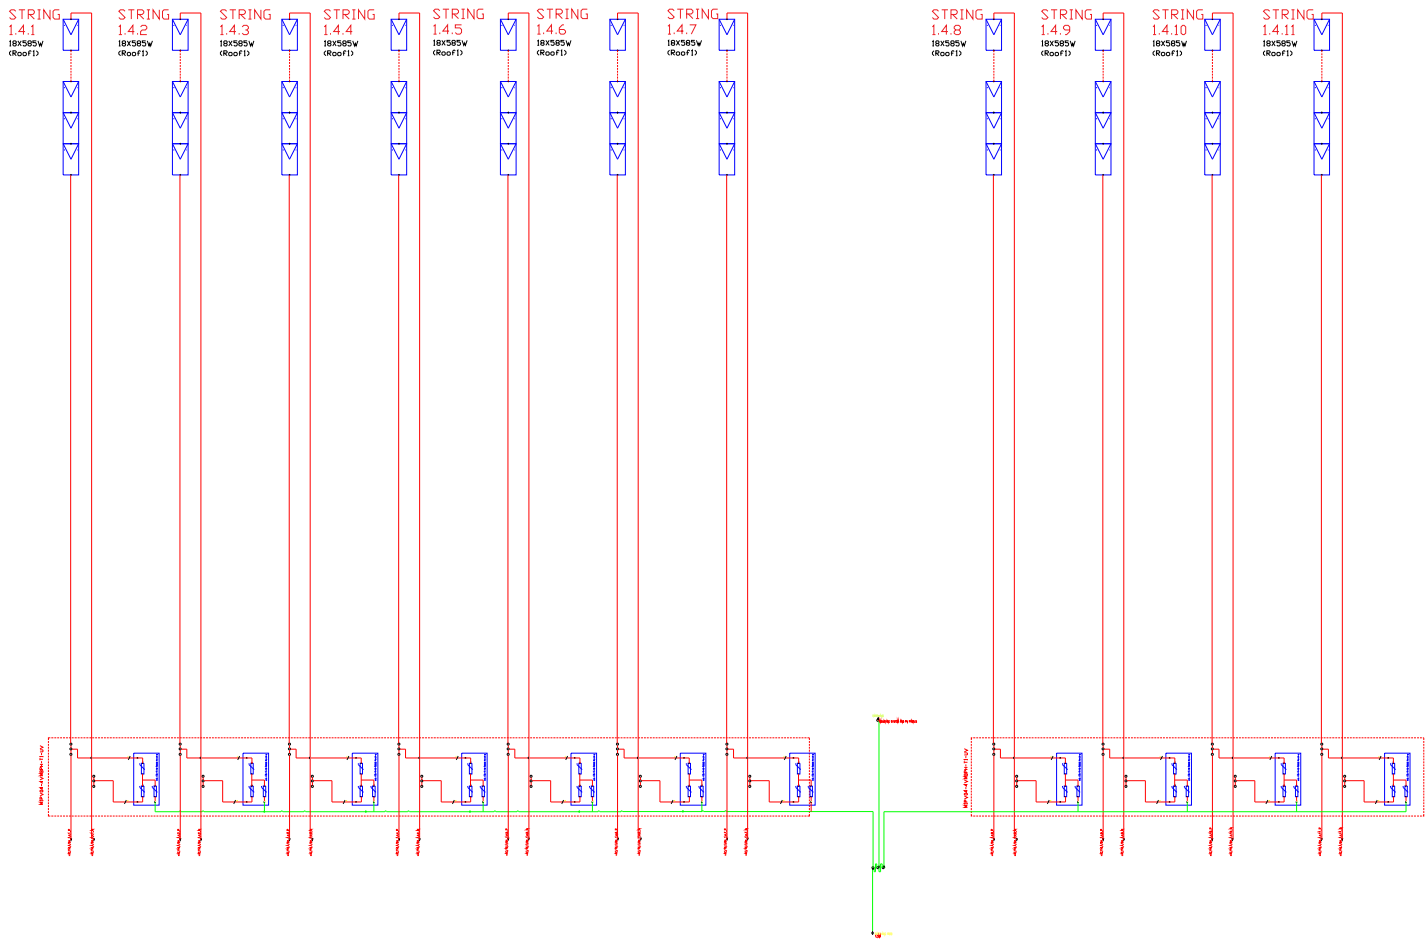


	Rooftop Solar System at Al-Falah-Industrial Campus		
	AL-FALAH INDUSTRIAL CAMPUS, DUBAI, UAE		
	Building D		
	SIZE	FSCM NO	DRAWING NUMBER 6	REV 1
	SCALE		SHEET 1

REVISIONS				

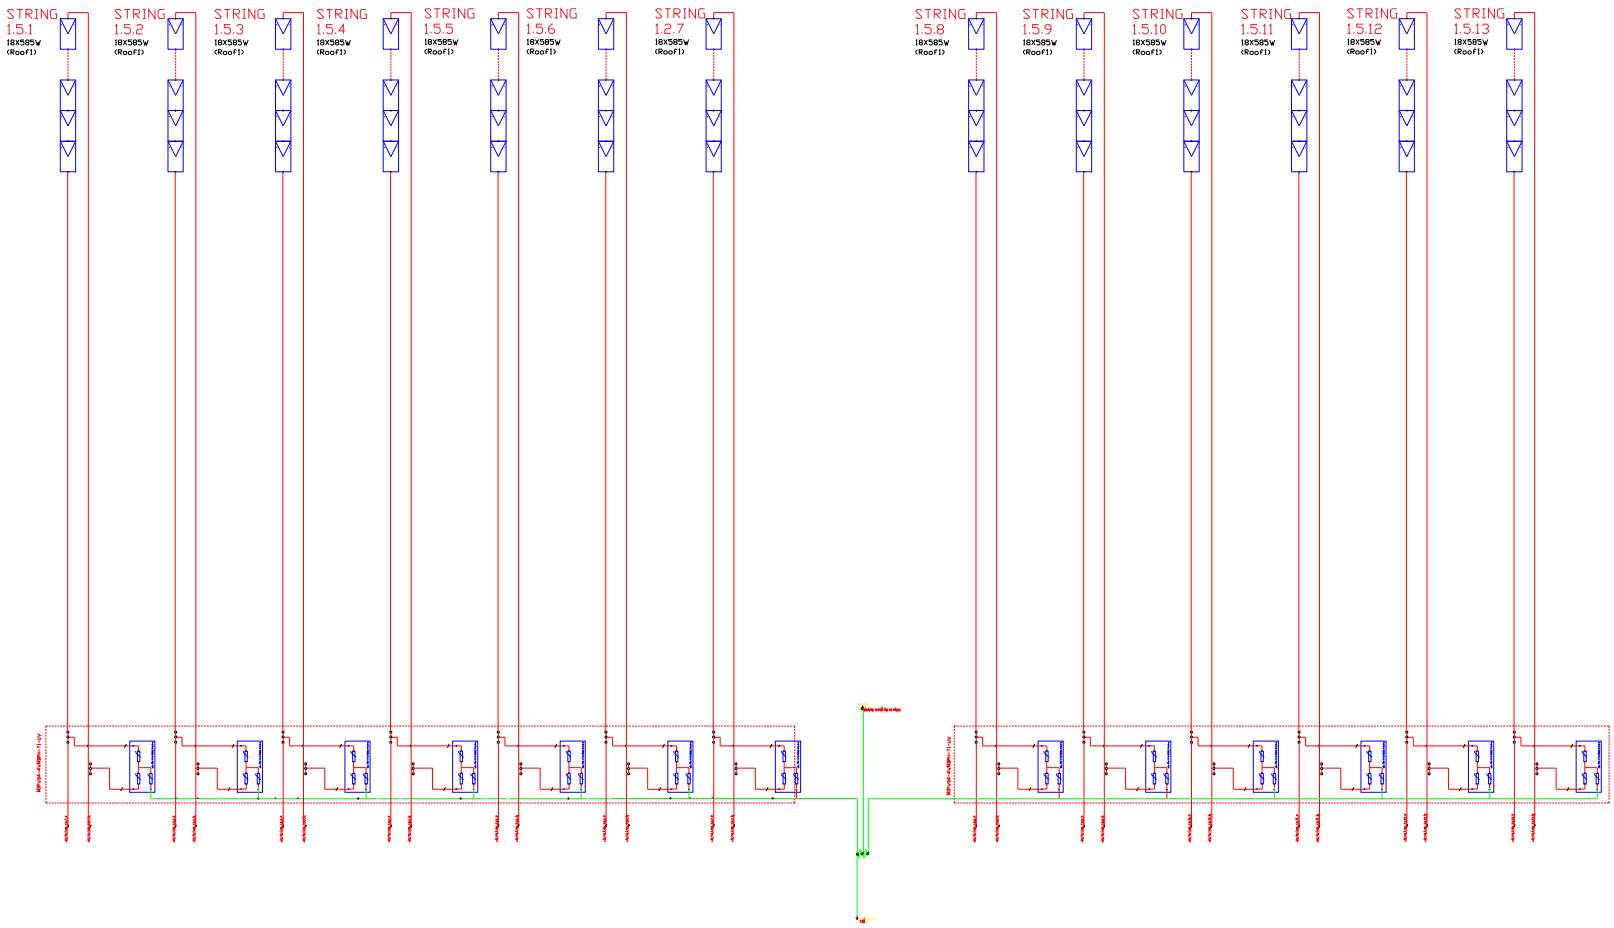


	Rooftop Solar System at Al-Falah-Industrial Campus			
	AL-FALAH INDUSTRIAL CAMPUS, DUBAI, UAE			
	Building E			
	SIZE	FSCM NO	DRAWING NUMBER 7	REV 1
	SCALE		SHEET 1	

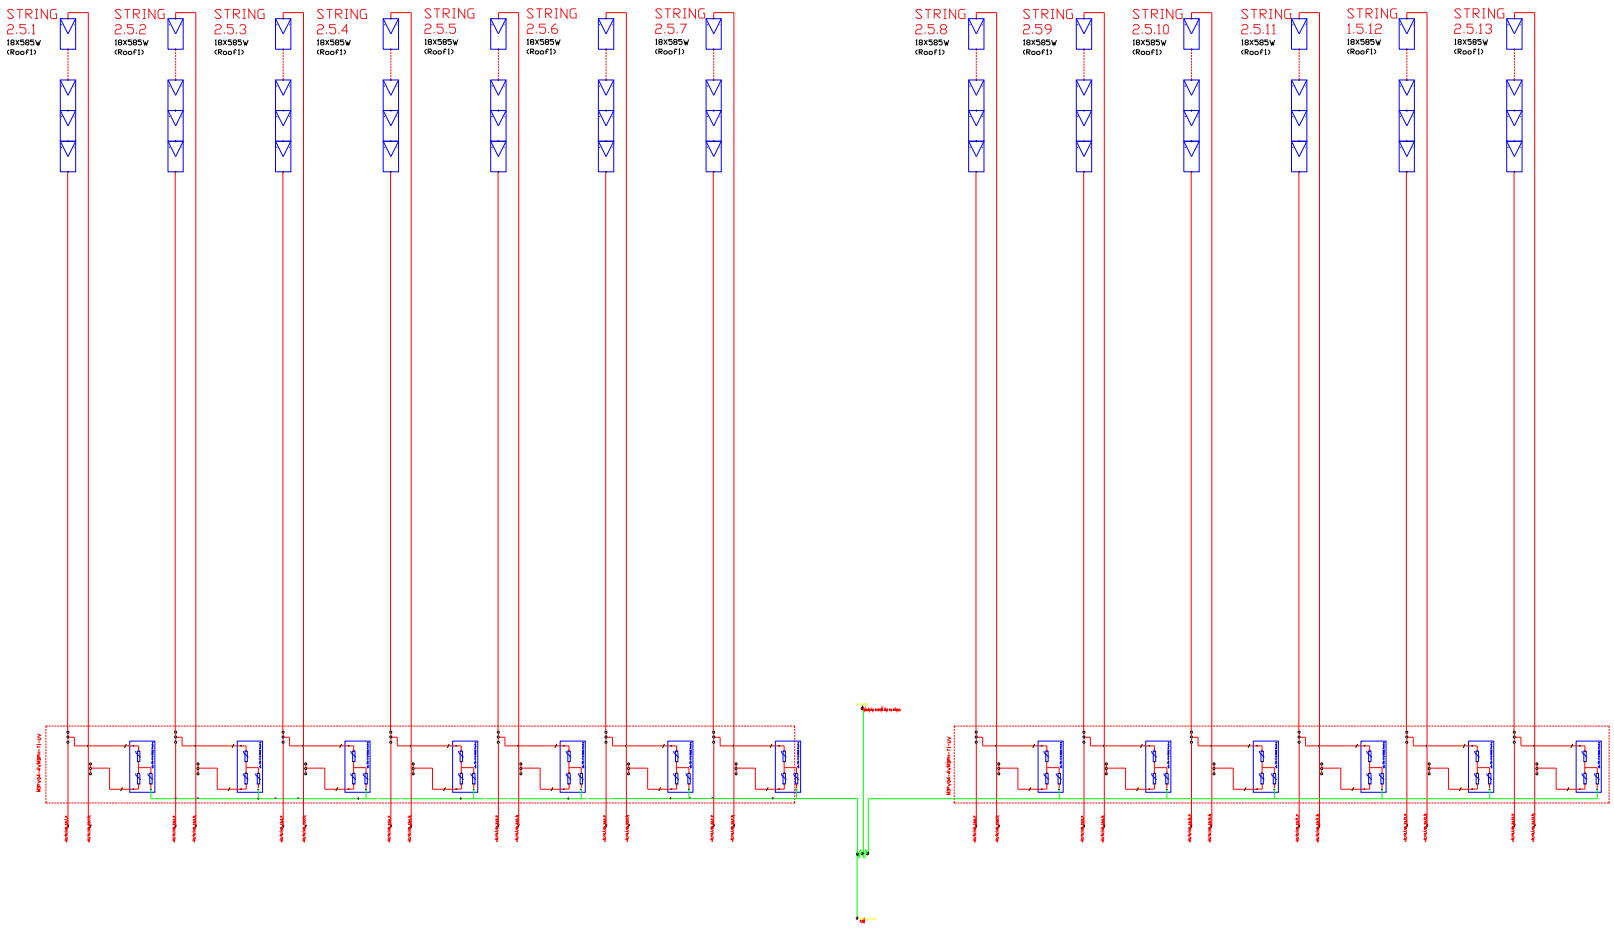


REVISIONS


	Rooftop Solar System at Al-Falah-Industrial Campus
	AL-FALAH INDUSTRIAL CAMPUS, DUBAI, UAE
	Building E
SIZE	FSCM NO / DRAWING NUMBER 8 / REV 1
SCALE	SHEET 1


REVISIONS

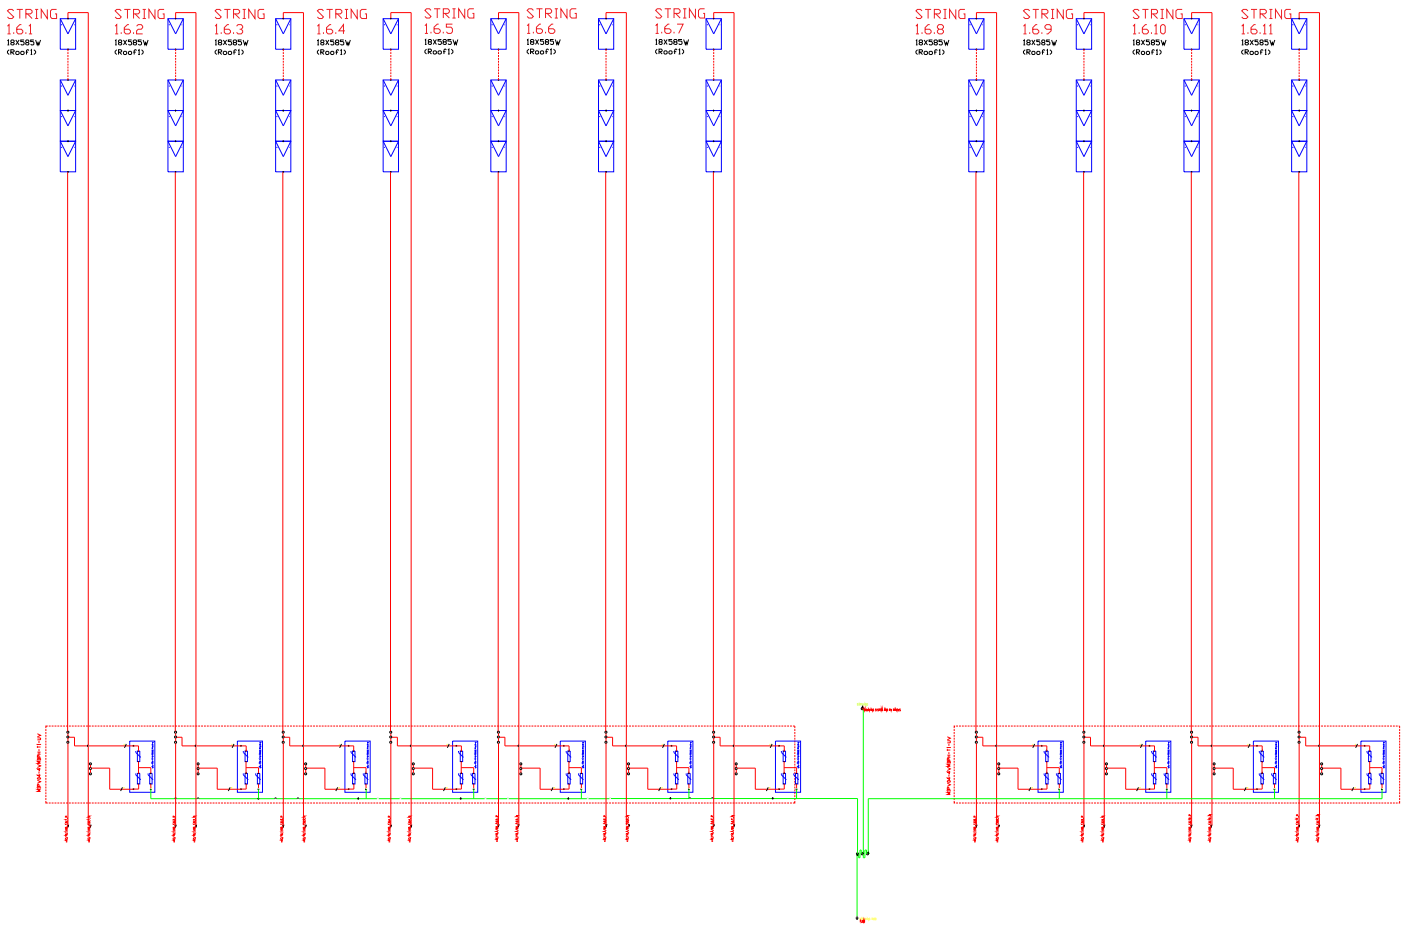



	Rooftop Solar System at Al-Falah-Industrial Campus
	AL-FALAH INDUSTRIAL CAMPUS, DUBAI, UAE
	Building F
SIZE / FSCM NO / DRAWING NUMBER 9 / REV 1	
SCALE / SHEET 1	

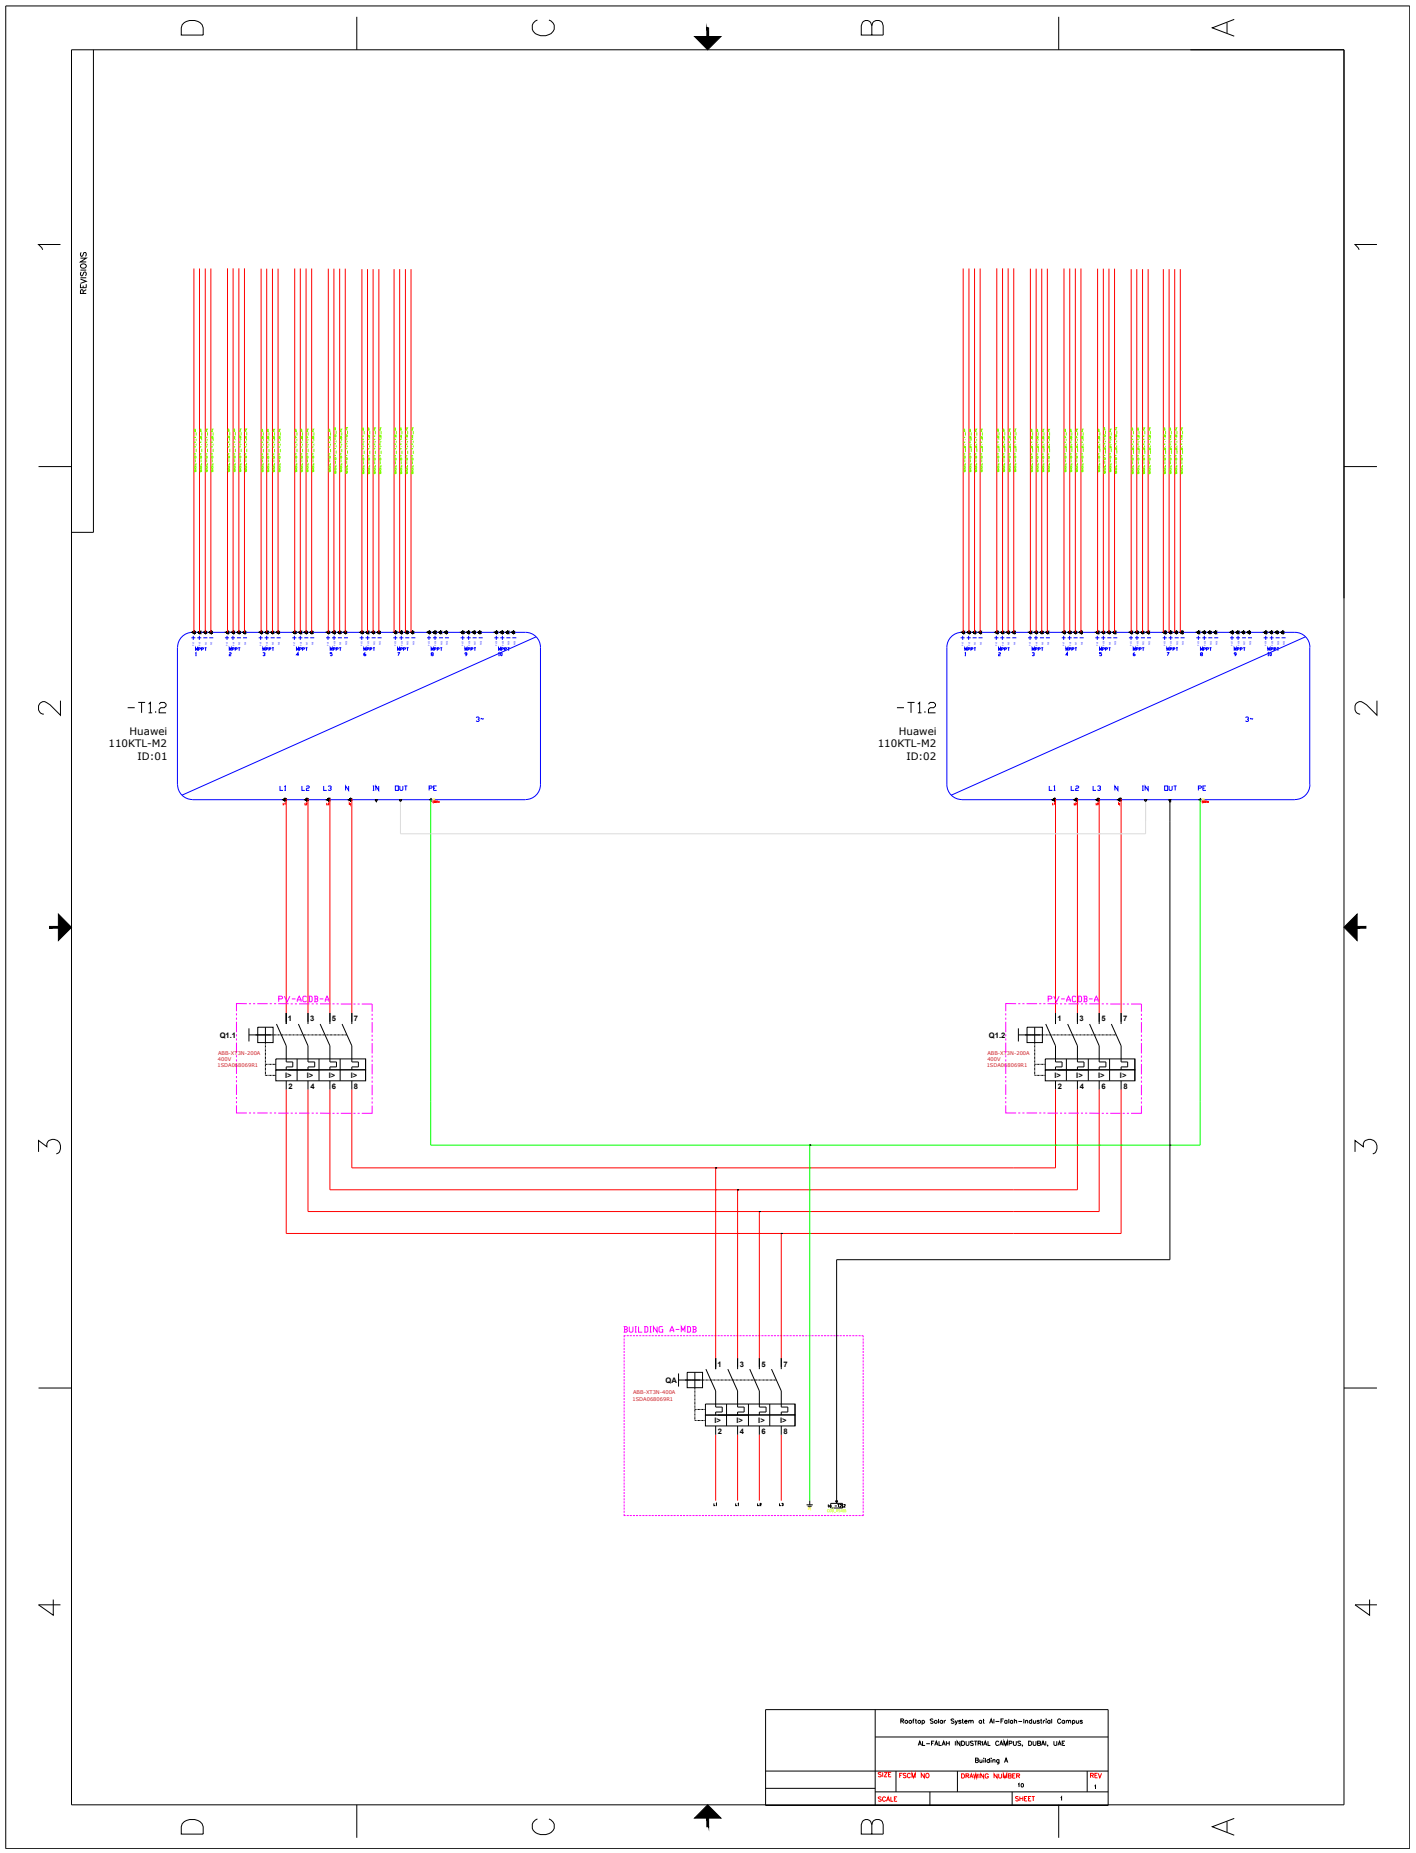

REVISIONS
-T1.2
Huawei
110KTL-M2
ID:01
-T1.2
Huawei
110KTL-M2
ID:02
L1 L2 L3 N IN OUT PE
PV-ACDB-A
Q1.1
Q1.2
BUILDING A-MDB
QA
Rooftop Solar System at Al-Falah-Industrial Campus
AL-FALAH INDUSTRIAL CAMPUS, DUBAI, UAE
Building A
SIZE
FSCM NO
DRAWING NUMBER
10
REV
1
SCALE
SHEET
1

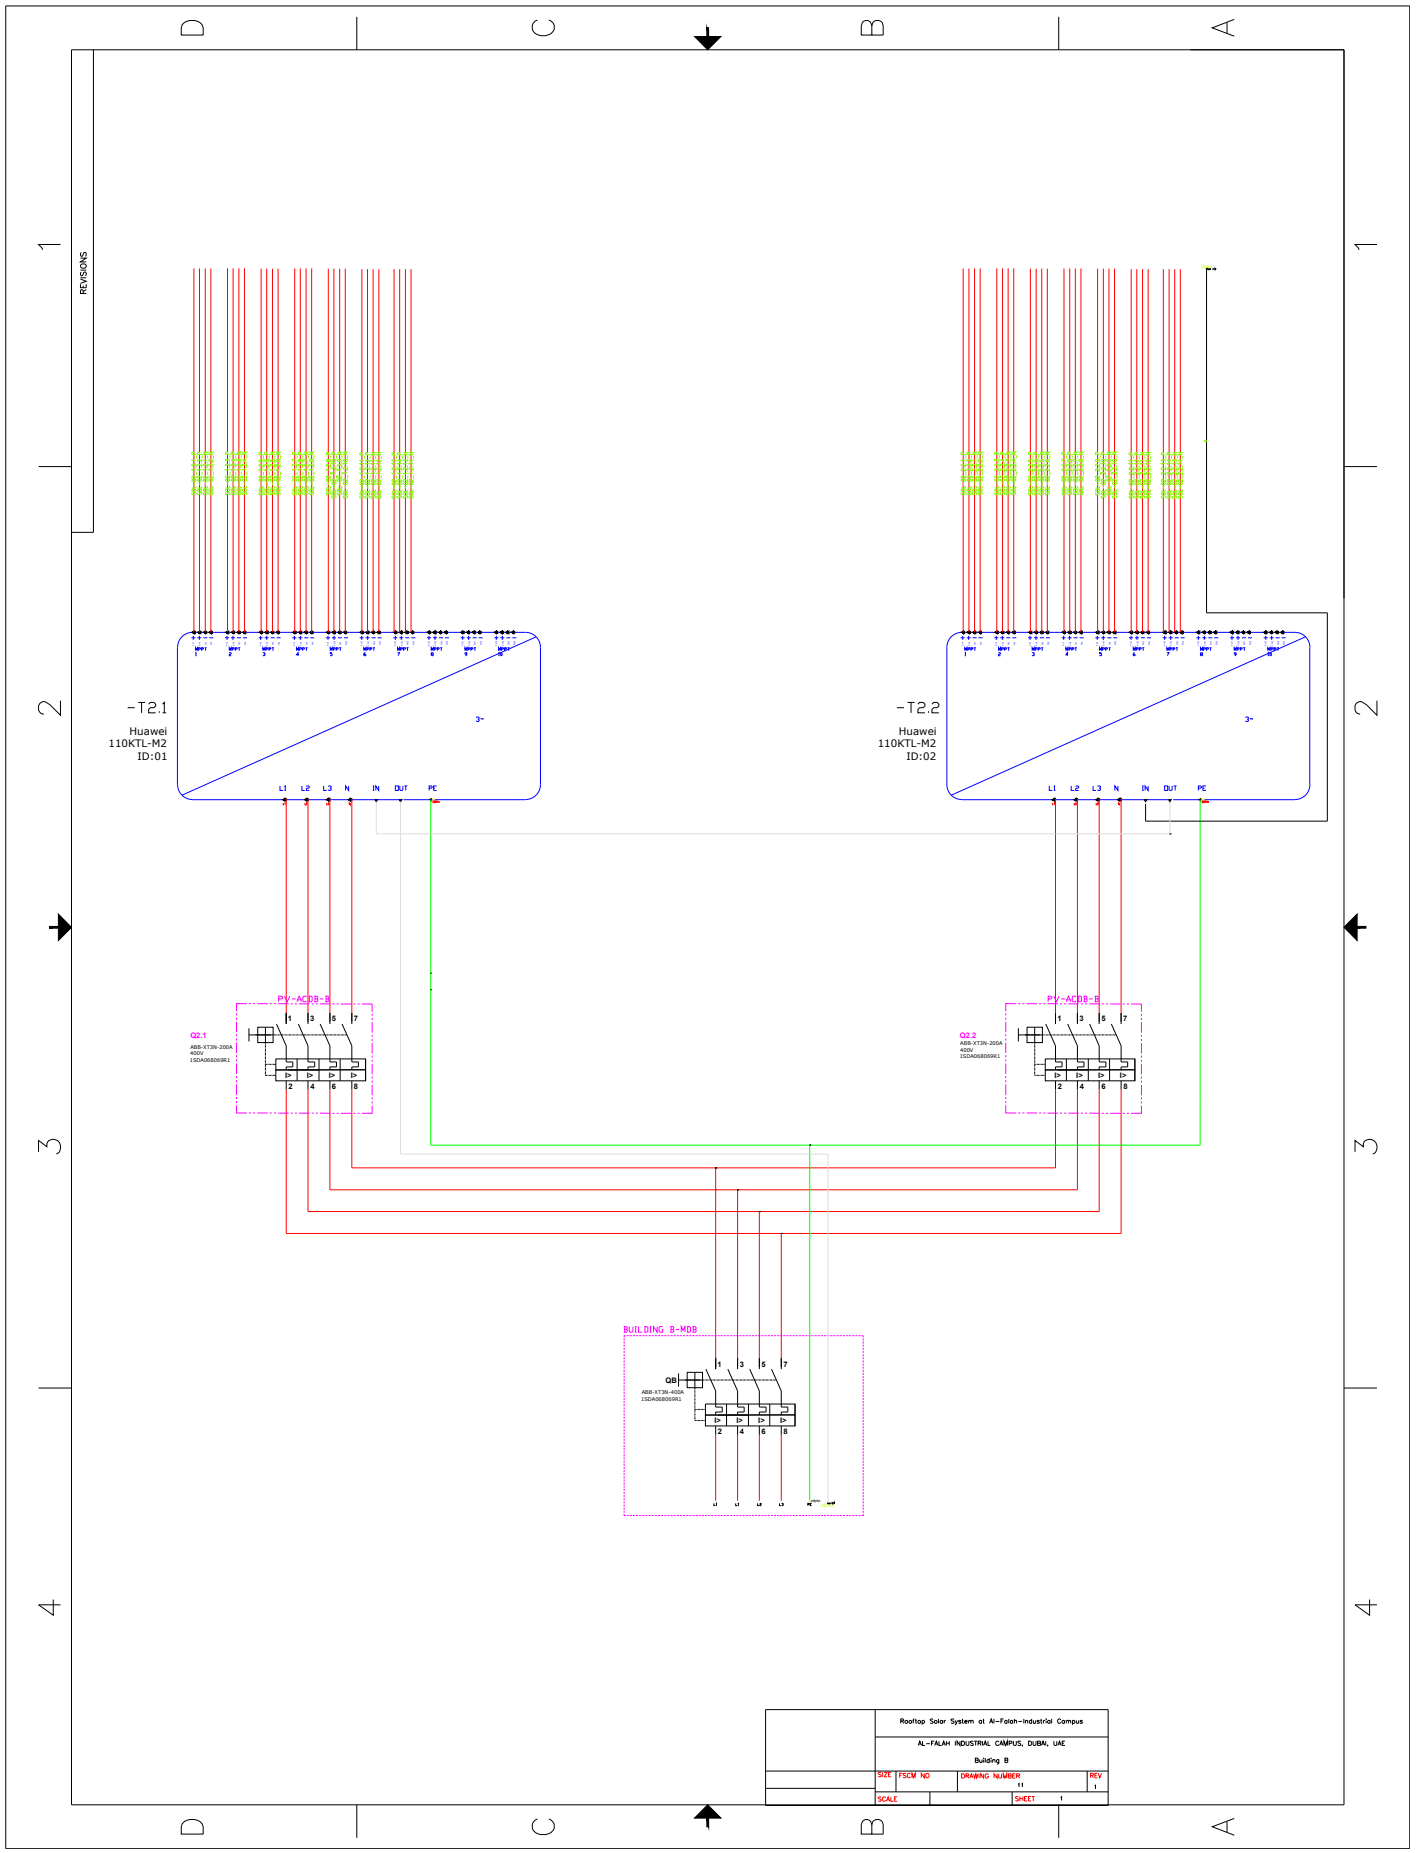

REVISIONS
-T2.1
Huawei
110KTL-M2
ID:01
-T2.2
Huawei
110KTL-M2
ID:02
L1 L2 L3 N IN OUT PE
PV-ACDB-B
Q2.1
Q2.2
BUILDING B-MDB
QB
Rooftop Solar System at Al-Falah-Industrial Campus
AL-FALAH INDUSTRIAL CAMPUS, DUBAI, UAE
Building B
SIZE
FSCM NO
DRAWING NUMBER
REV
SCALE
SHEET

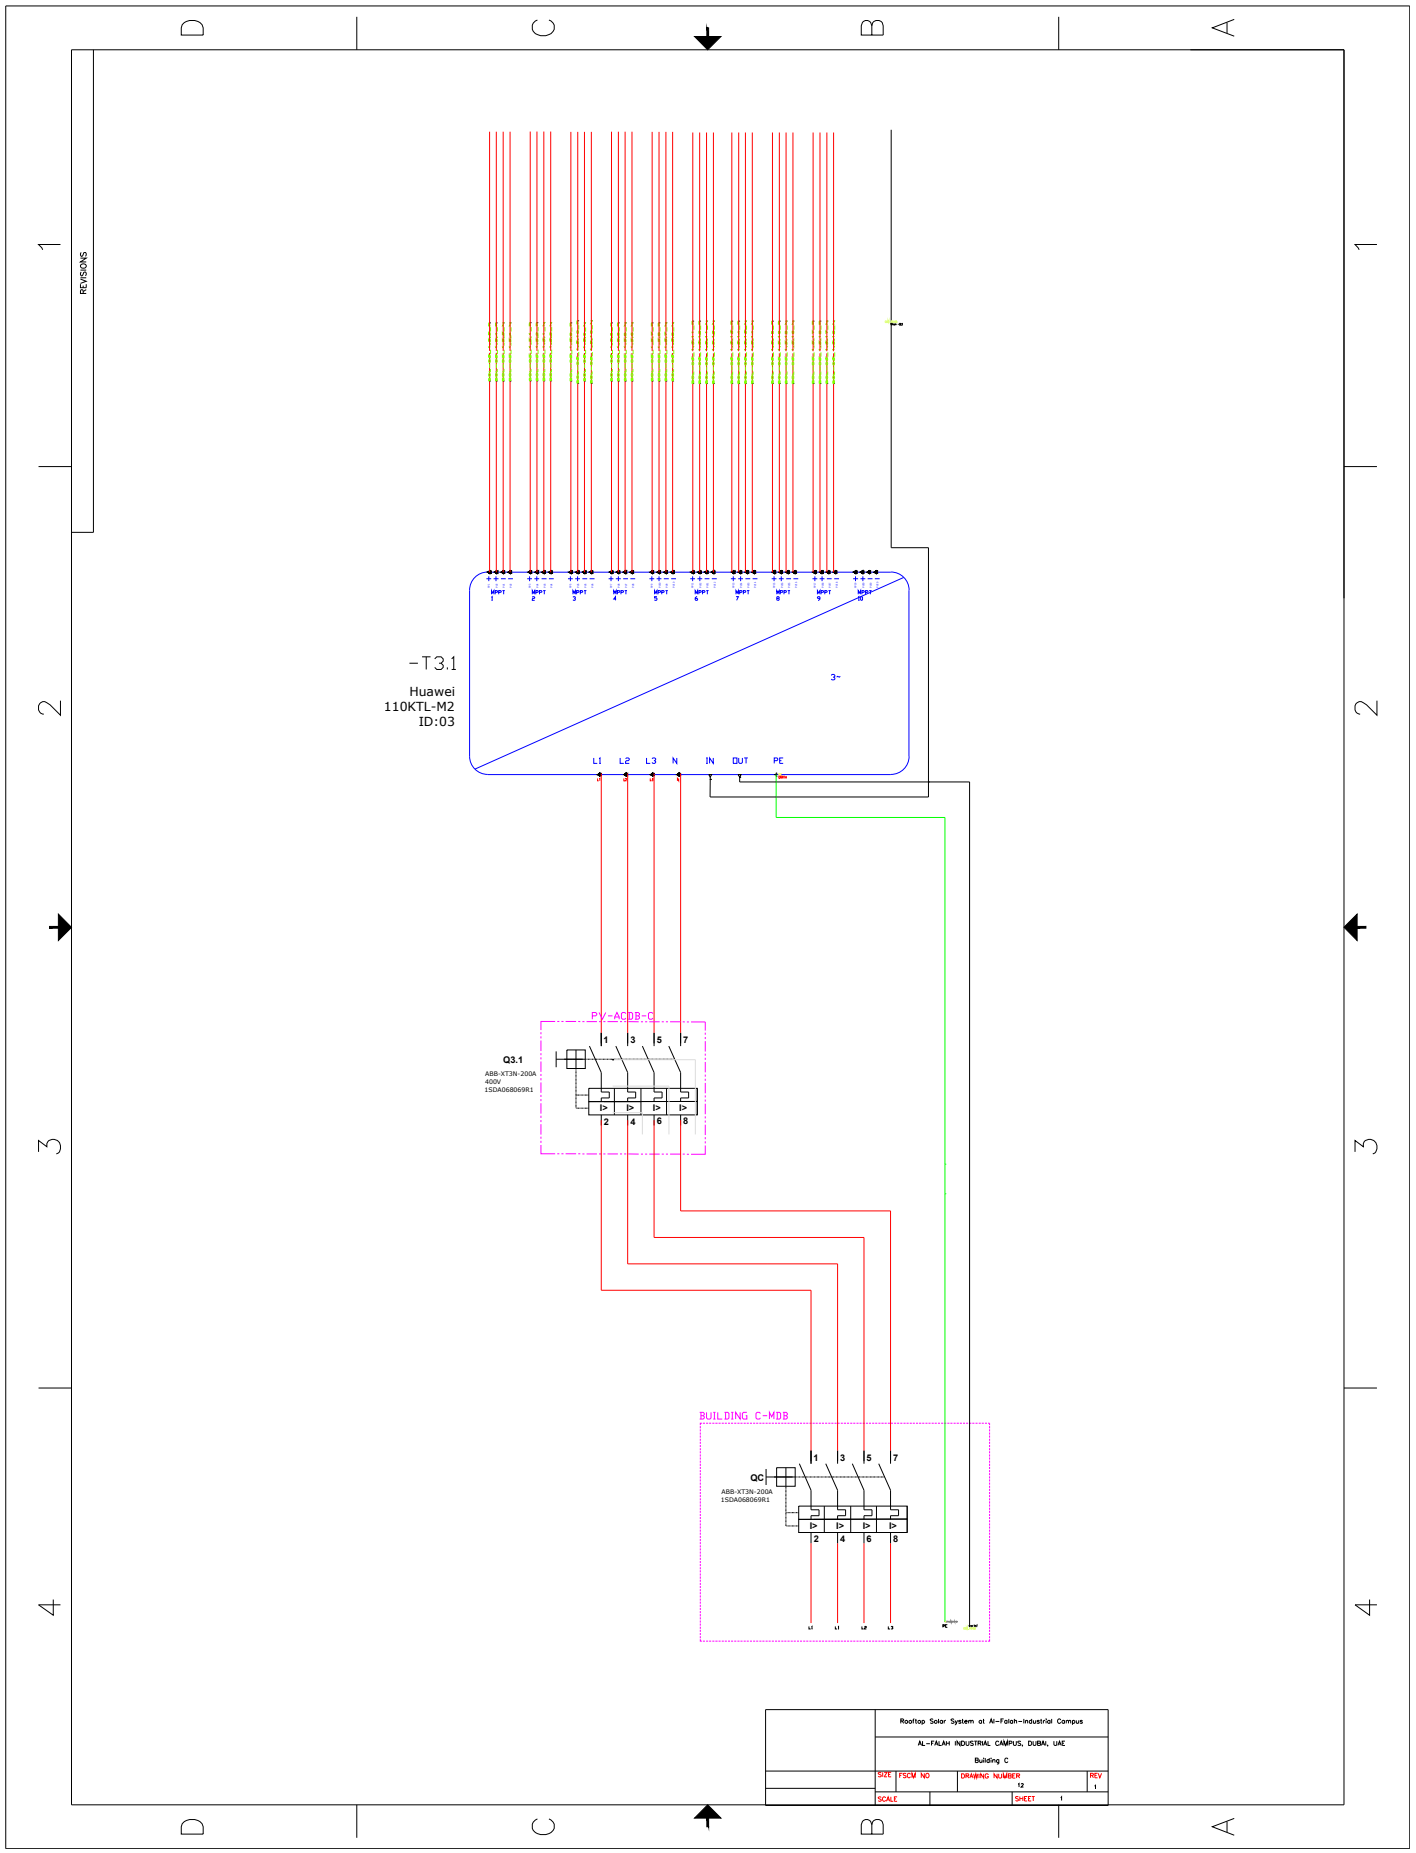
REVISIONS
-T3.1
Huawei
110KTL-M2
ID:03
L1 L2 L3 N IN OUT PE
PV-ACDB-C
Q3.1
ABB-XT3N-200A
400V
1SDA068069R1
BUILDING C-MDB
QC
ABB-XT3N-200A
1SDA068069R1
Rooftop Solar System at Al-Falah-Industrial Campus
AL-FALAH INDUSTRIAL CAMPUS, DUBAI, UAE
Building C
SIZE
FSCM NO
DRAWING NUMBER
12
REV
1
SCALE
SHEET
1

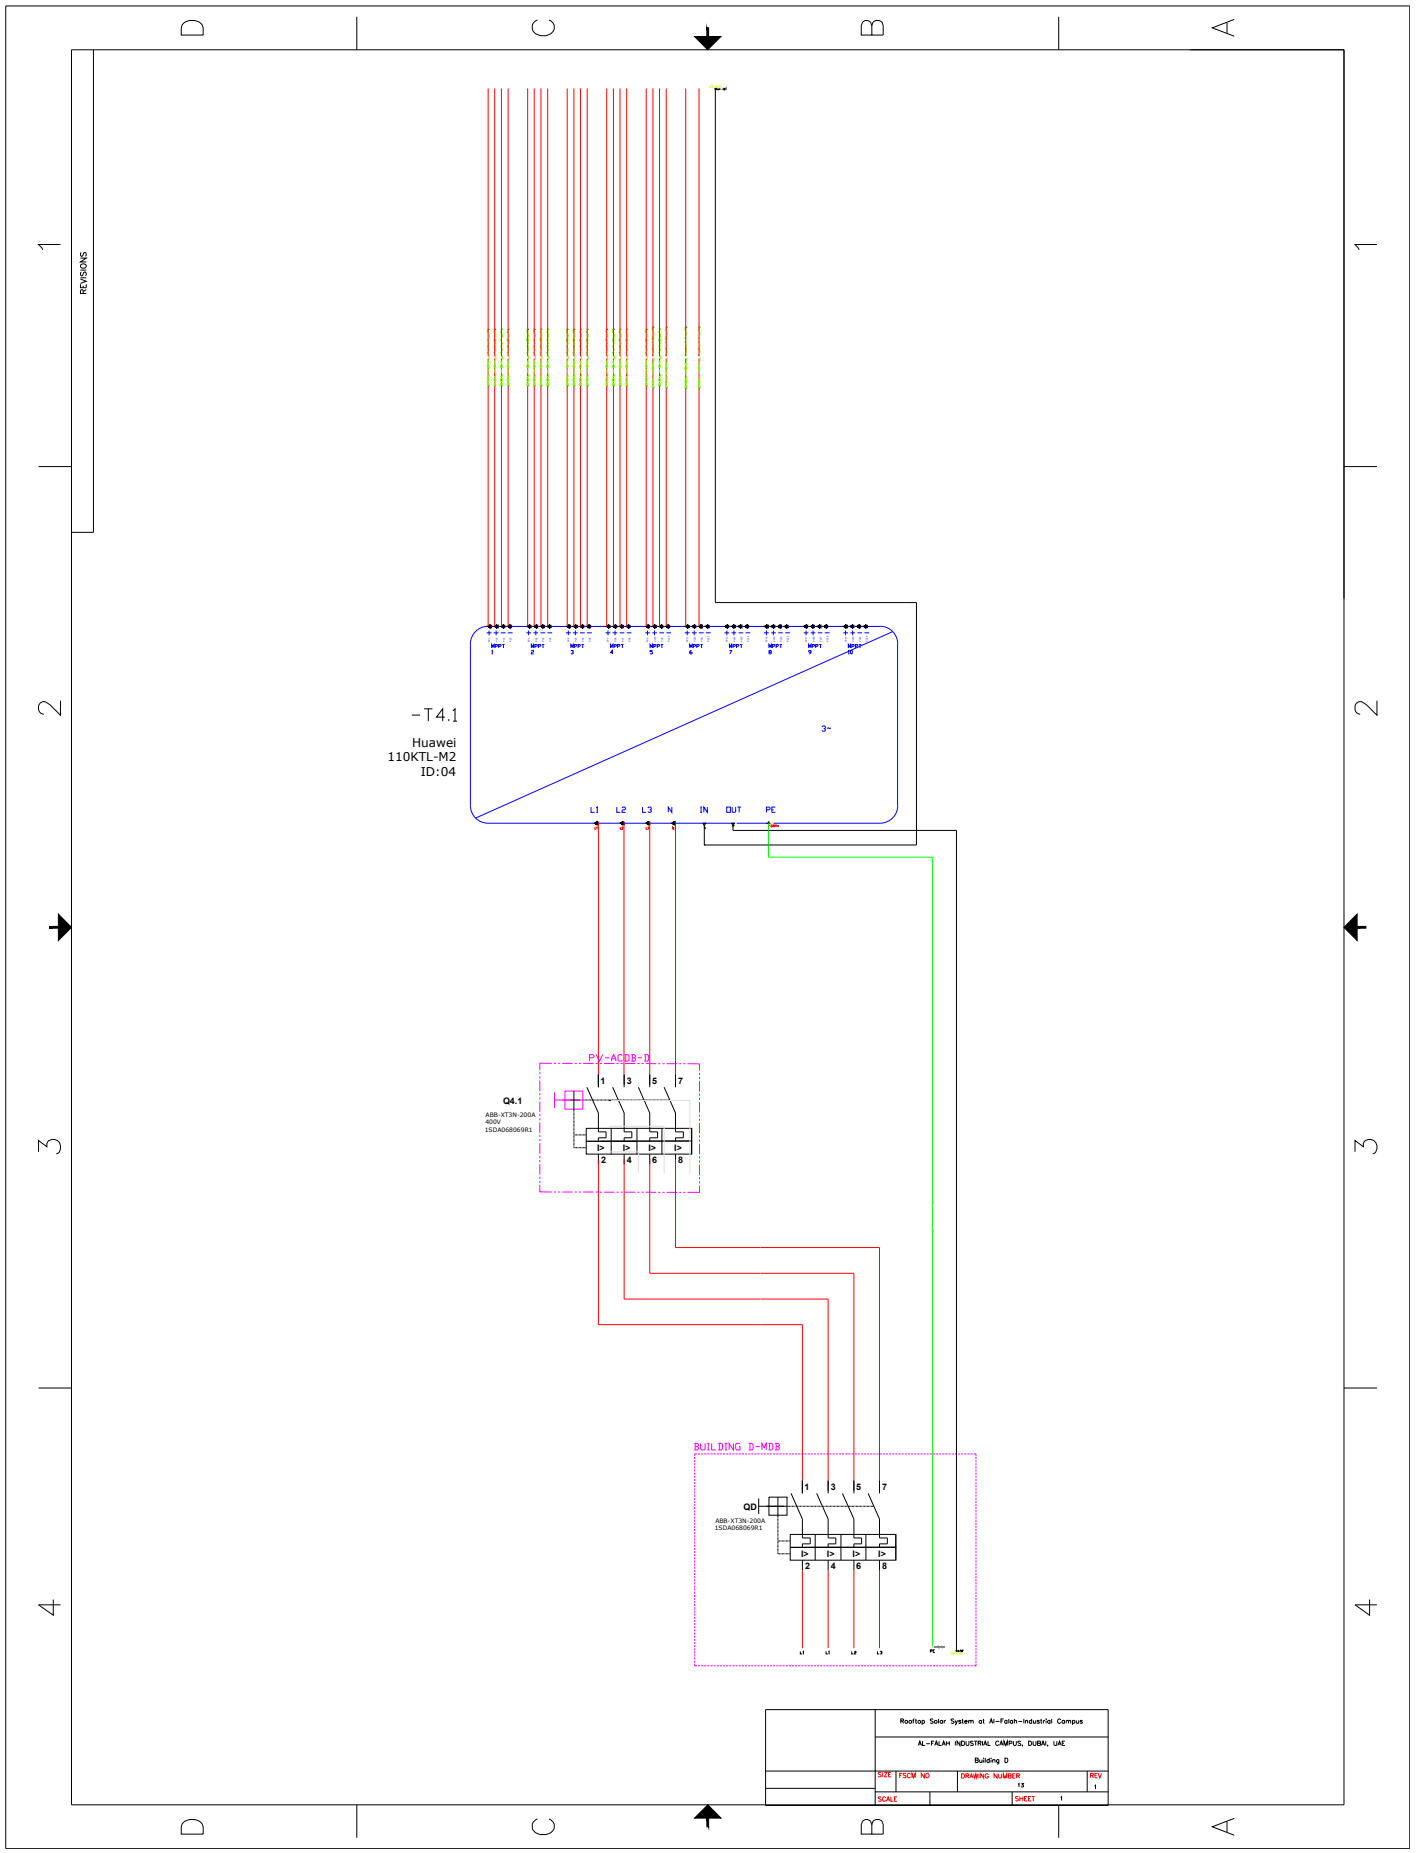
REVISIONS
-T4.1
Huawei
110KTL-M2
ID:04
3~
L1 L2 L3 N IN OUT PE
PV-ACDB-D
Q4.1
ABB-XT3N-200A
400V
1SDA068069R1
BUILDING D-MDB
QD
ABB-XT3N-200A
1SDA068069R1
Rooftop Solar System at Al-Falah-Industrial Campus
AL-FALAH INDUSTRIAL CAMPUS, DUBAI, UAE
Building D
SIZE
FSCM NO
DRAWING NUMBER
REV
SCALE
SHEET

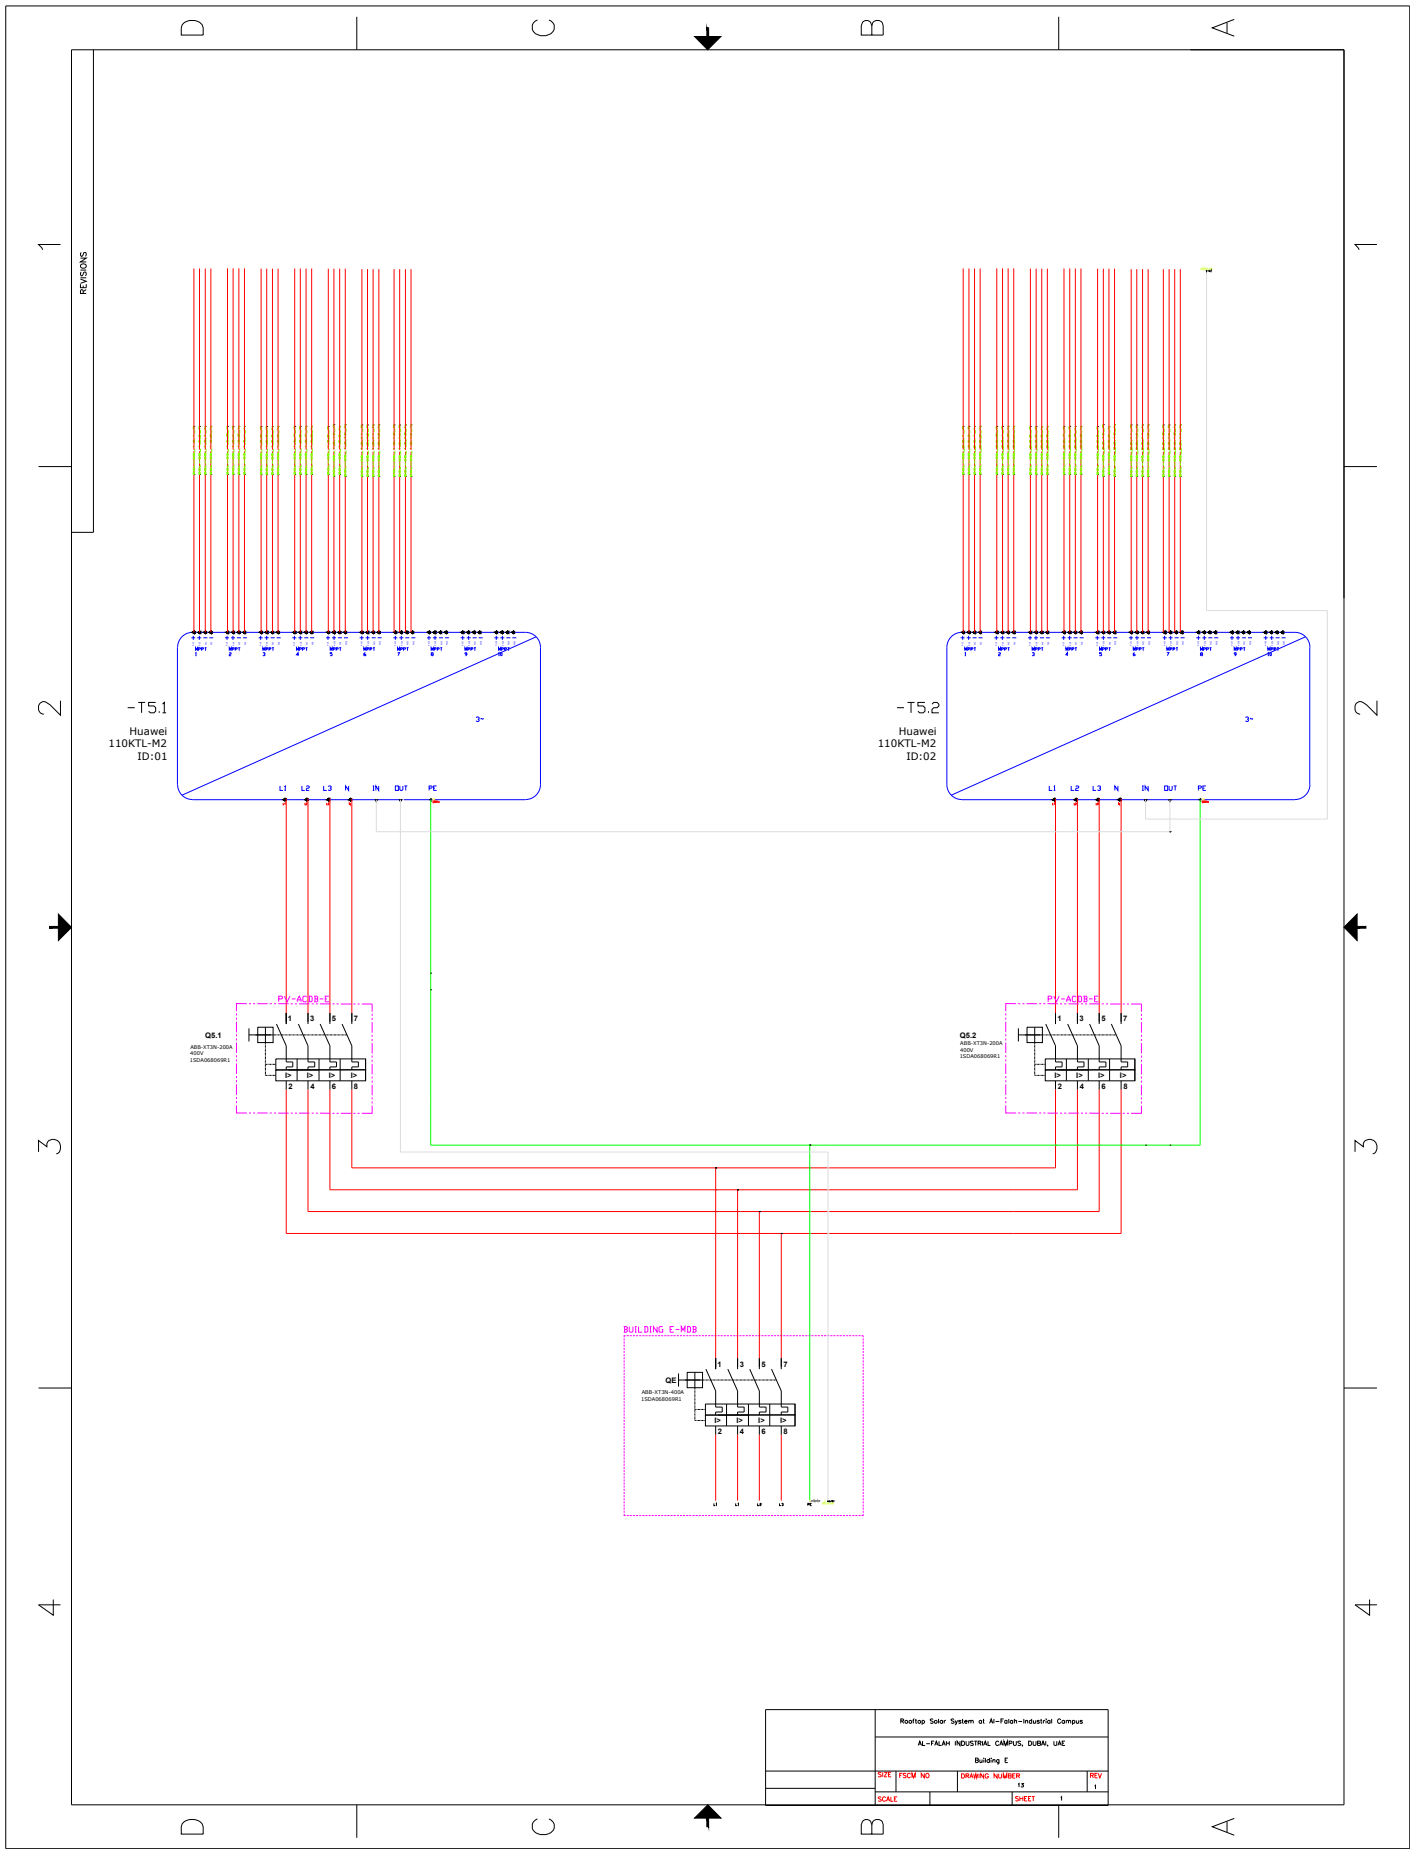
REVISIONS
-T5.1
Huawei
110KTL-M2
ID:01
-T5.2
Huawei
110KTL-M2
ID:02
L1 L2 L3 N IN OUT PE
PV-ACDB-E
Q5.1
Q5.2
BUILDING E-MDB
QE
Rooftop Solar System at Al-Falah-Industrial Campus
AL-FALAH INDUSTRIAL CAMPUS, DUBAI, UAE
Building E
SIZE
FSCM NO
DRAWING NUMBER
REV
SCALE
SHEET

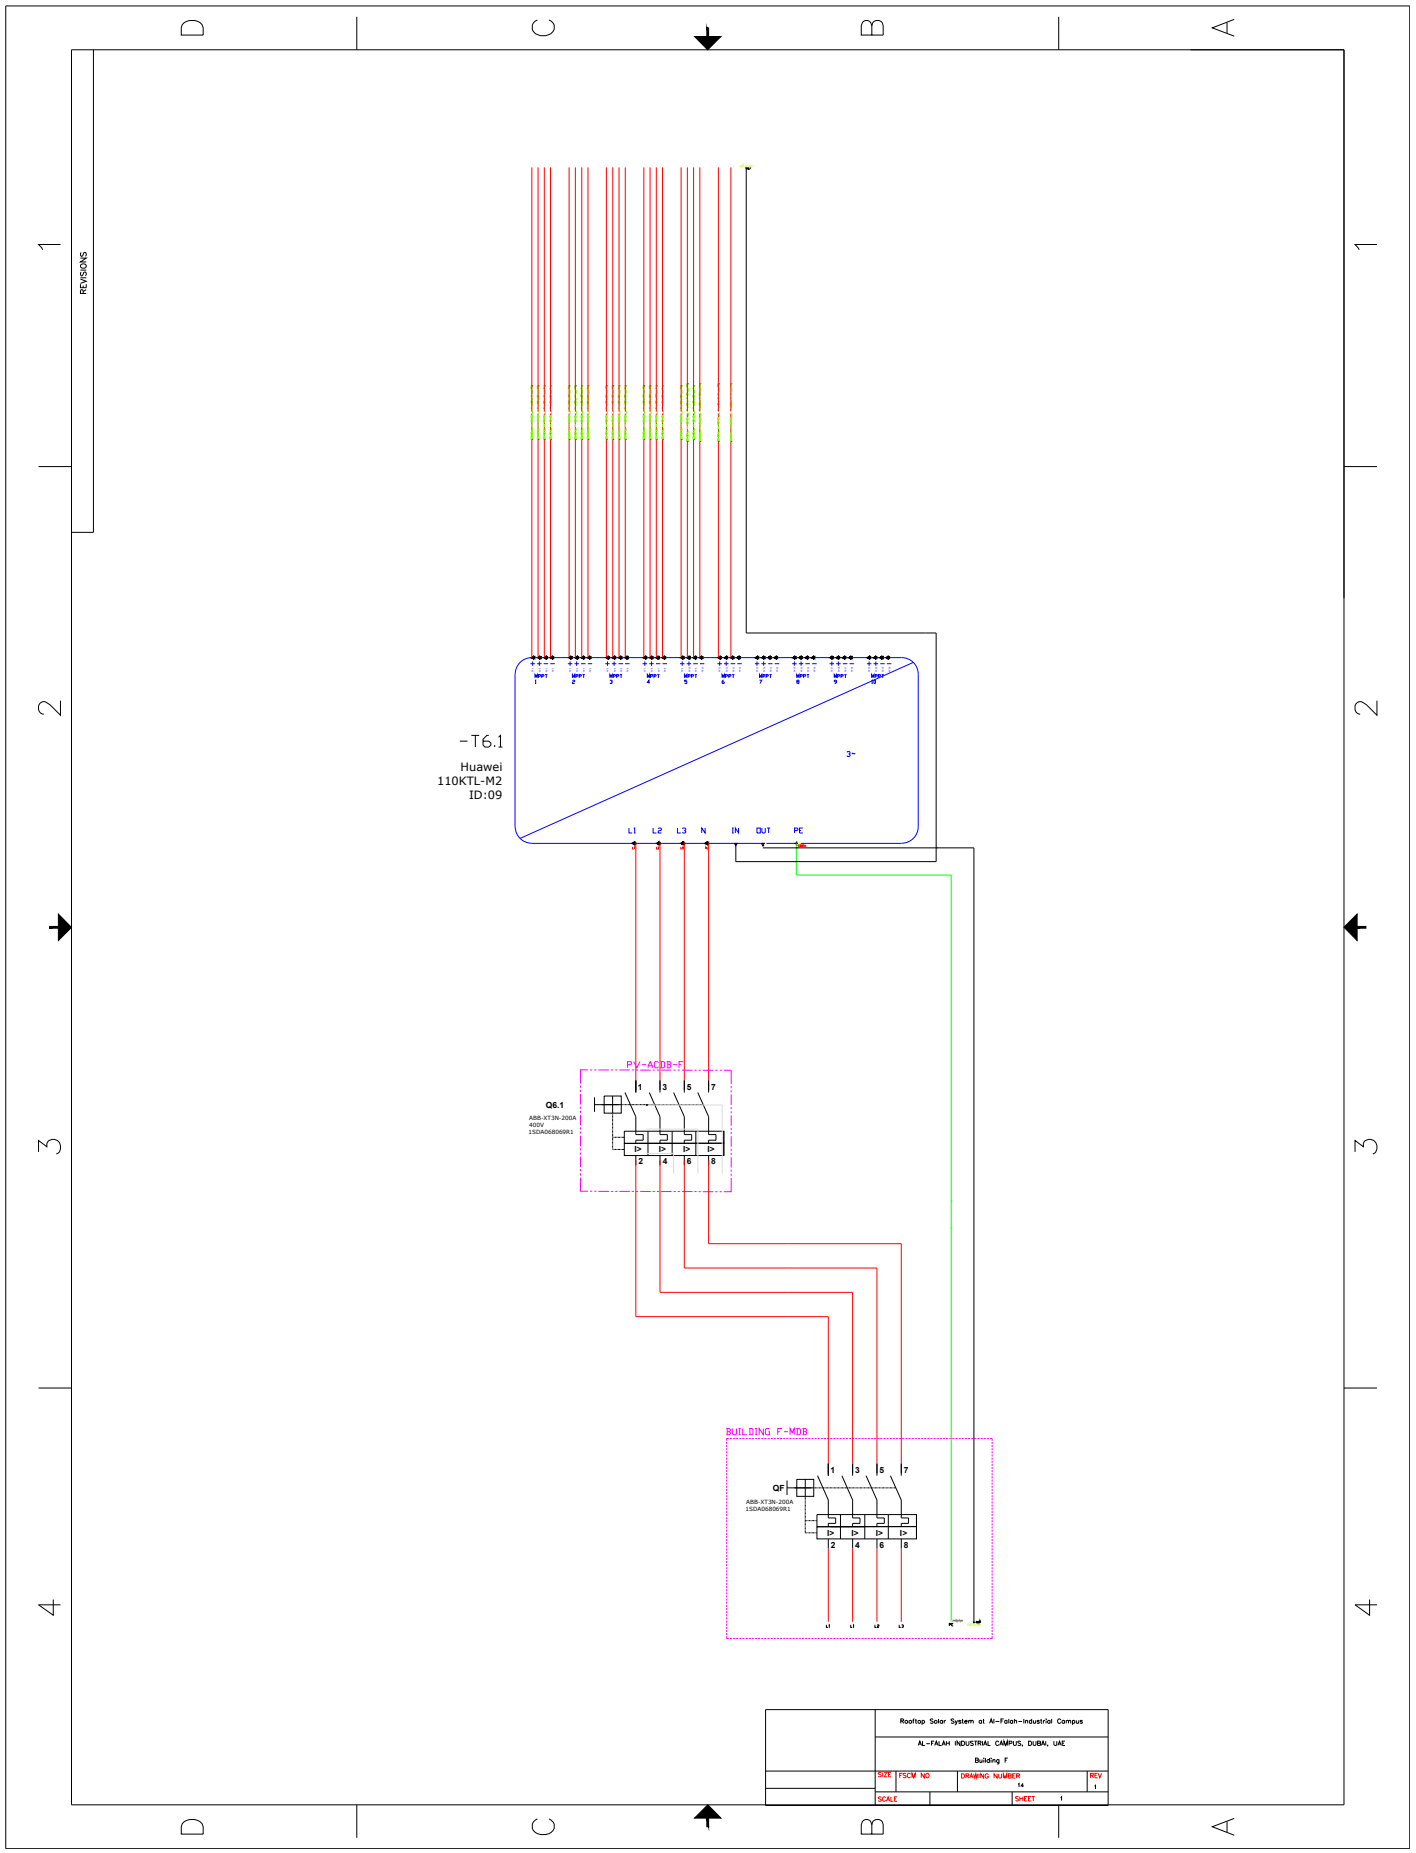
REVISIONS
-T6.1
Huawei
110KTL-M2
ID:09
L1 L2 L3 N IN OUT PE
PV-ACDB-F
Q6.1
ABB-XT3N-200A
400V
1SDA068069R1
BUILDING F-MDB
QF
ABB-XT3N-200A
1SDA068069R1
Rooftop Solar System at Al-Falah-Industrial Campus
AL-FALAH INDUSTRIAL CAMPUS, DUBAI, UAE
Building F
SIZE
FSCM NO
DRAWING NUMBER
14
REV
1
SCALE
SHEET
1

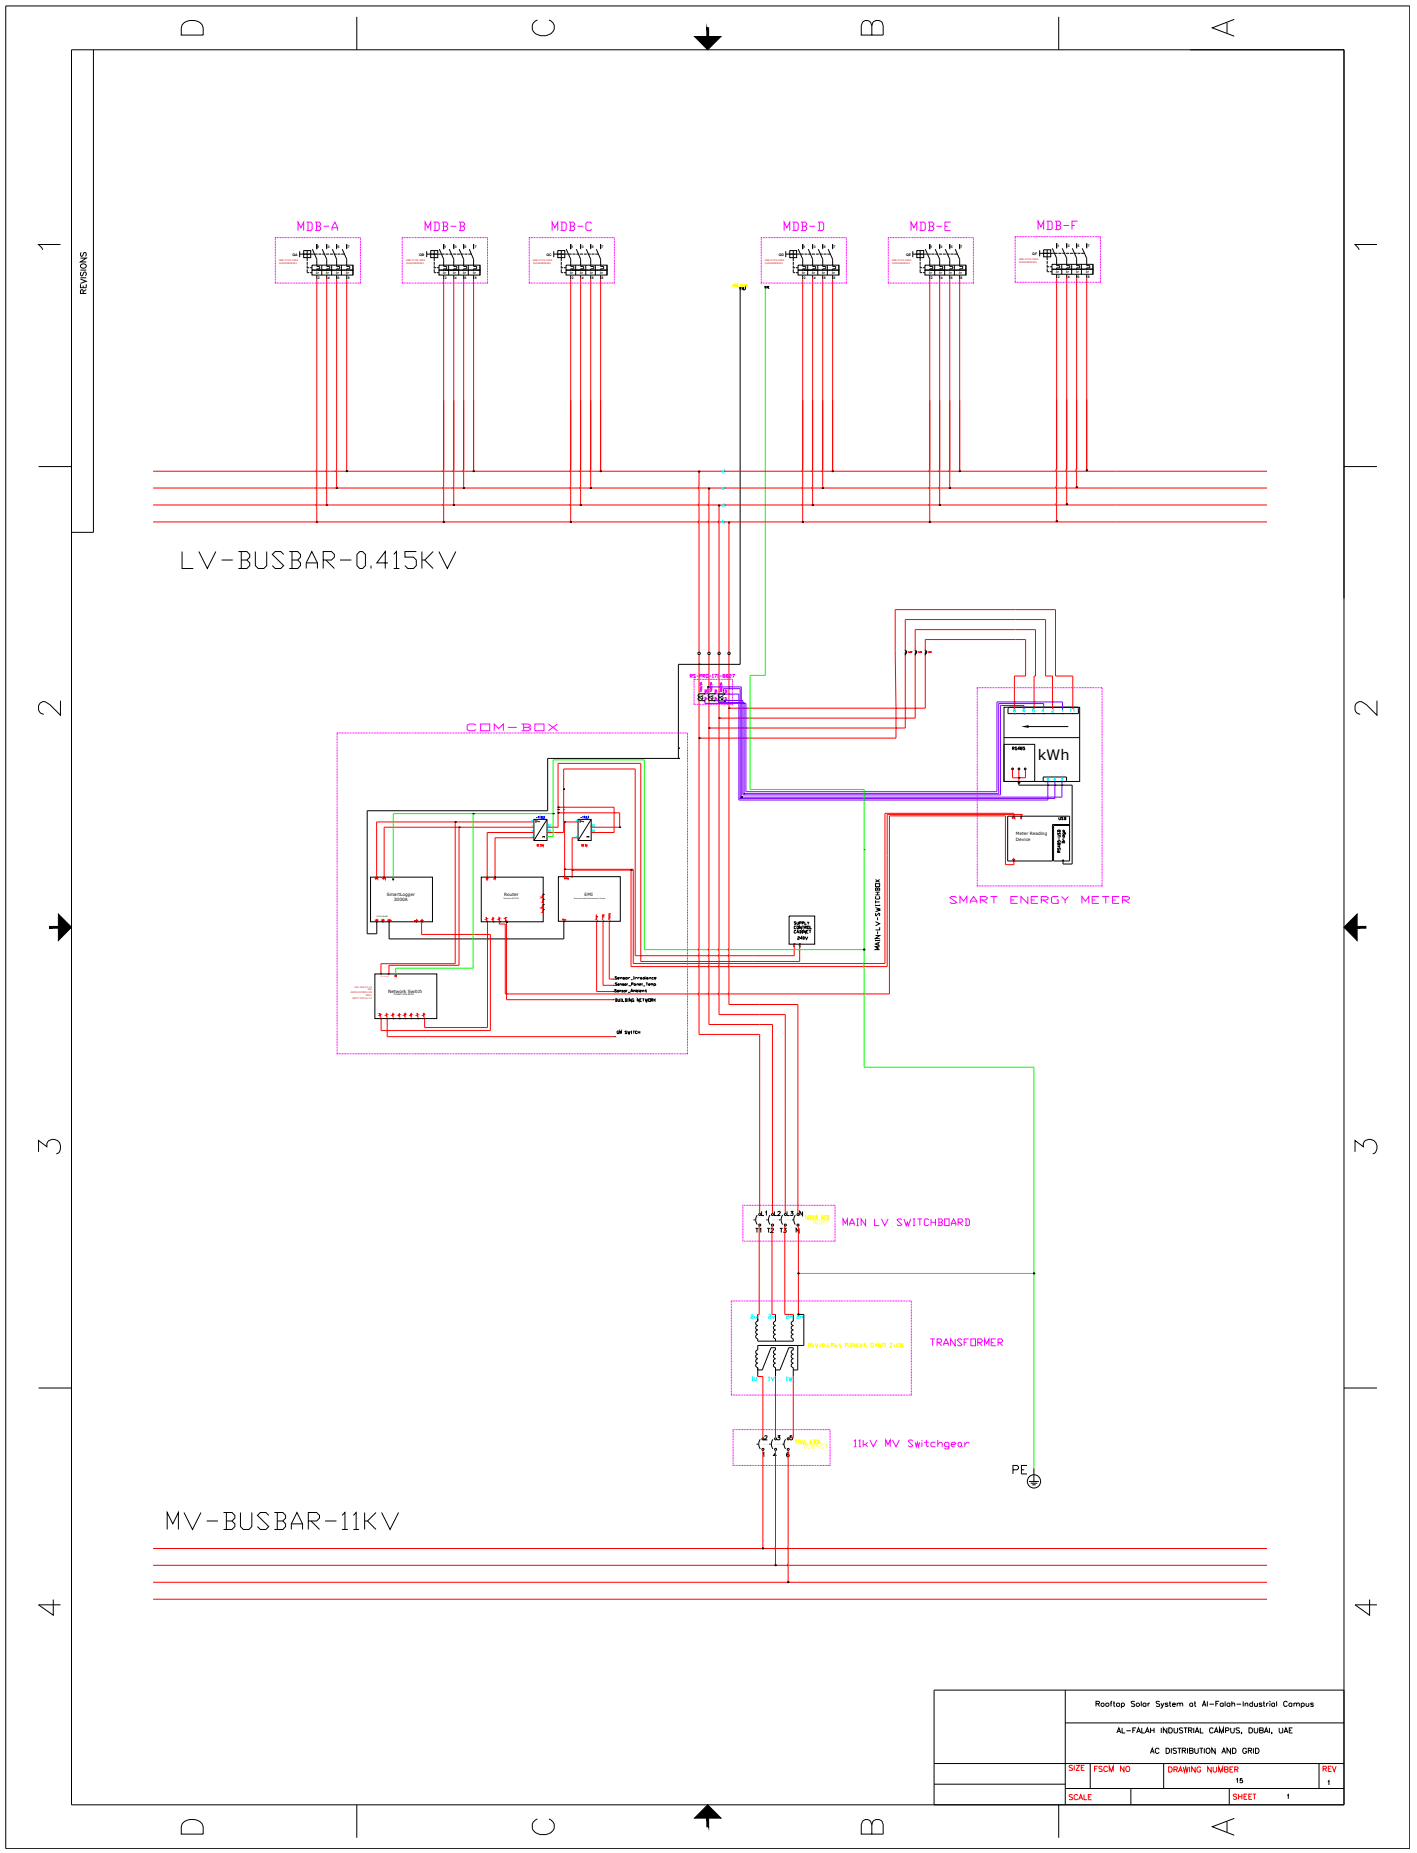
MDB-A
MDB-B
MDB-C
MDB-D
MDB-E
MDB-F
LV-BUSBAR-0.415KV
COM-BOX
kWh
SMART ENERGY METER
MAIN-LV-SWITCHES
MAIN LV SWITCHBOARD
TRANSFORMER
11kV MV Switchgear
PE
MV-BUSBAR-11KV
REVISIONS
Rooftop Solar System at Al-Falah-Industrial Campus
AL-FALAH INDUSTRIAL CAMPUS, DUBAI, UAE
AC DISTRIBUTION AND GRID
SIZE
FSCM NO
DRAWING NUMBER
15
REV
SCALE
SHEET