PROJECT: AL-FATAH PRISMA MALL


Solar Energy System Wiring Diagram

660kW Solar Energy System with 863.4kWp PV


LET THE SUN PAY YOUR BILL

Engr. M Usama Rafique
usama.rafique@billsun.com


SINGLE LINE DIAGRAM

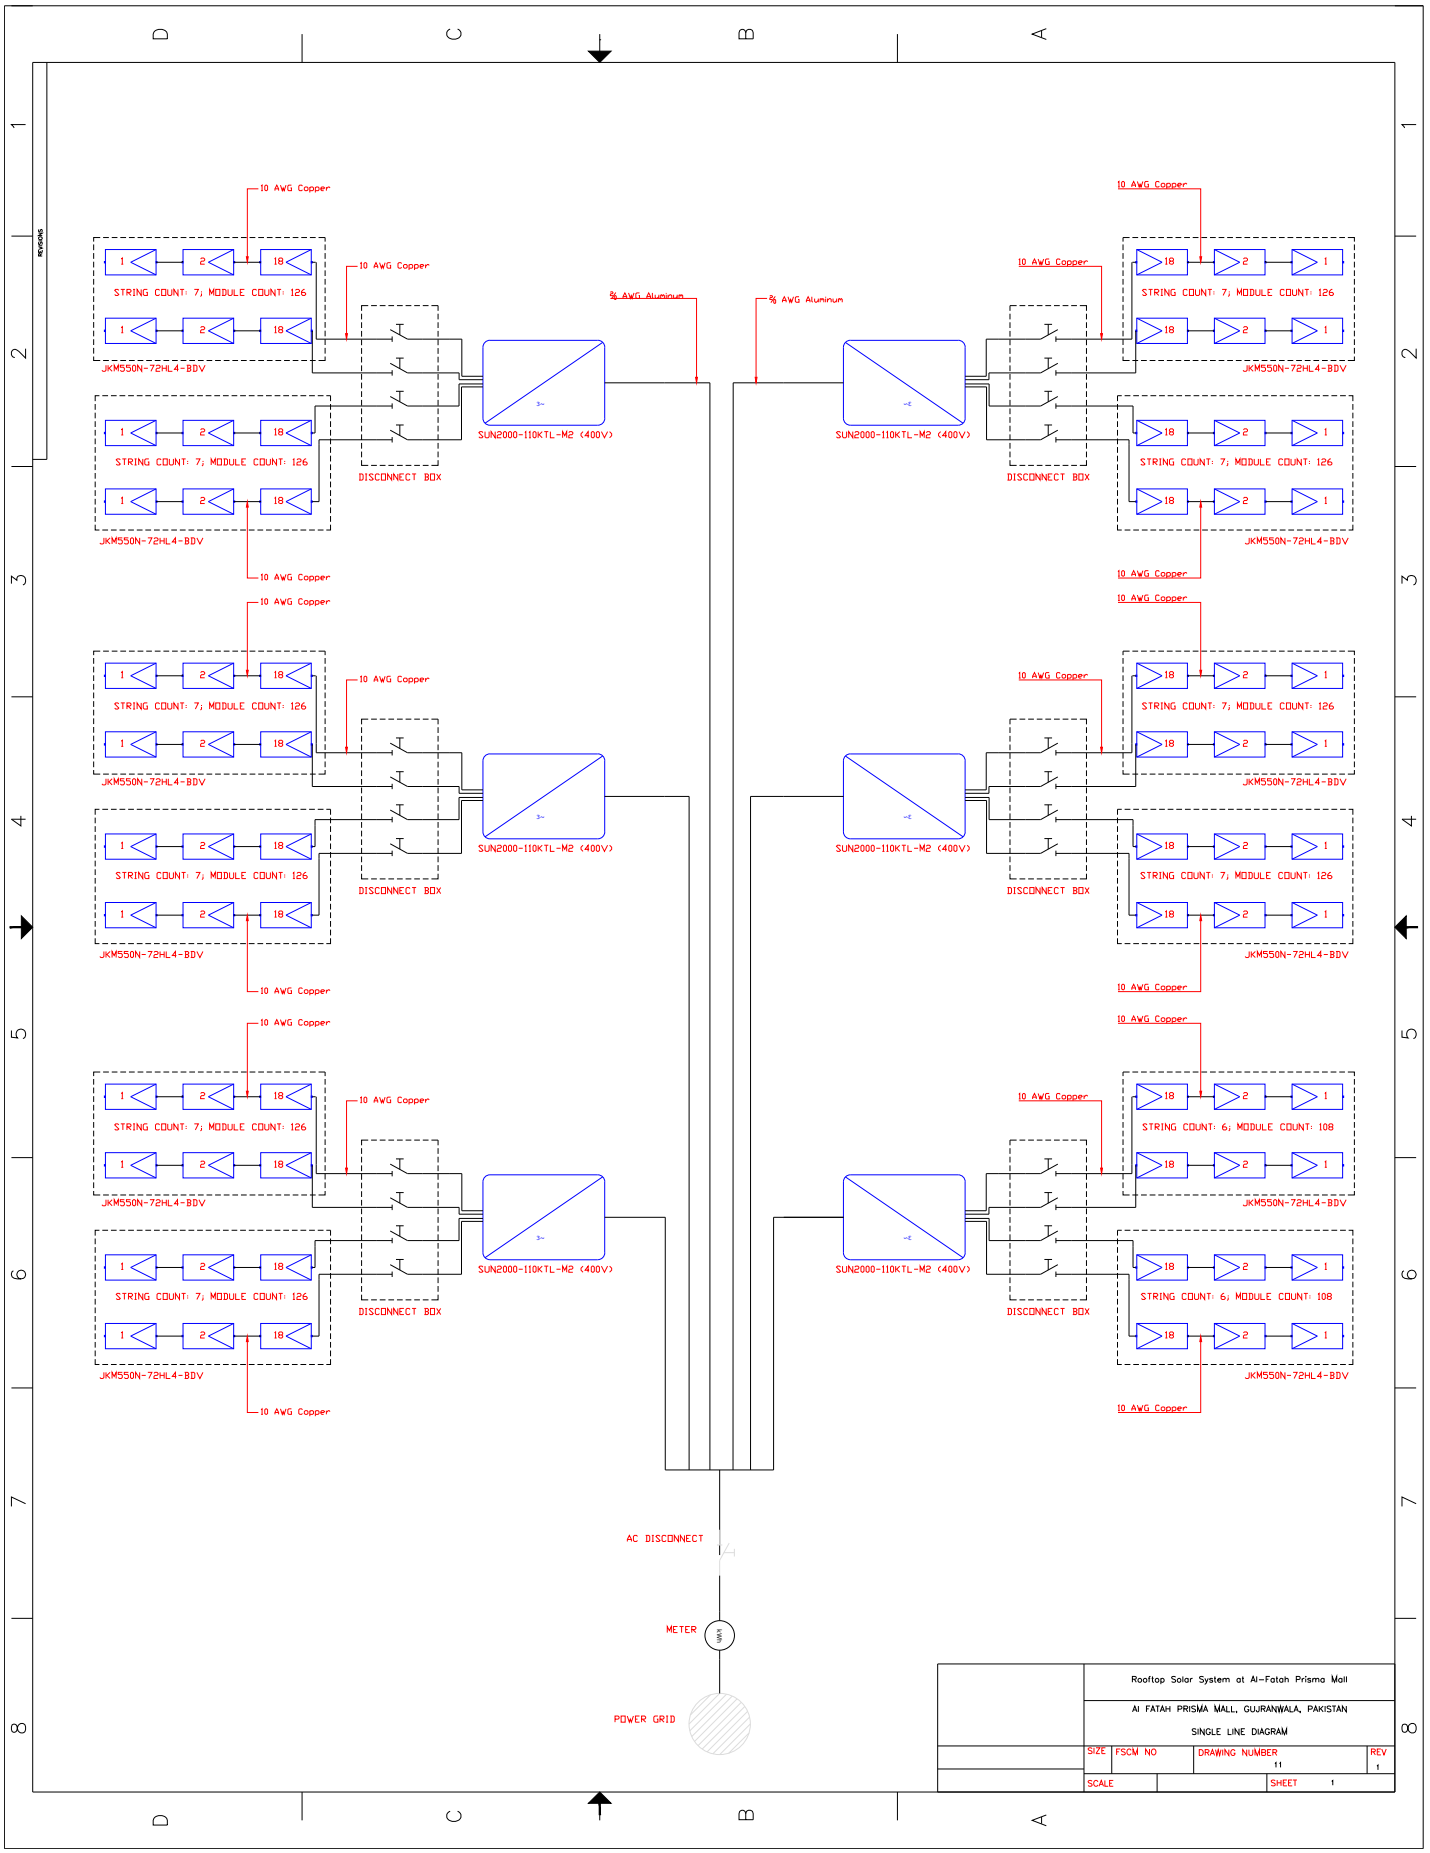


PV STRING DISTRIBUTION

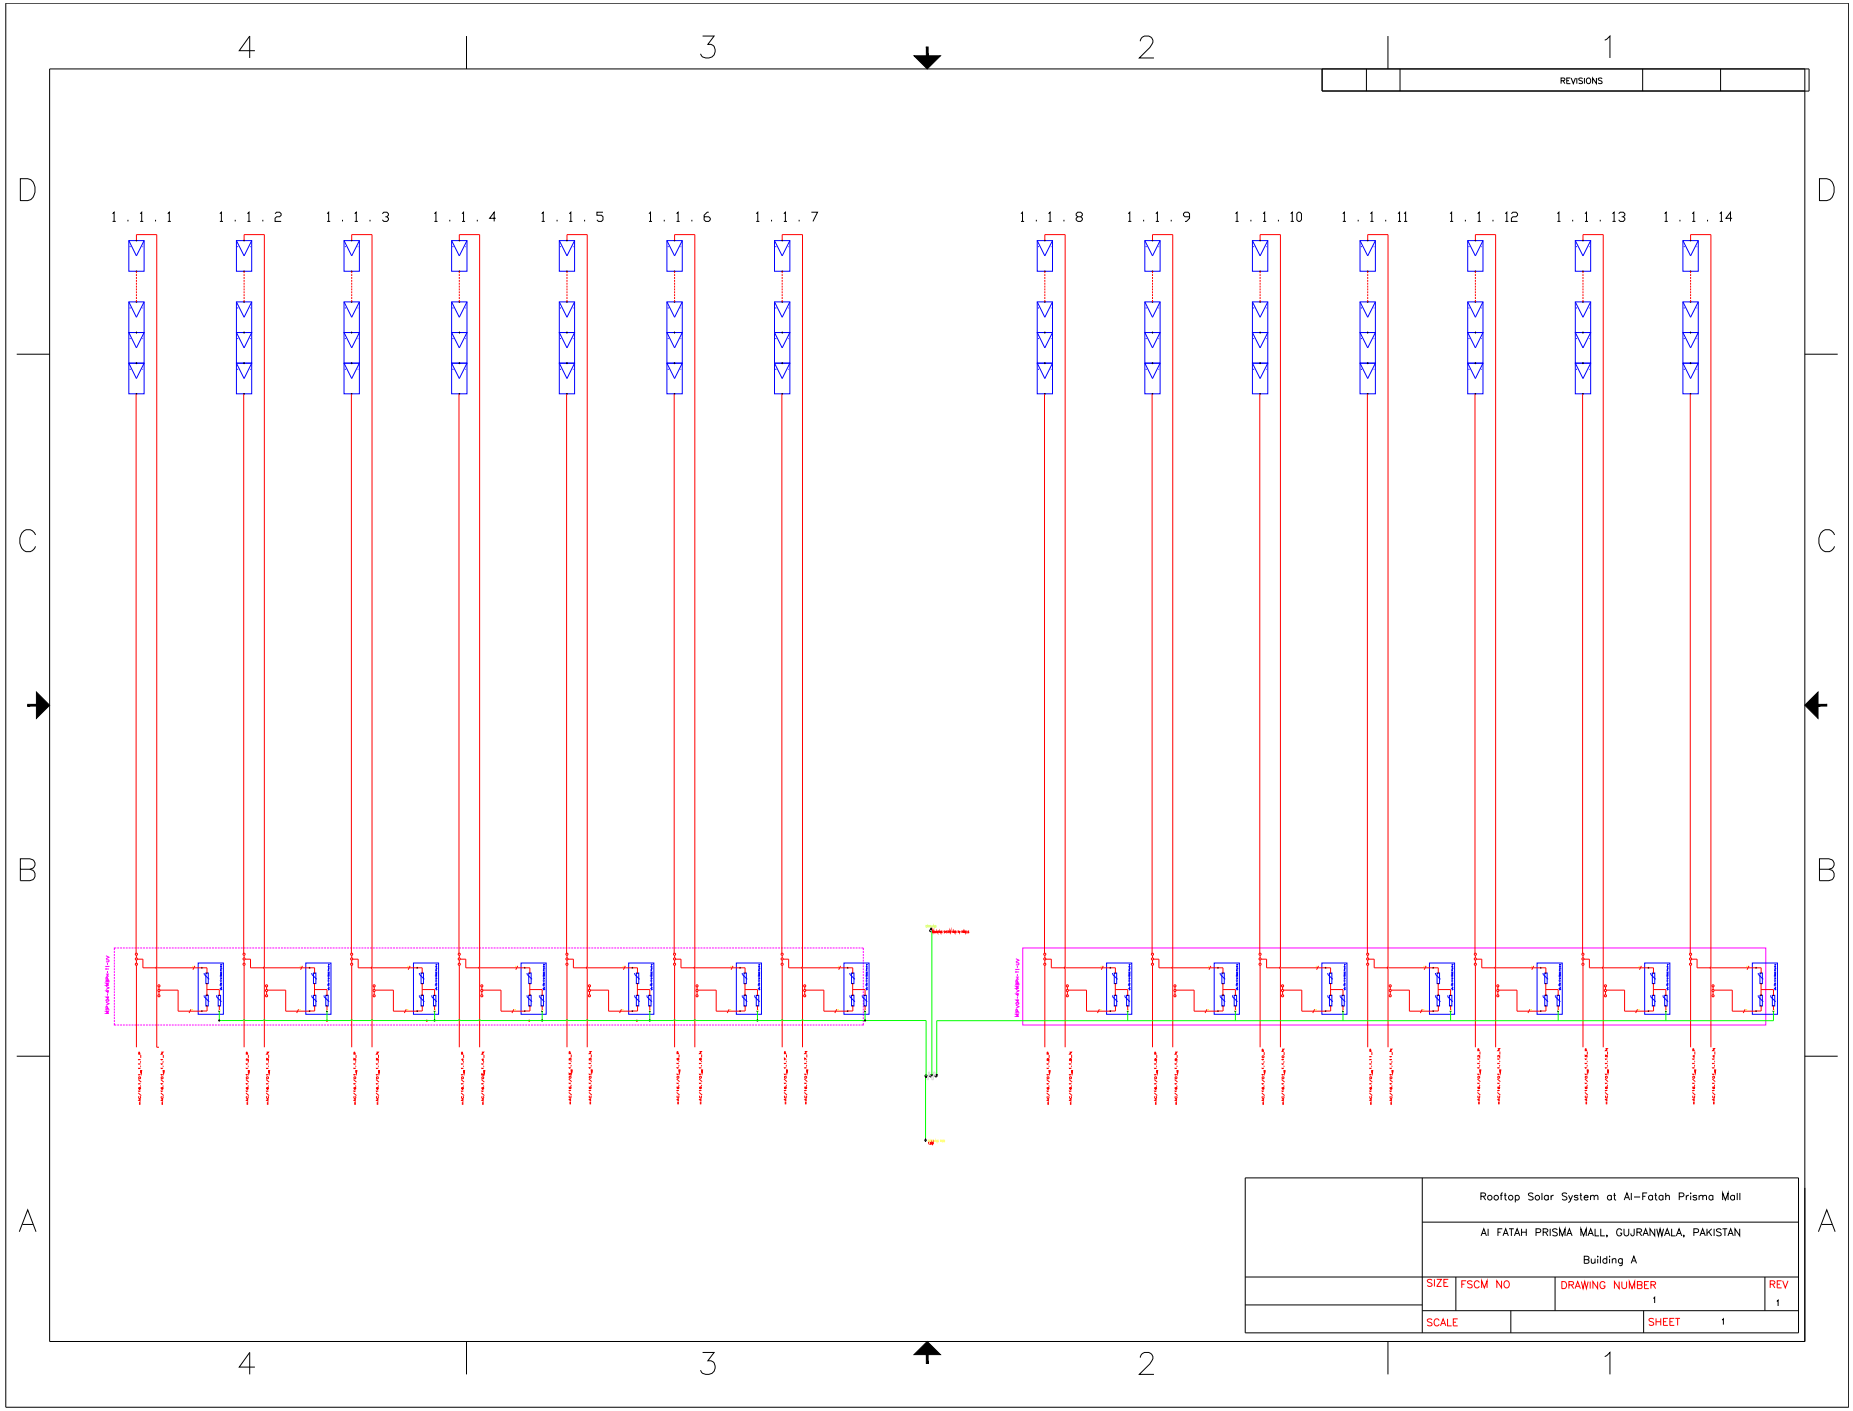


PV STRING DISTRIBUTION

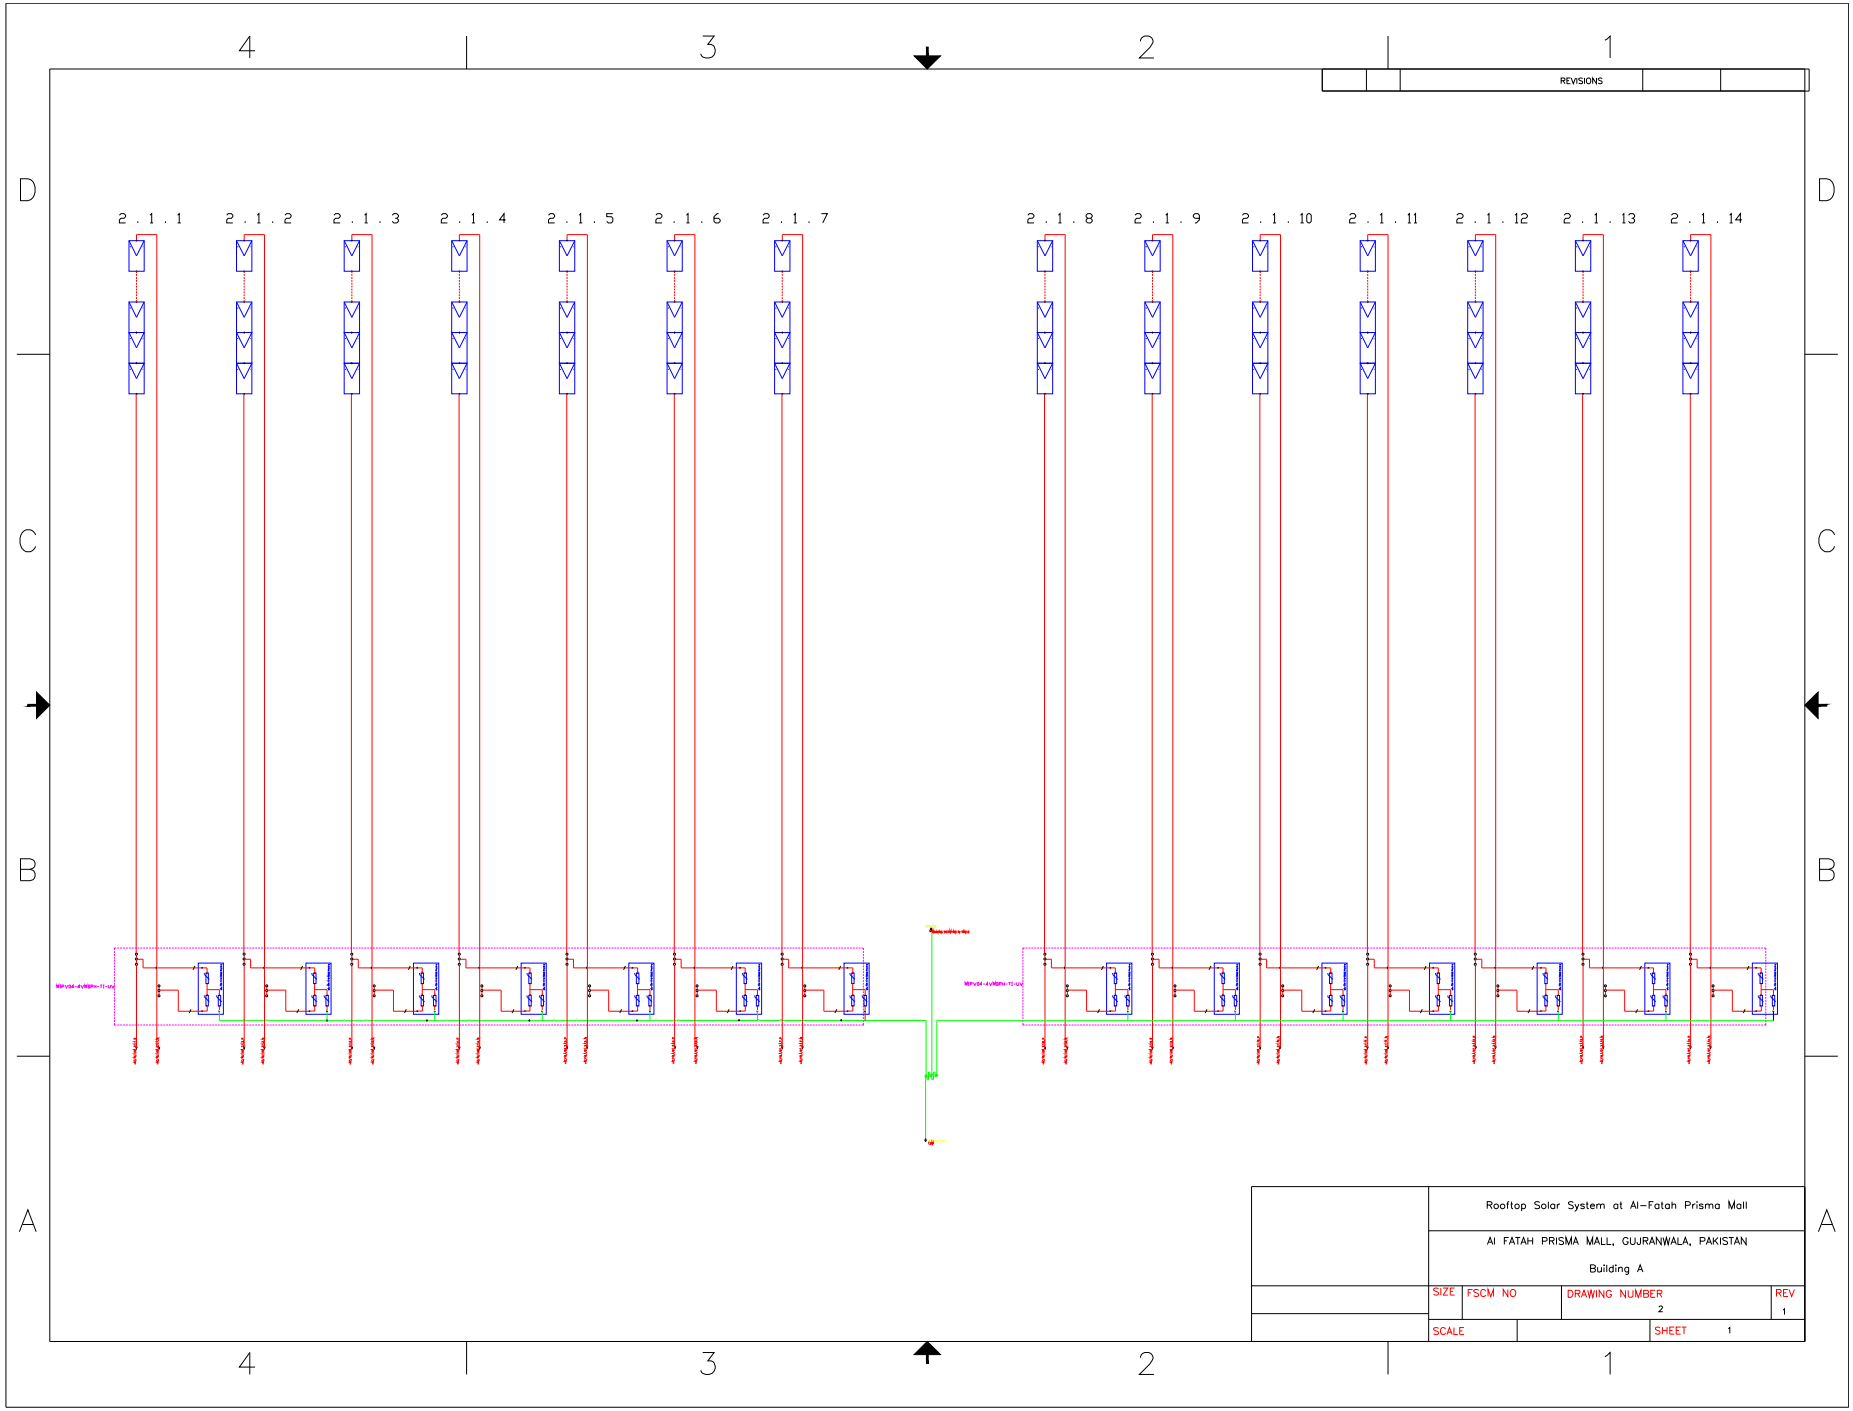


PV STRING DISTRIBUTION

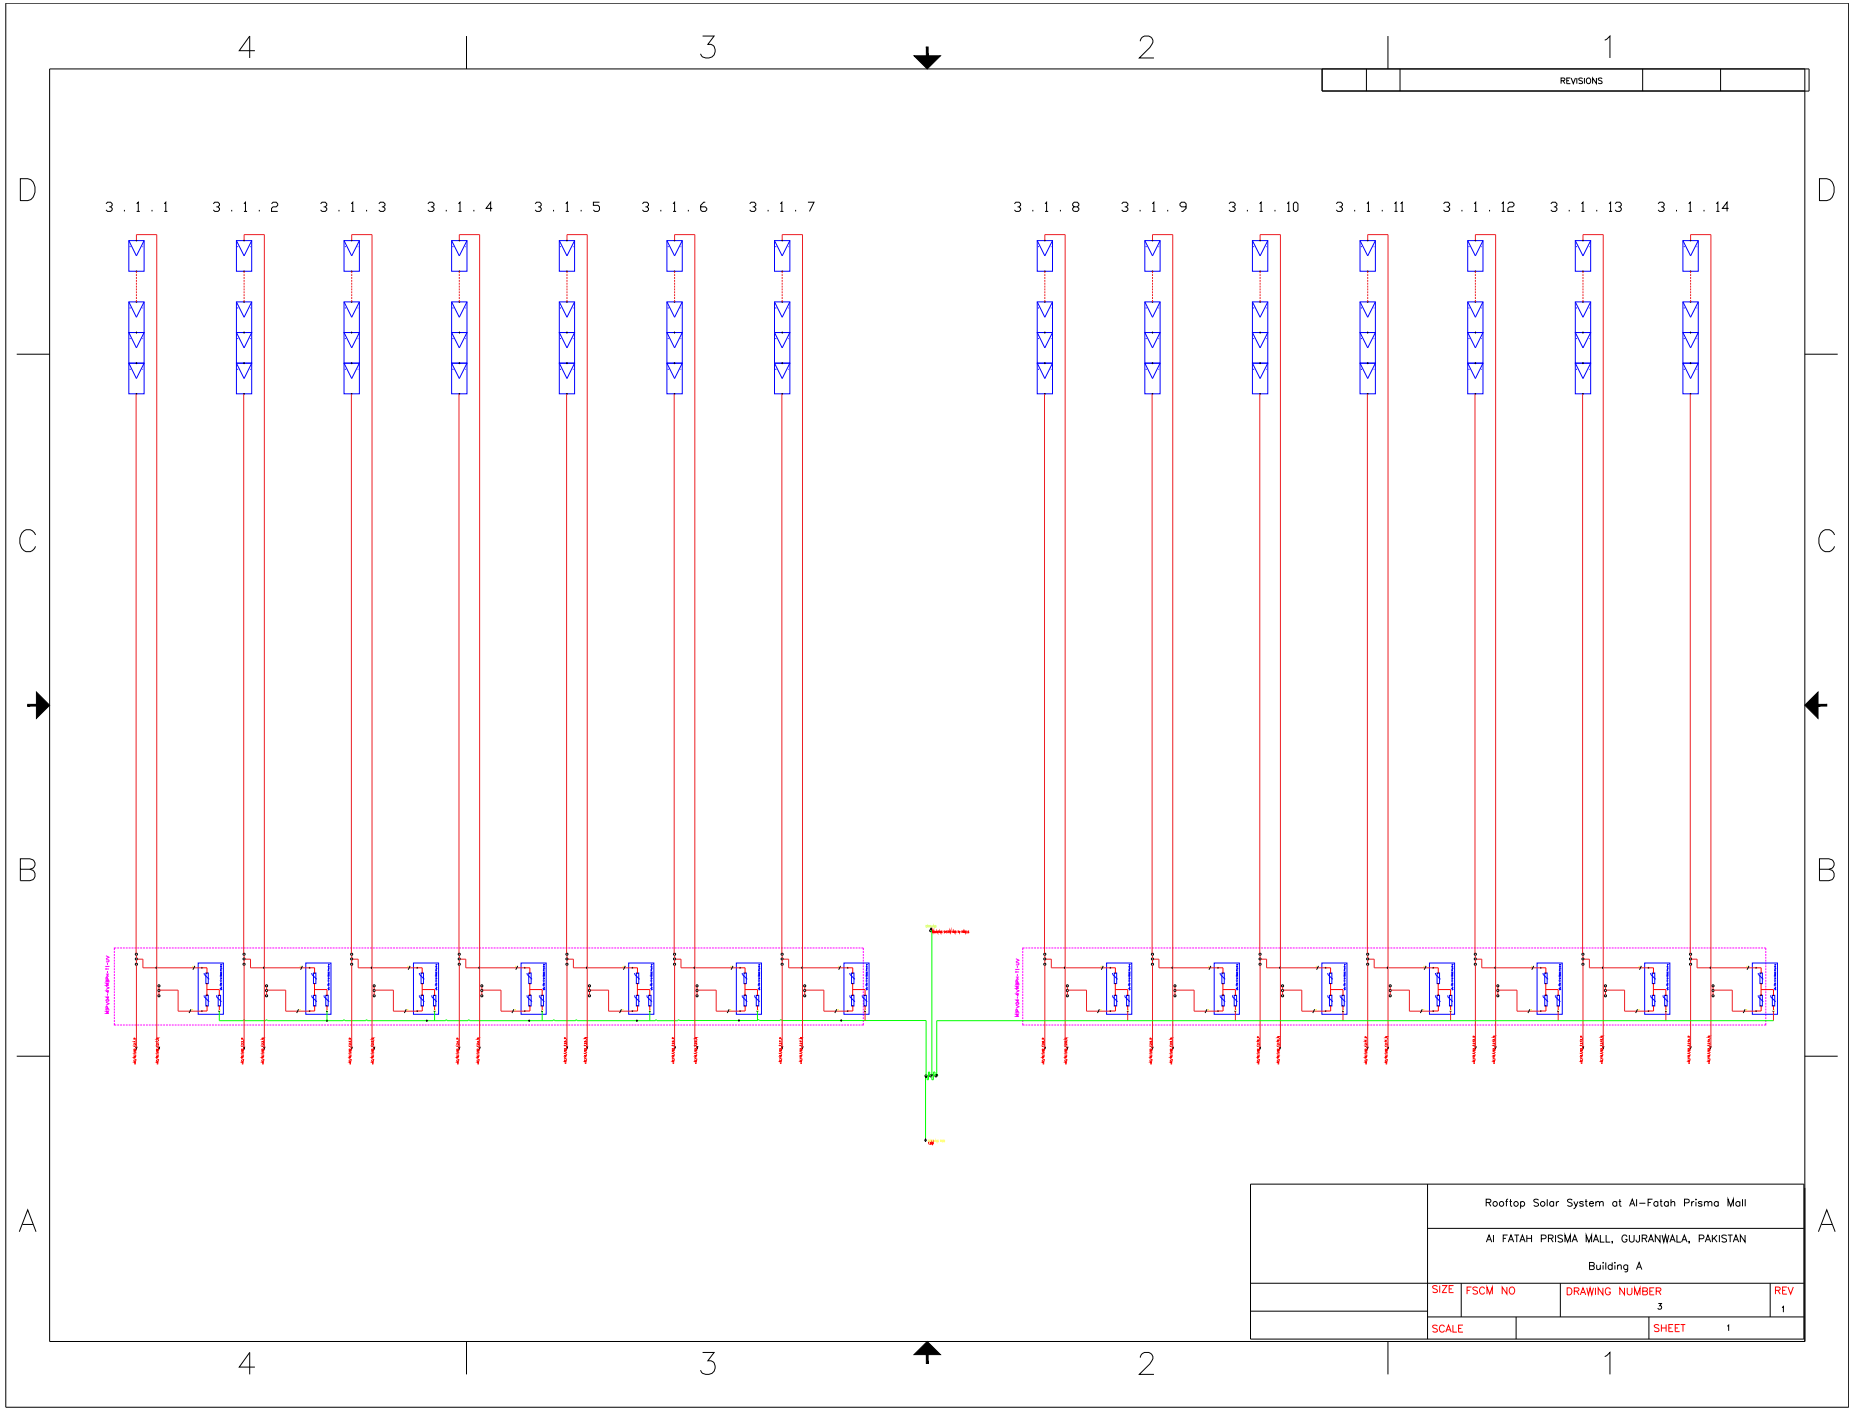


PV STRING DISTRIBUTION

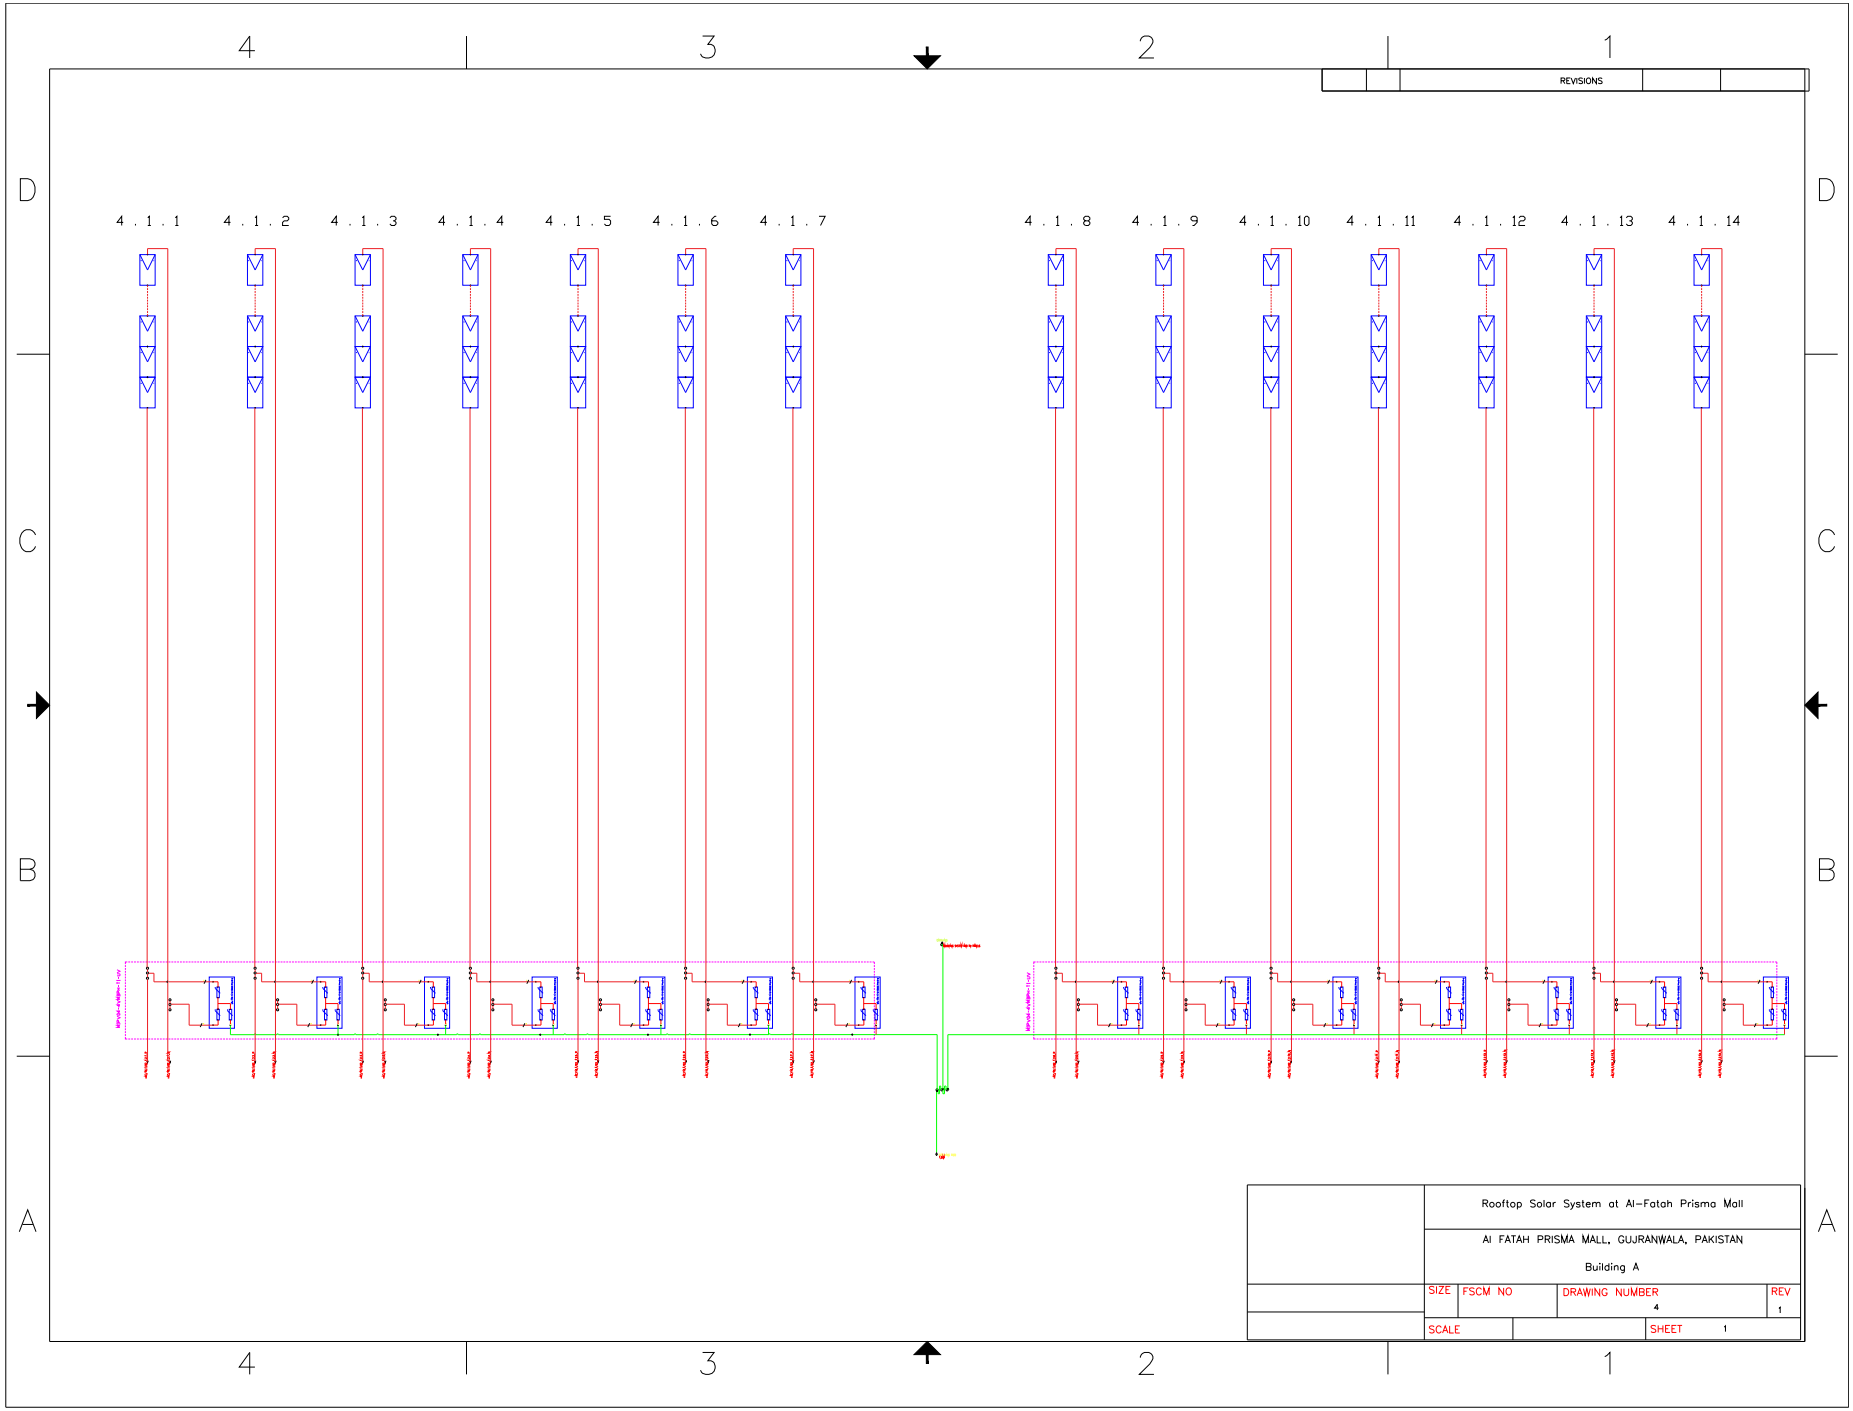


PV STRING DISTRIBUTION

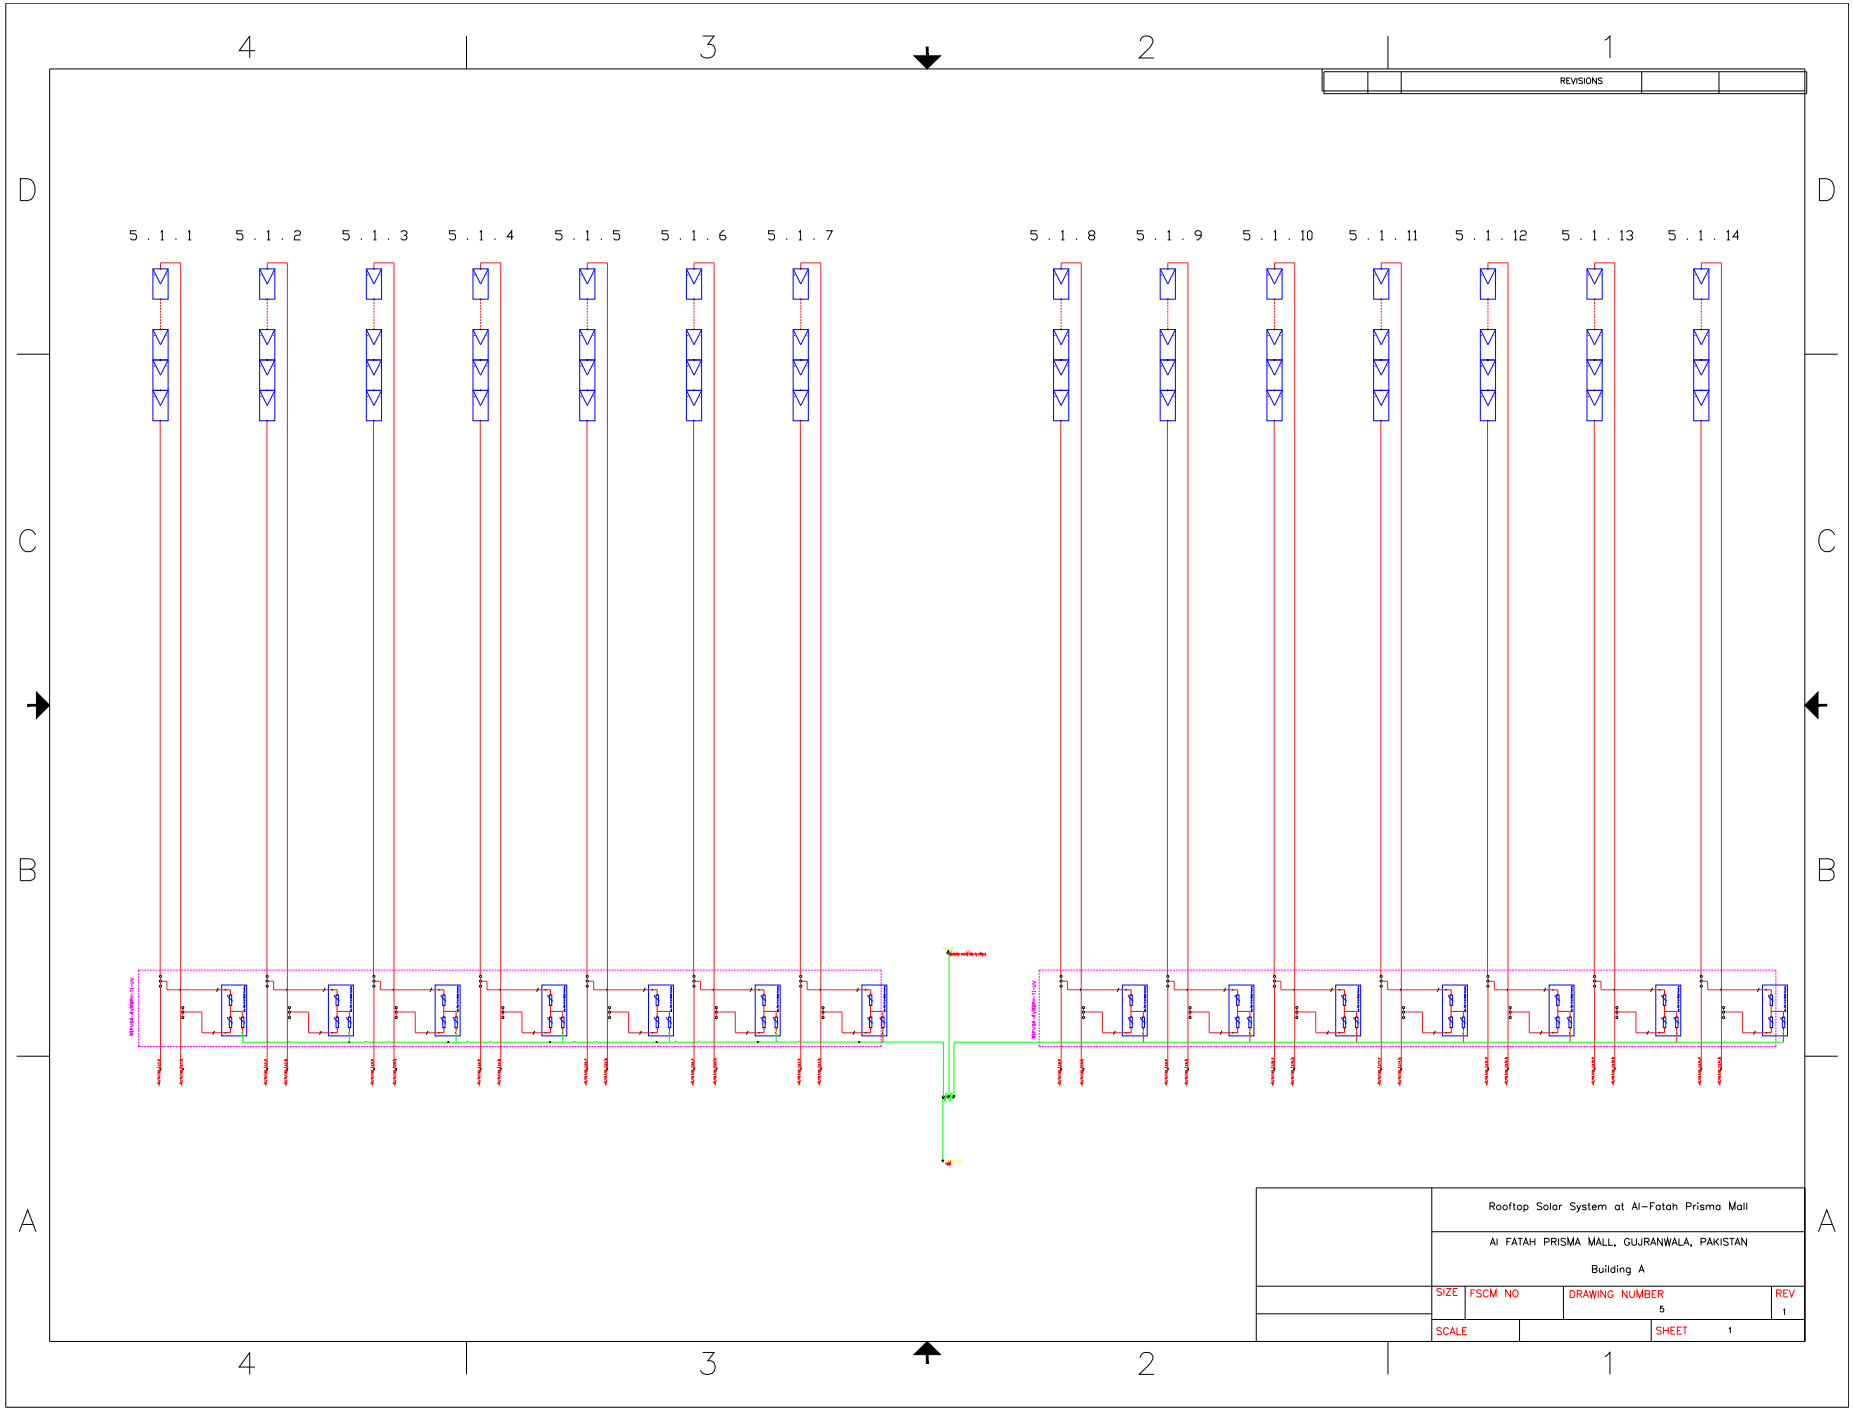


PV STRING DISTRIBUTION

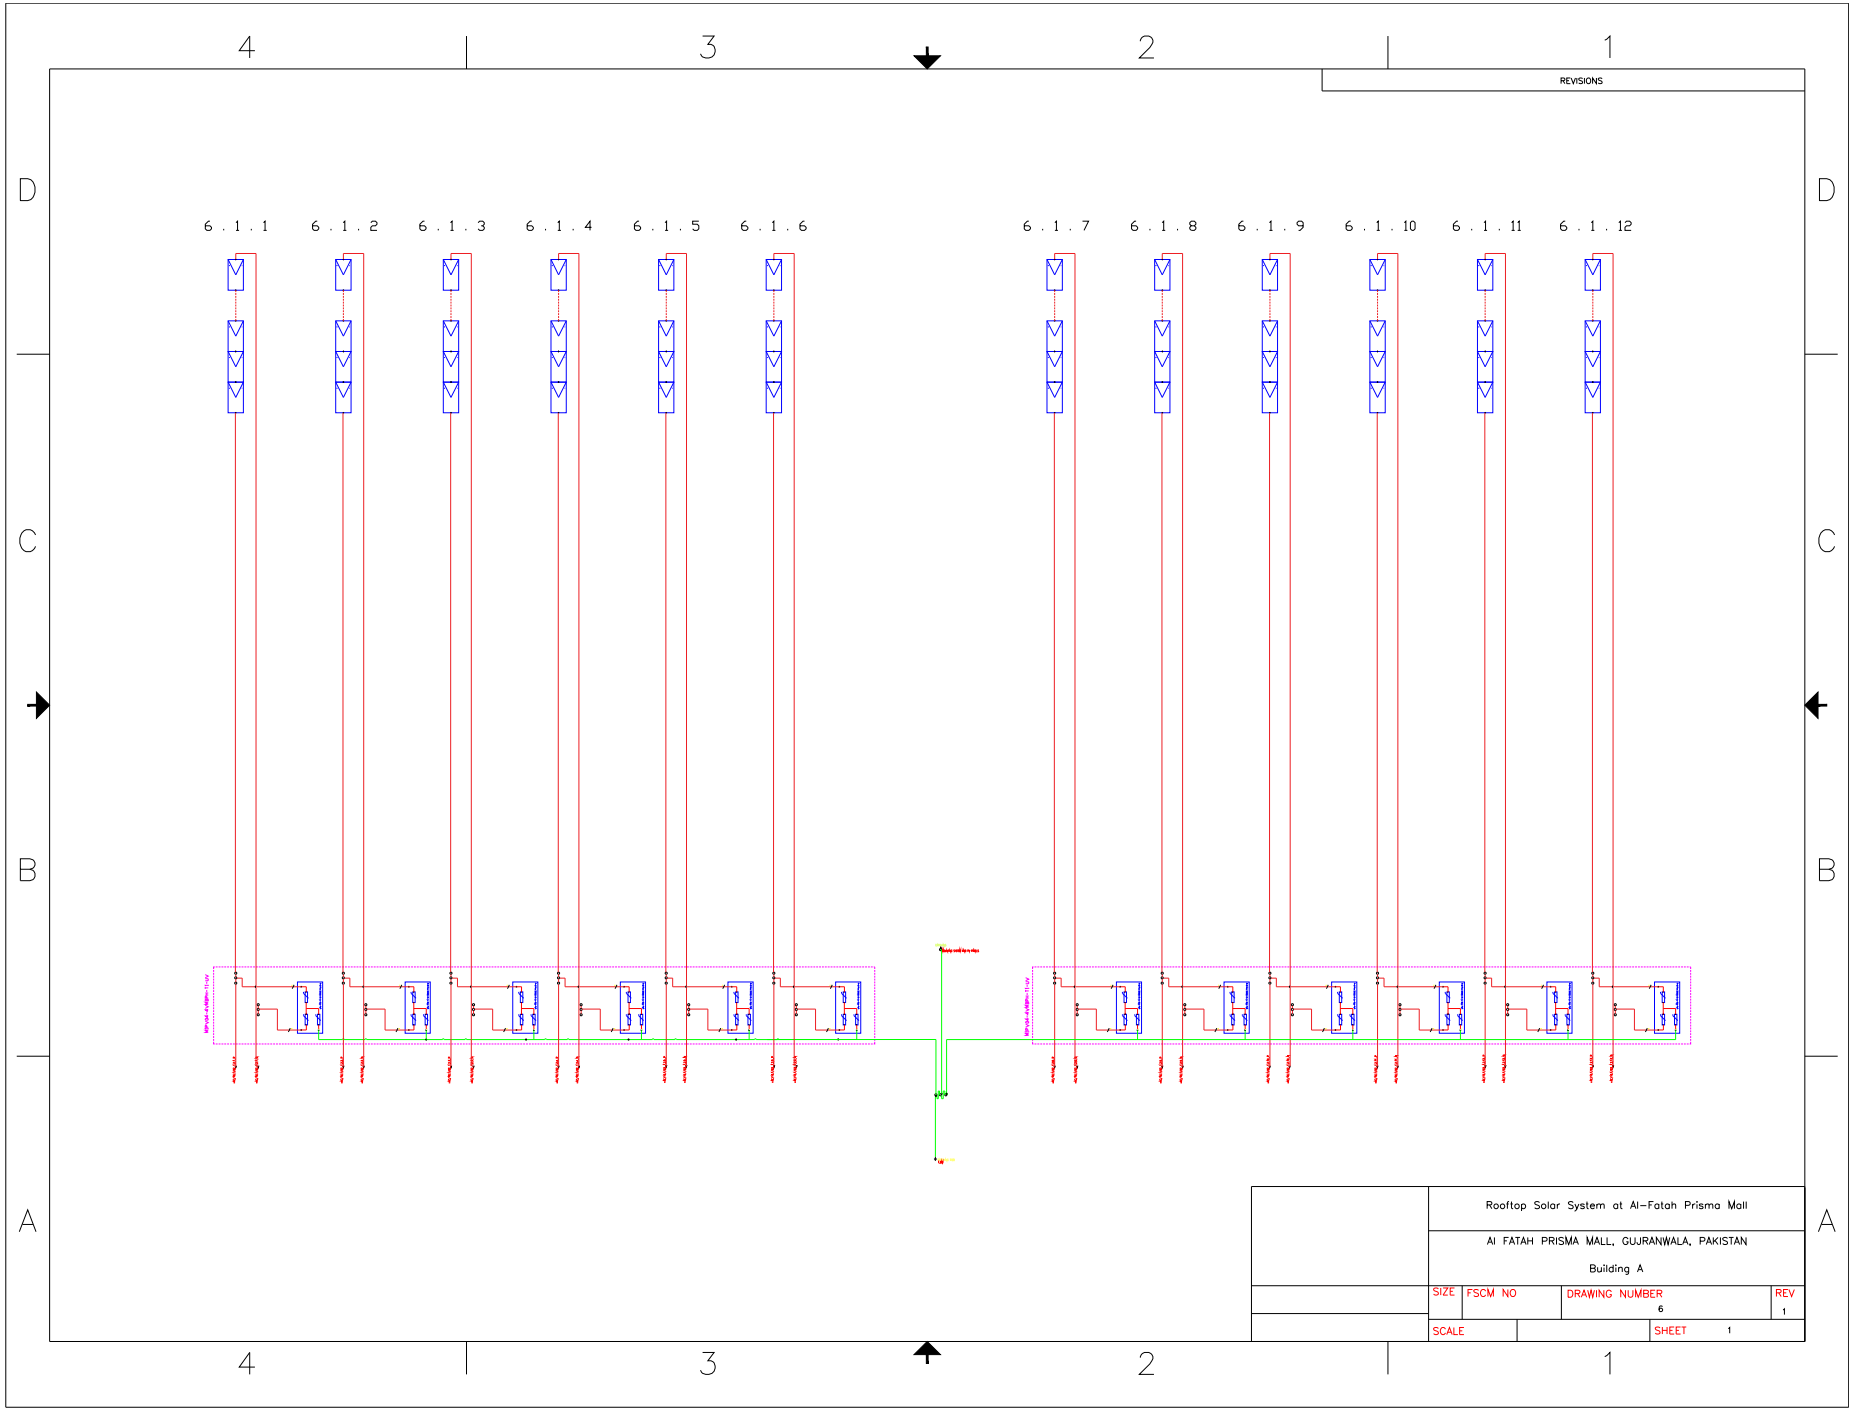


AC LAYOUT

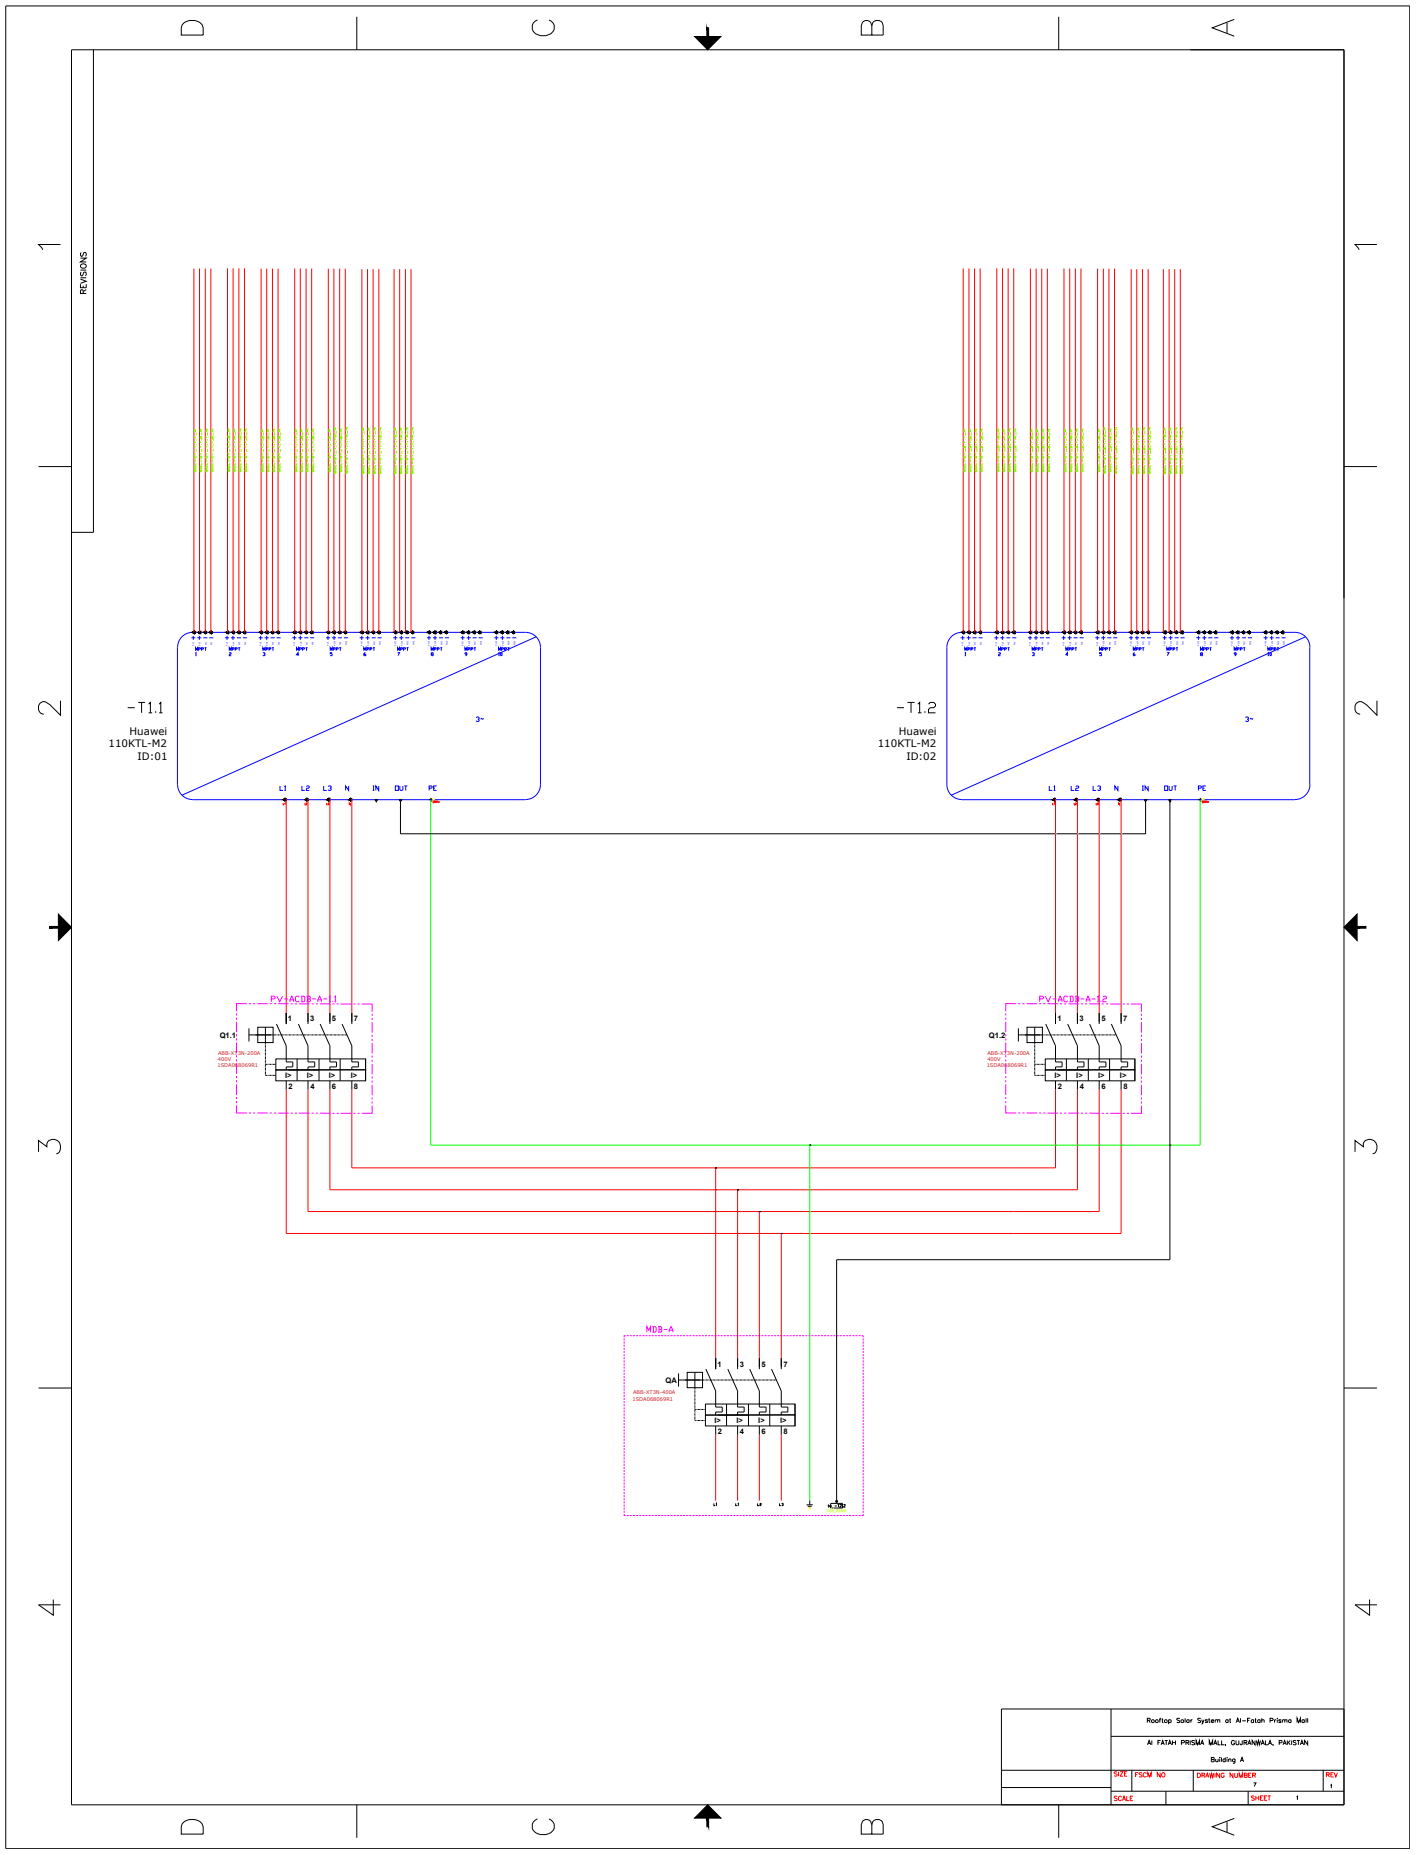
REVISIONS
-T1.1
Huawei
110KTL-M2
ID:01
-T1.2
Huawei
110KTL-M2
ID:02
L1 L2 L3 N IN OUT PE
PV-ACDB-A-1
PV-ACDB-A-2
Q1.1
Q1.2
MDB-A
QA
Rooftop Solar System at Al-Fateh Prisma Mall
AL FATAH PRISMA MALL, GUJRANWALA, PAKISTAN
Building A
SIZE
FSCM NO
DRAWING NUMBER
REV
SCALE
SHEET

AC LAYOUT

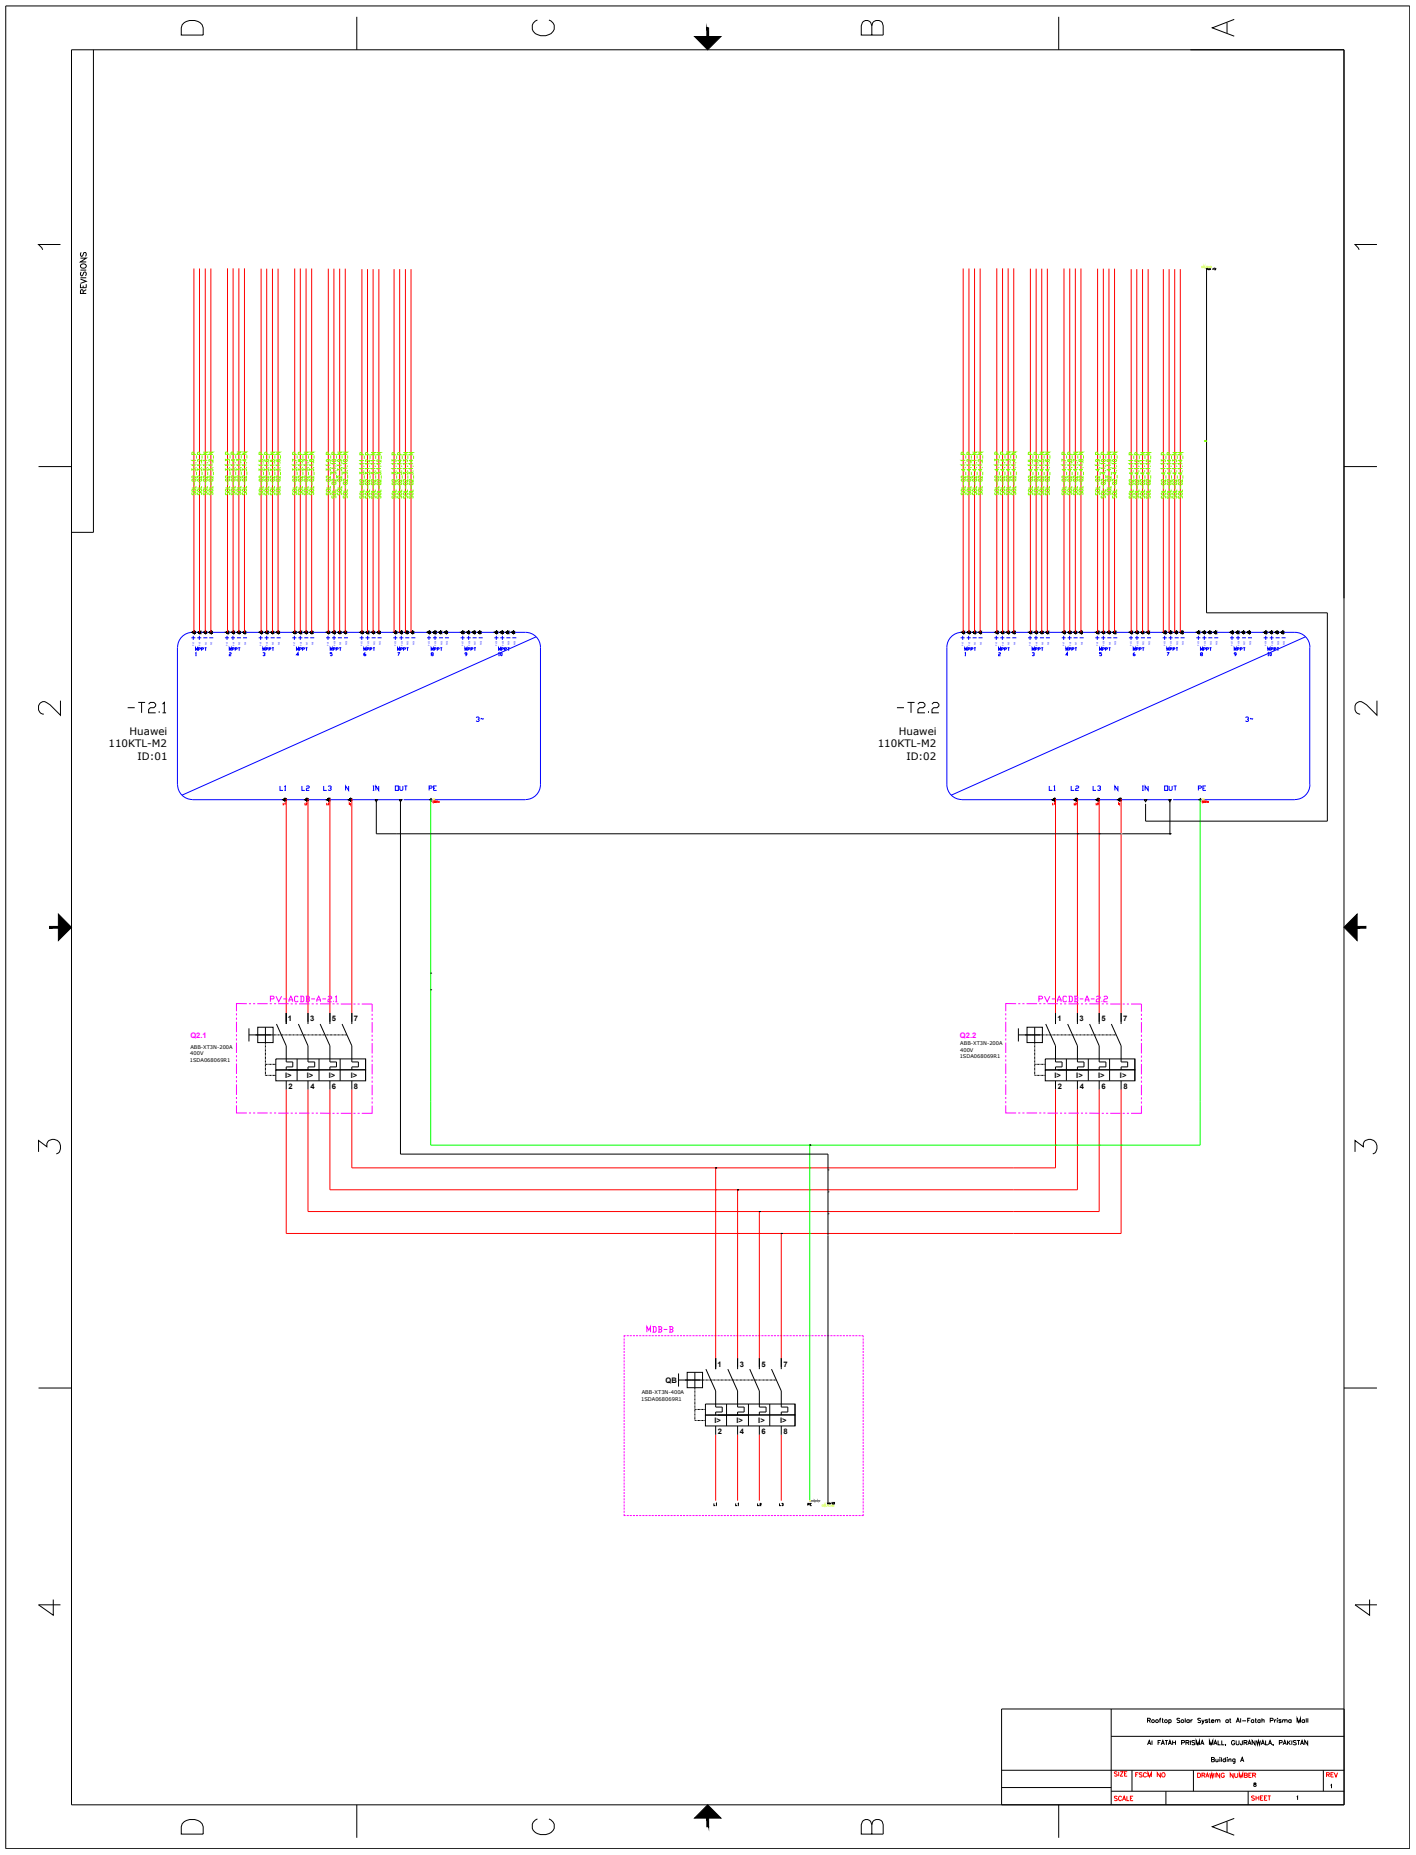
REVISIONS
-T2.1
Huawei
110KTL-M2
ID:01
-T2.2
Huawei
110KTL-M2
ID:02
L1 L2 L3 N IN OUT PE
PV-ACDB-A-2.1
PV-ACDB-A-2.2
Q2.1
Q2.2
MDB-B
QB
Rooftop Solar System at Al-Fatah Prisma Mall
AL FATAH PRISMA MALL, GUJRANWALA, PAKISTAN
Building A
SIZE
FSCM NO
DRAWING NUMBER
REV
SCALE
SHEET

AC LAYOUT

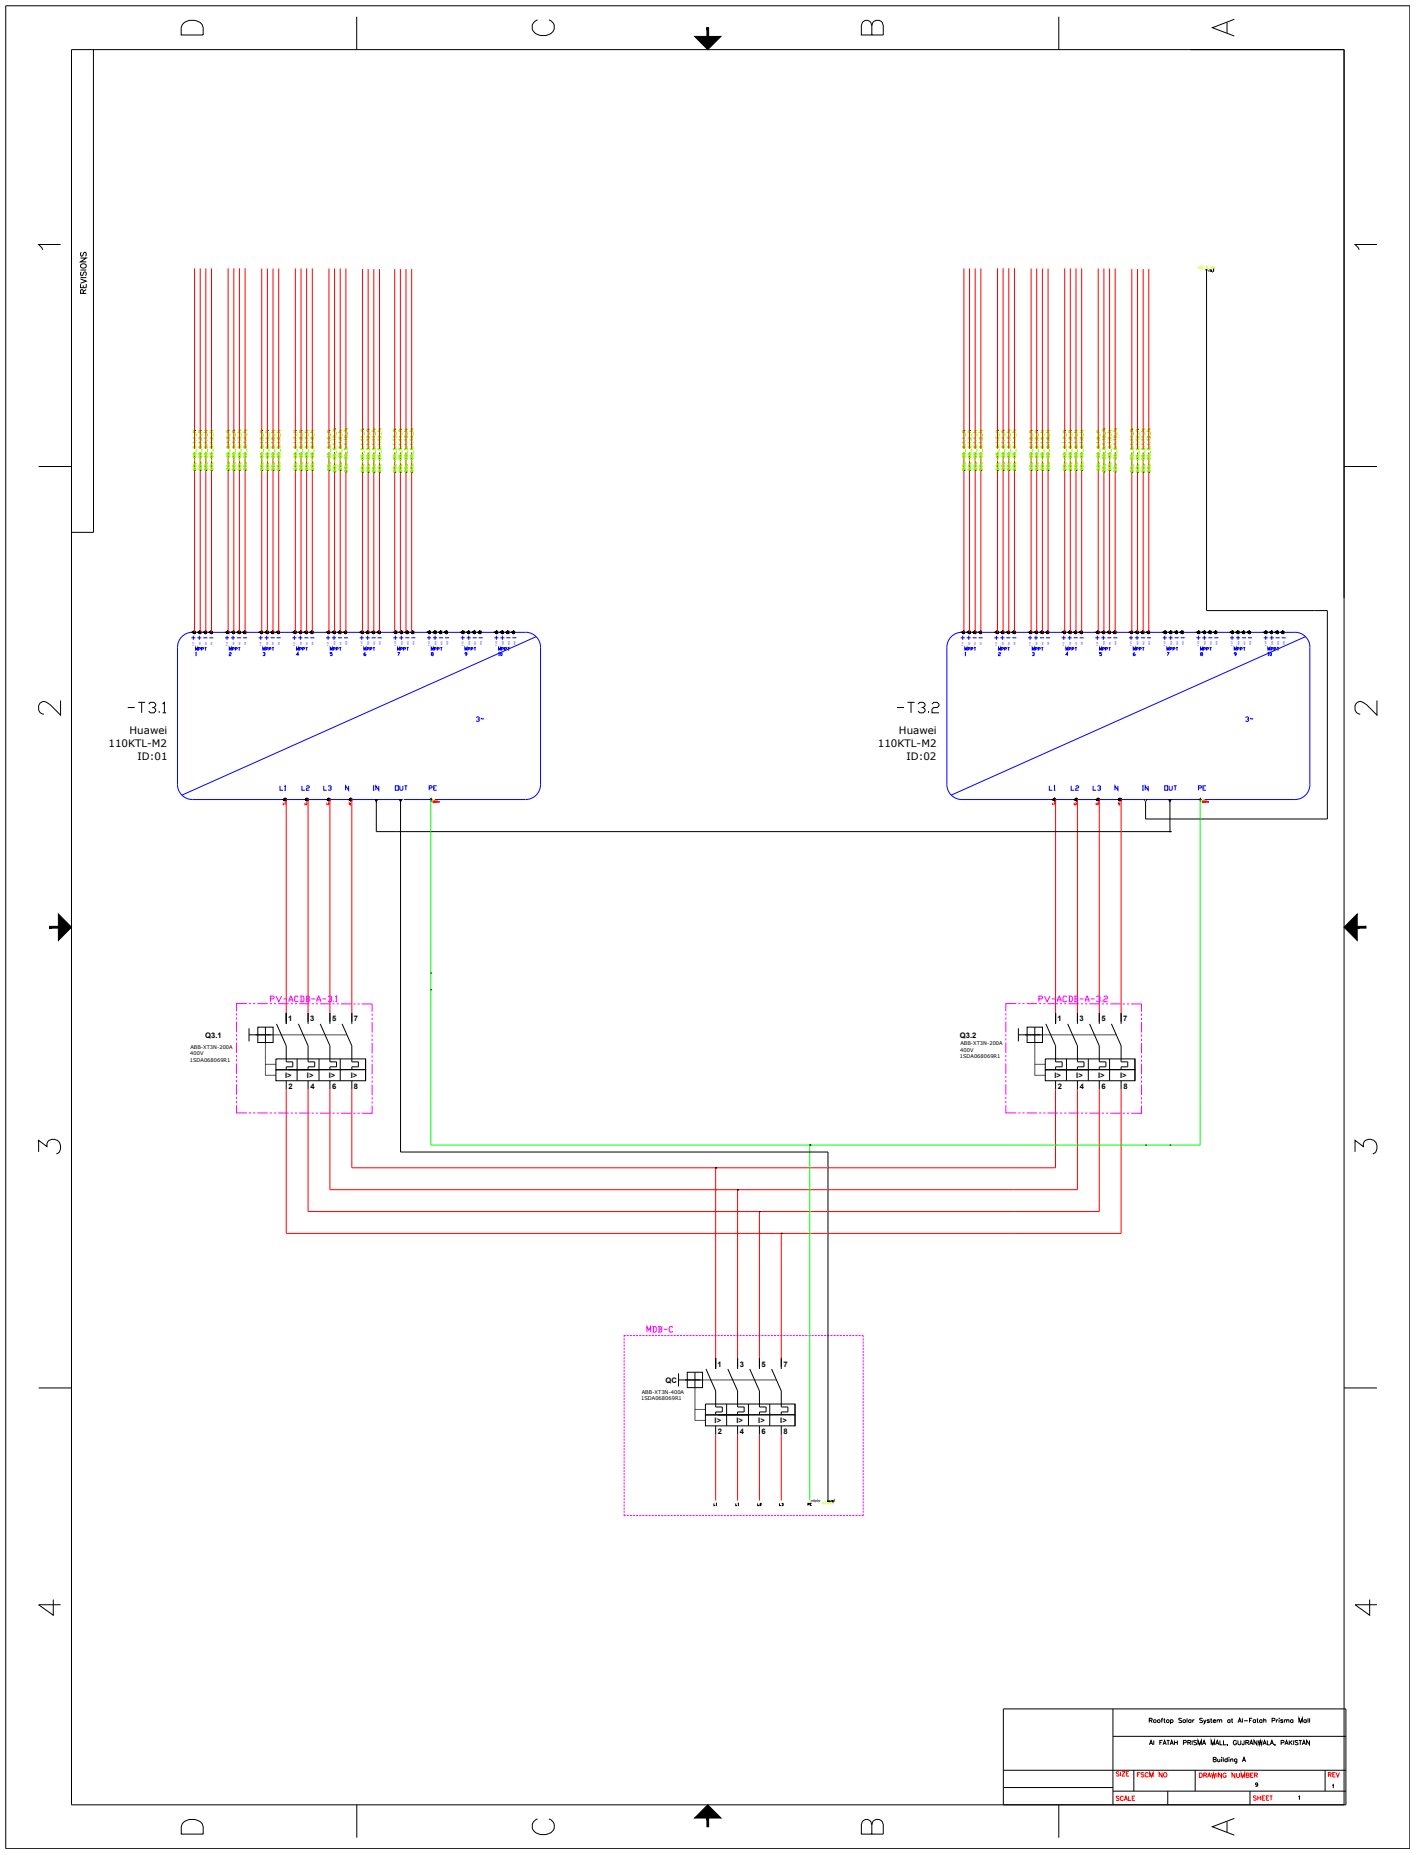
REVISIONS
-T3.1
Huawei
110KTL-M2
ID:01
-T3.2
Huawei
110KTL-M2
ID:02
L1 L2 L3 N IN OUT PE
PV-ACDB-A-2.1
Q3.1
PV-ACDB-A-2.2
Q3.2
MDB-C
QC
Rooftop Solar System at Al-Fatah Prisma Mall
AL FATAH PRISMA MALL, GUJRANWALA, PAKISTAN
Building A
SIZE
FSCM NO
DRAWING NUMBER
REV
SCALE
SHEET

AC DISTRIBUTION AND GRID CONNECTION

