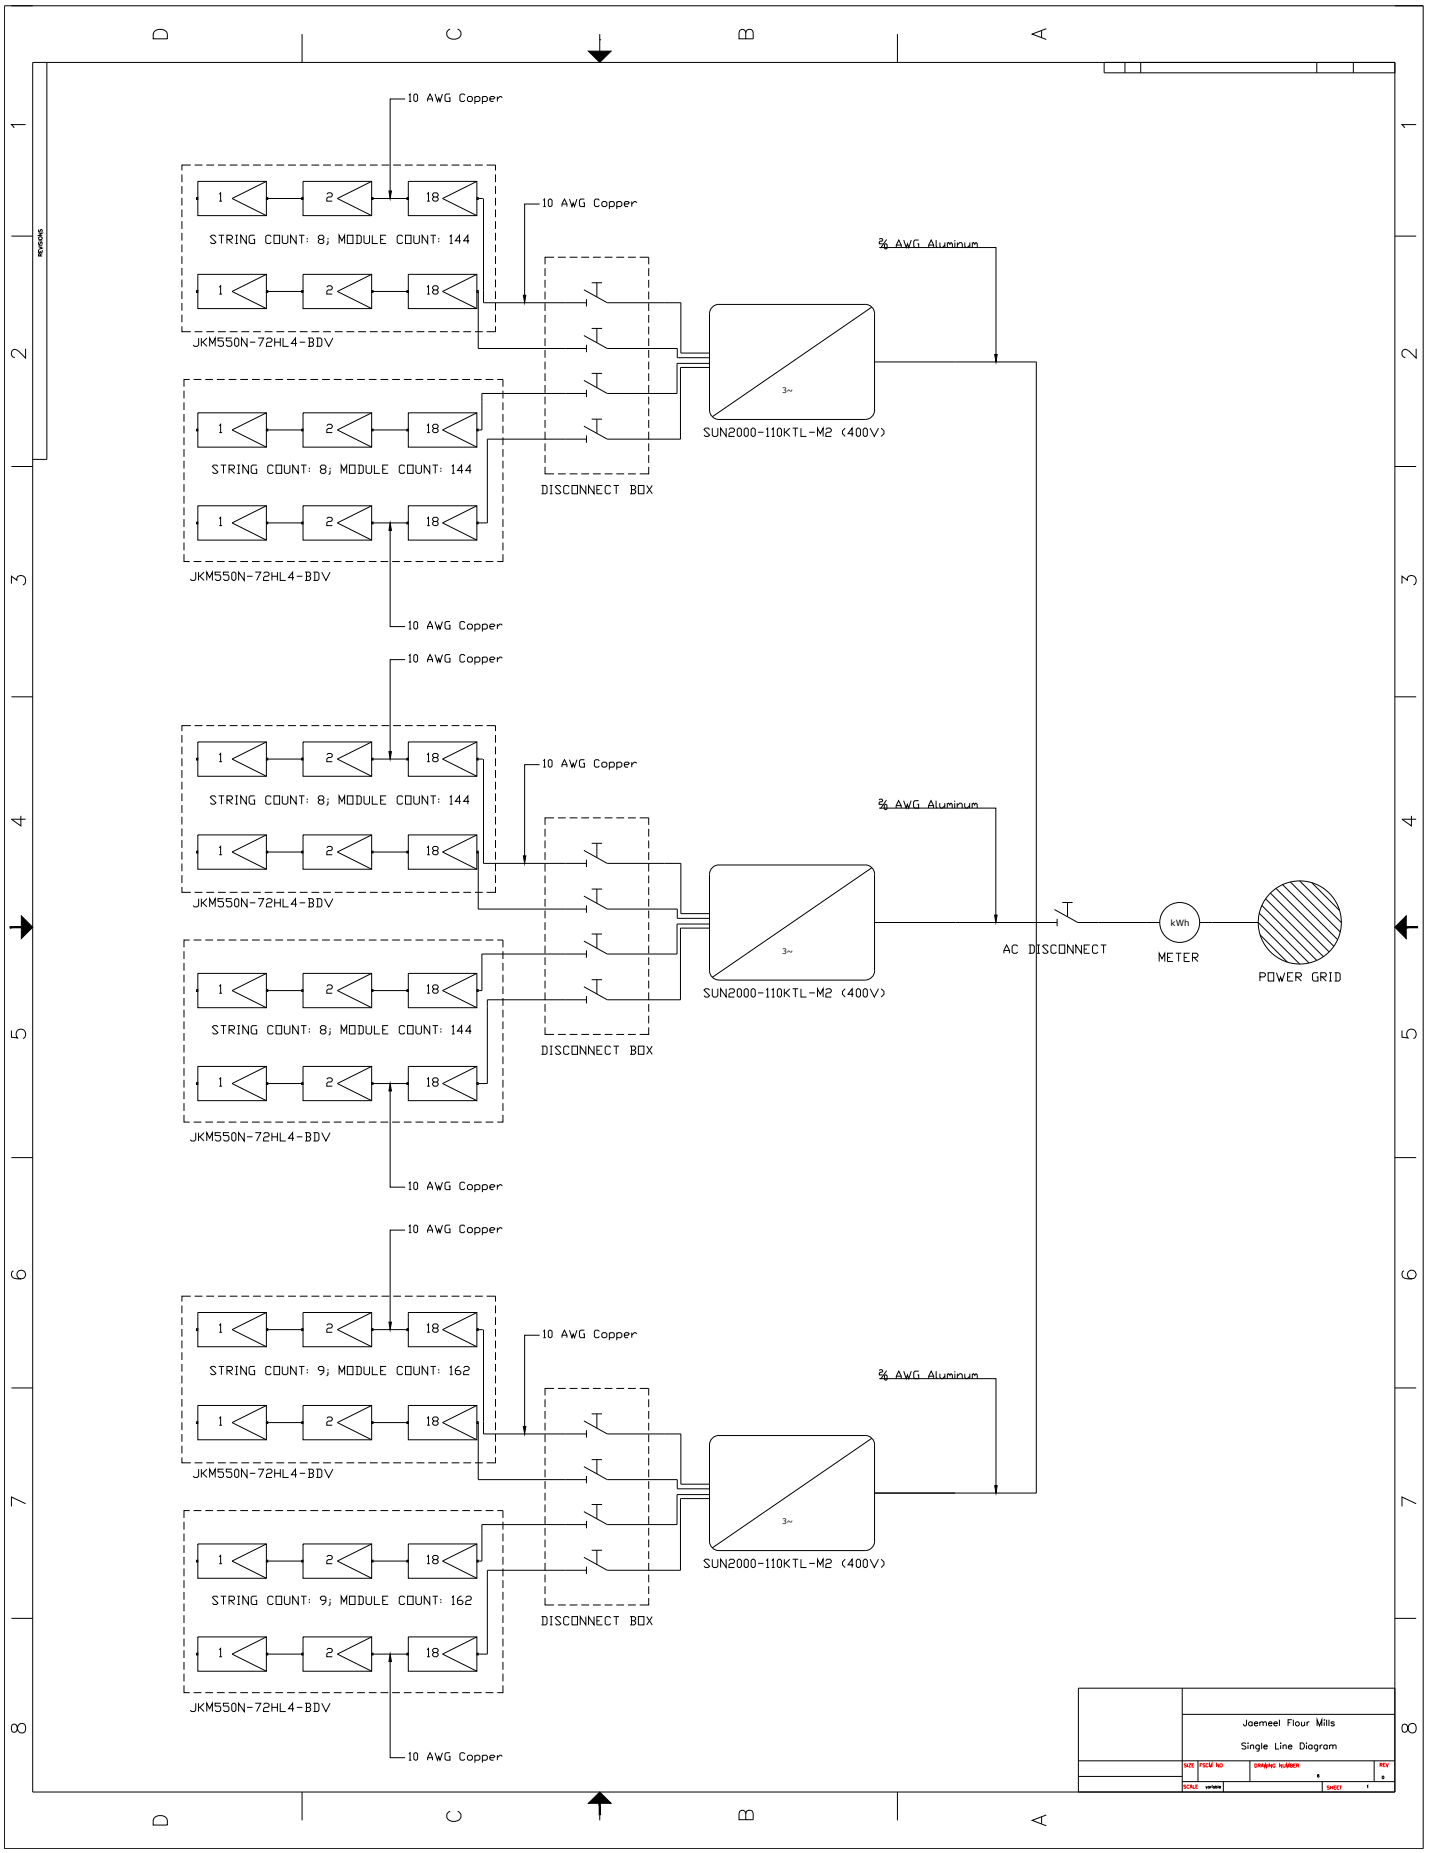

10 AWG Copper
STRING COUNT: 8; MODULE COUNT: 144
JKM550N-72HL4-BDV
DISCONNECT BOX
SUN2000-110KTL-M2 (400V)
8 AWG Aluminum
AC DISCONNECT
METER
POWER GRID
STRING COUNT: 9; MODULE COUNT: 162
Jaemeel Flour Mills
Single Line Diagram