SLD &TECHNICAL DRAWINGS

500 kWp Grid-Connected Ground Mounted Solar PV Installation

Asset Owner: Jameel Flour Mills Limited

Location: Bhakkar, Punjab, Pakistan


Primary Core Equipment: Huawei SUN2000-110KTL-M2 & Jinko 550W

Document Control Code: AN-PV-OMM-2026-REV1

Target Audience: Internal Operations & Maintenance Department


Date of Issue: August 2023

REVISIONS

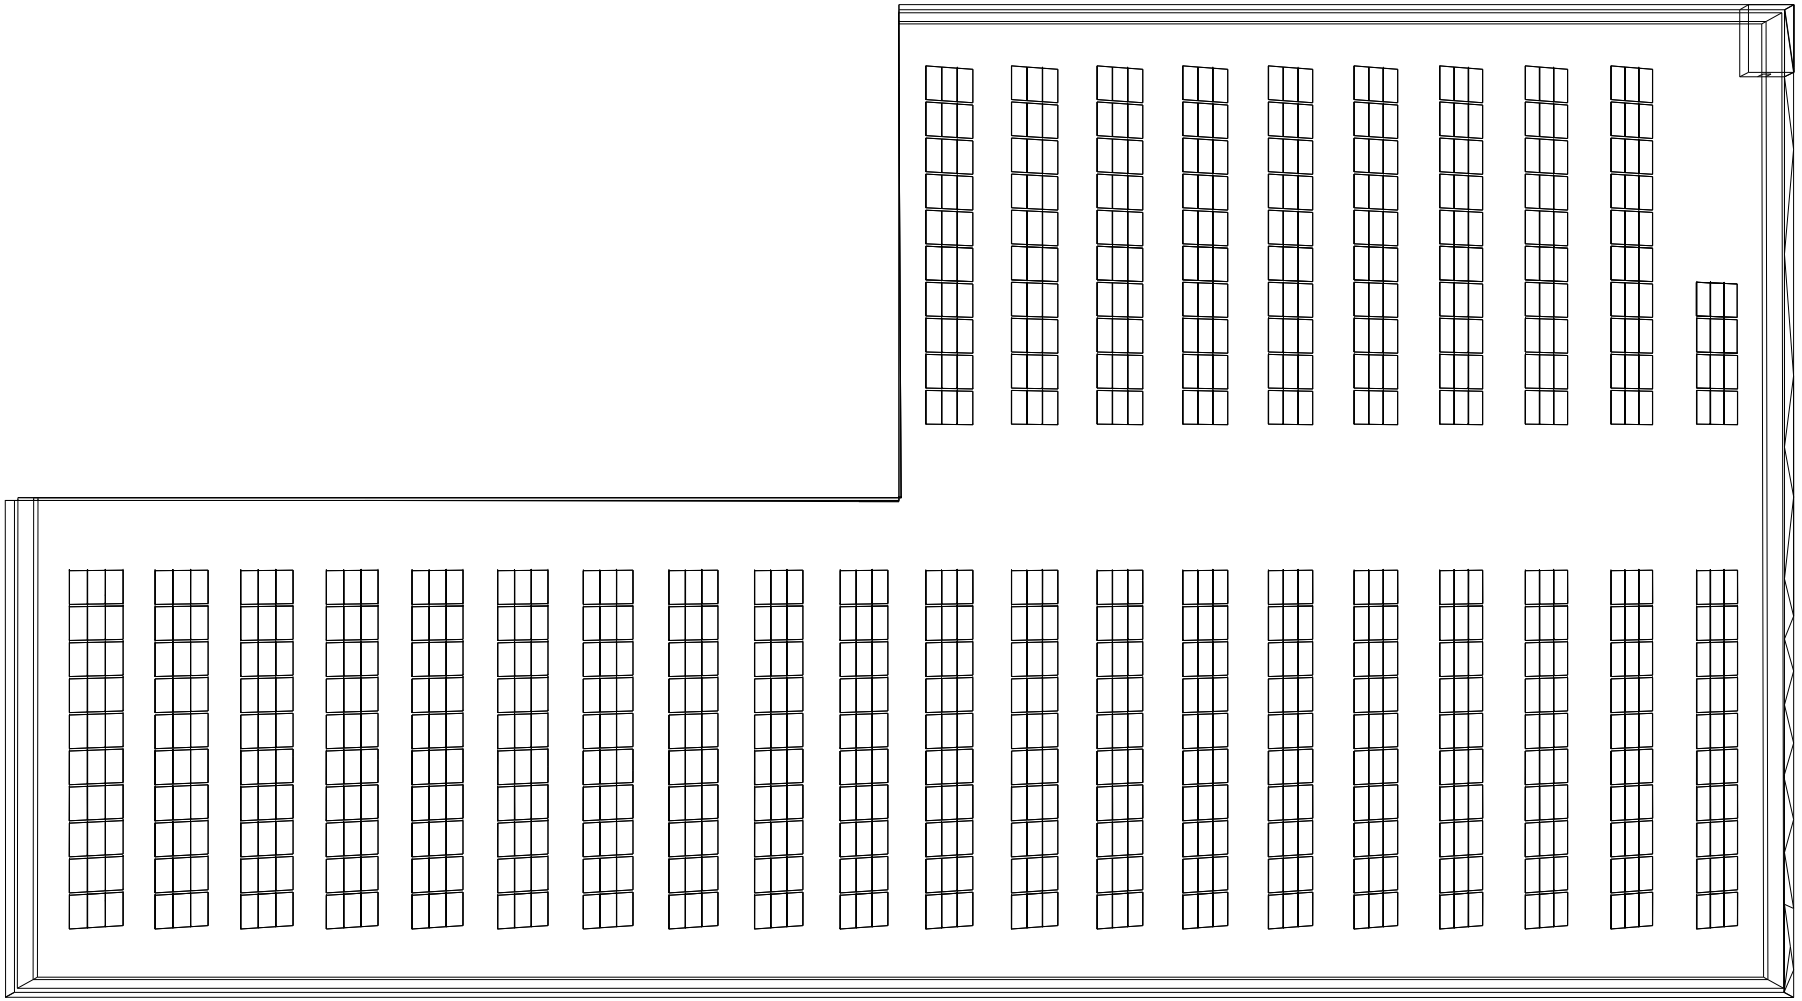


	Rooftop Solar System at Jameel Flour Mills
	JAMEEL FLOUR MILLS BHAKKAR, PUNJAB
	OVERVIEW
SIZE	FSCM NO / DRAWING NUMBER 1.1 / REV 1
SCALE	SHEET 1


SINGLE LINE DIAGRAM

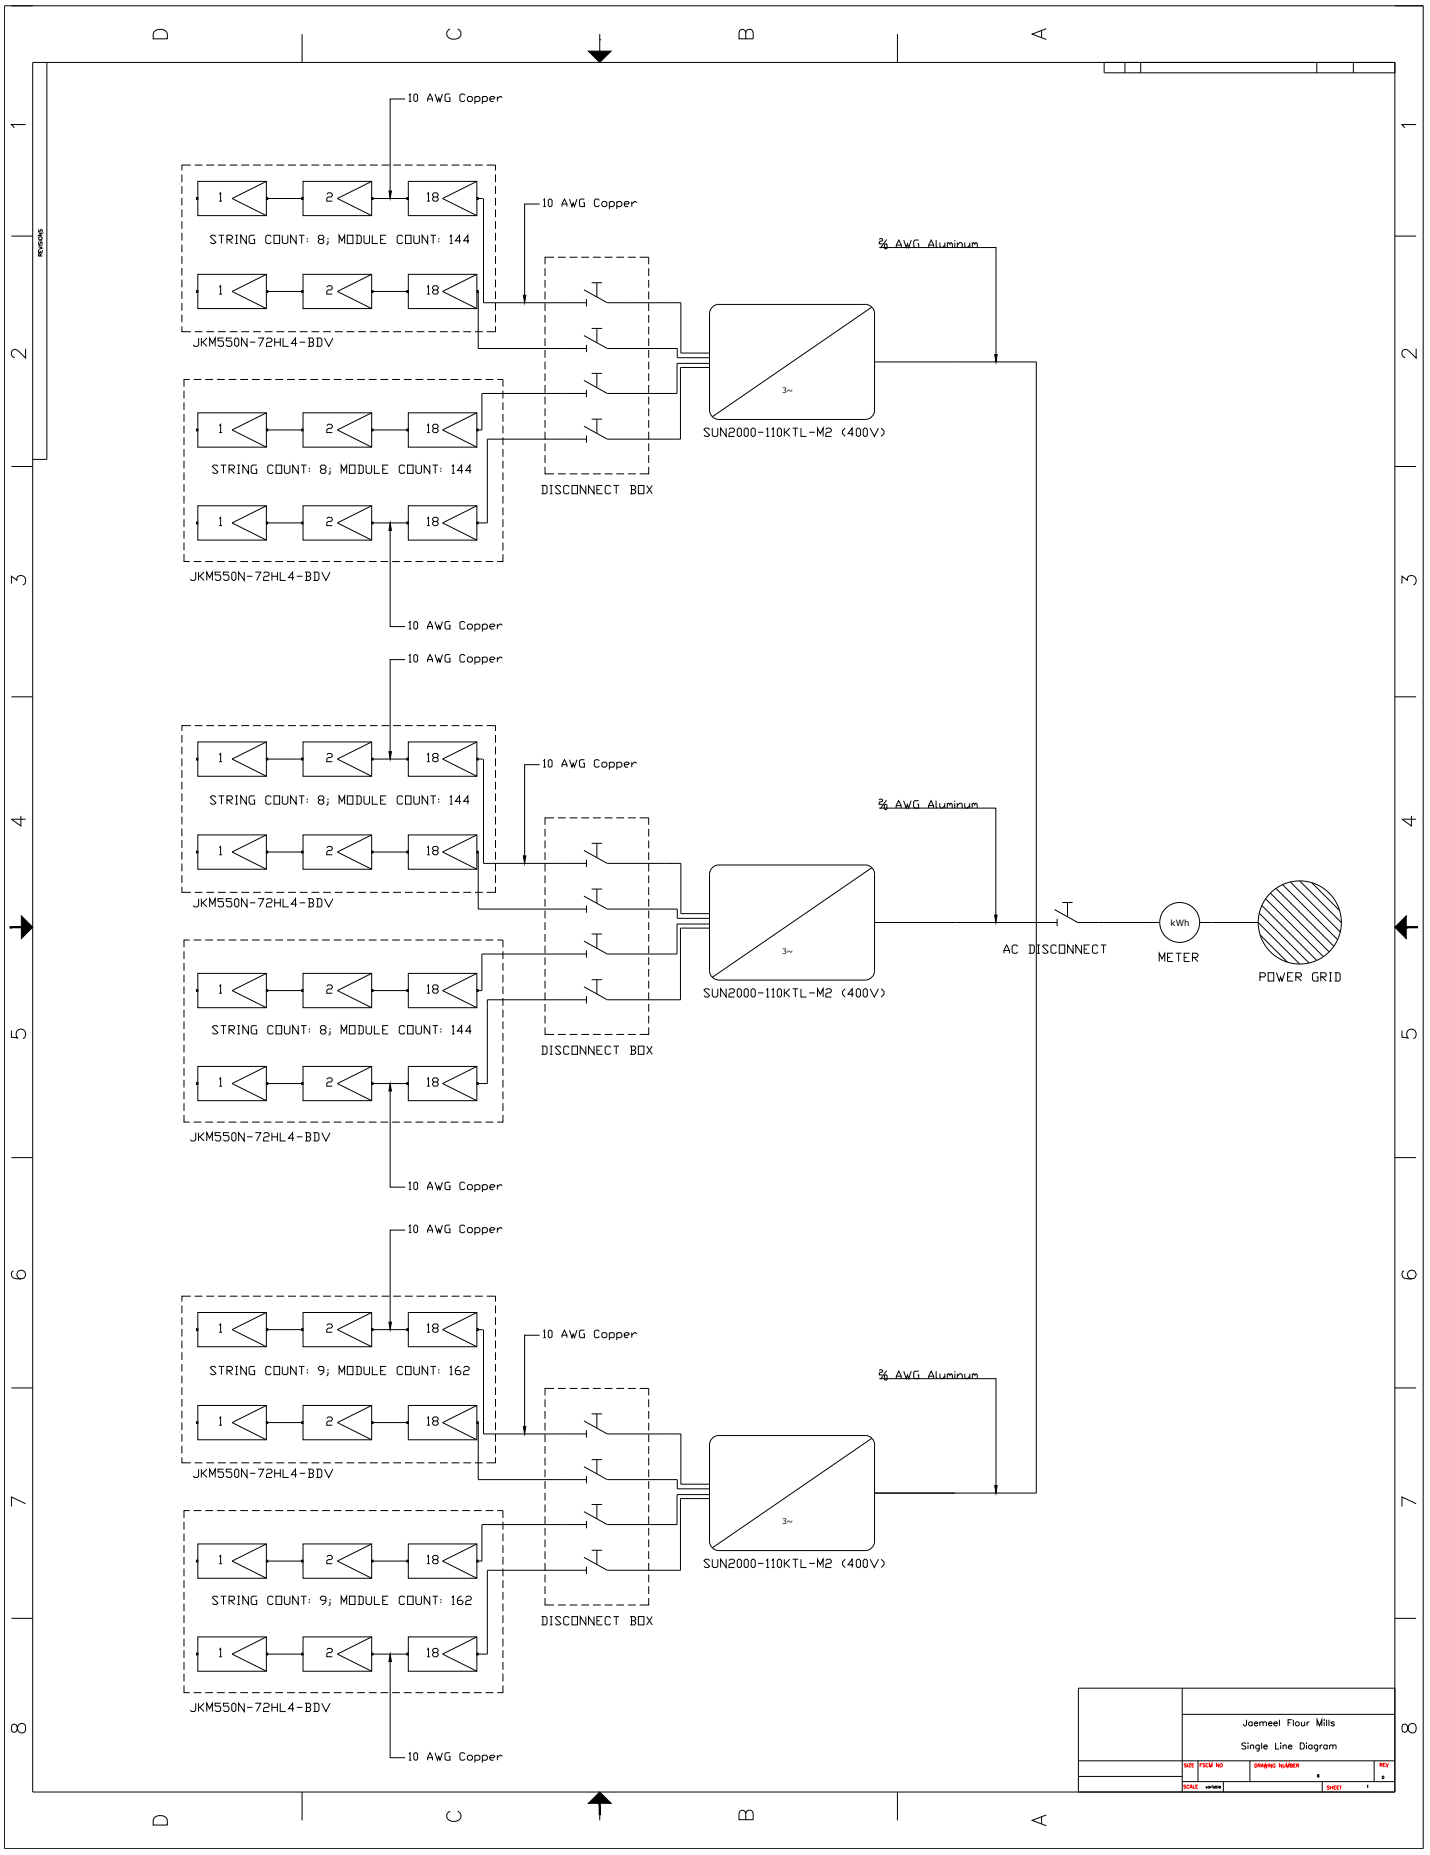


DC WIRING DIAGRAM

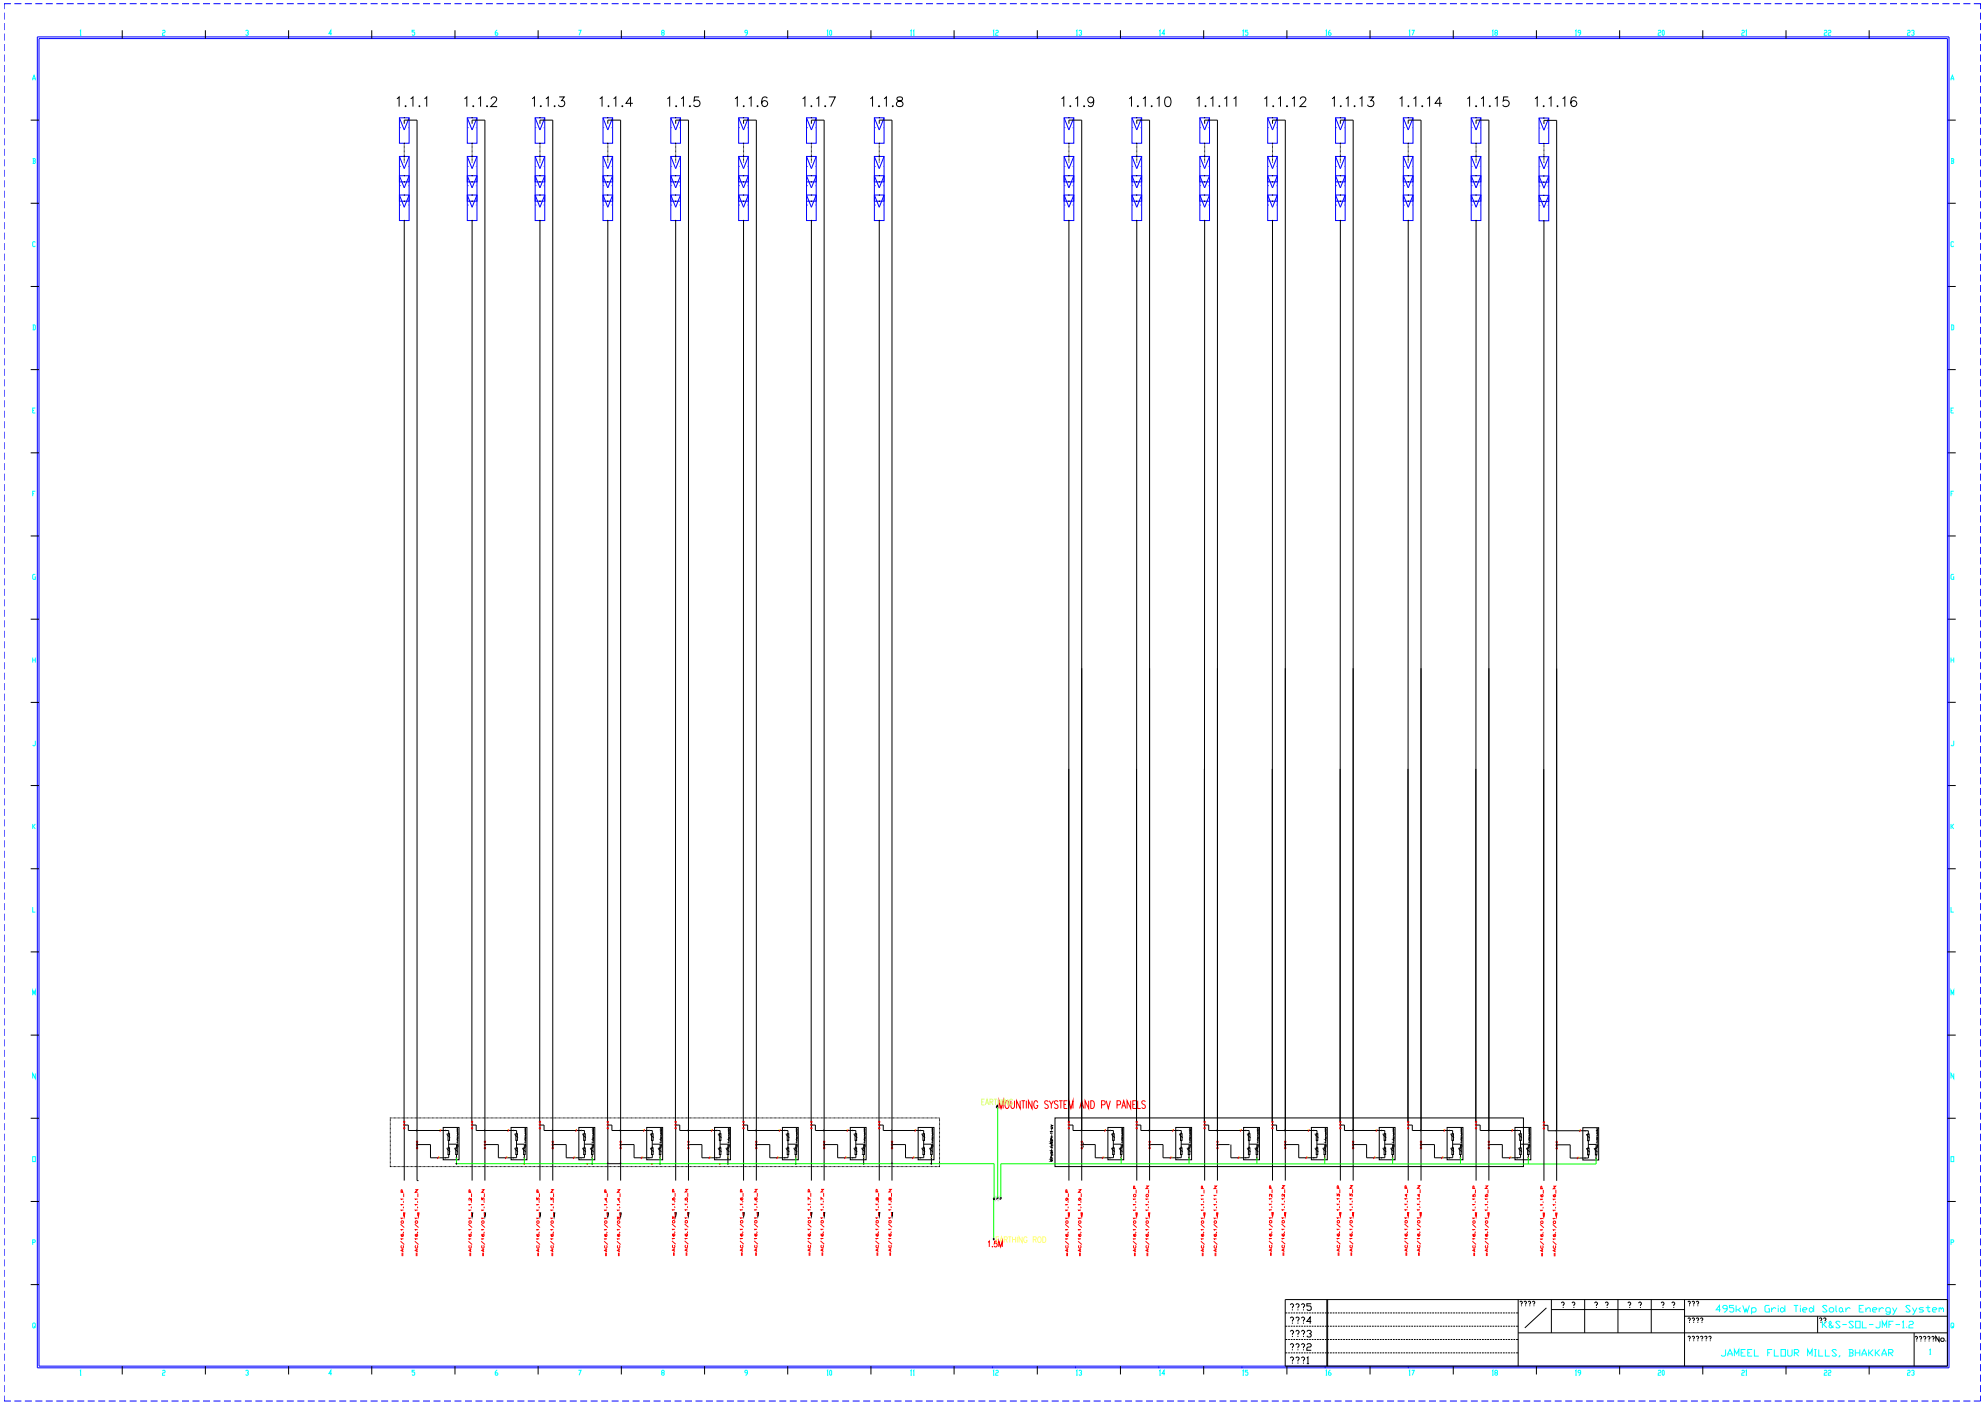


DC WIRING DIAGRAM

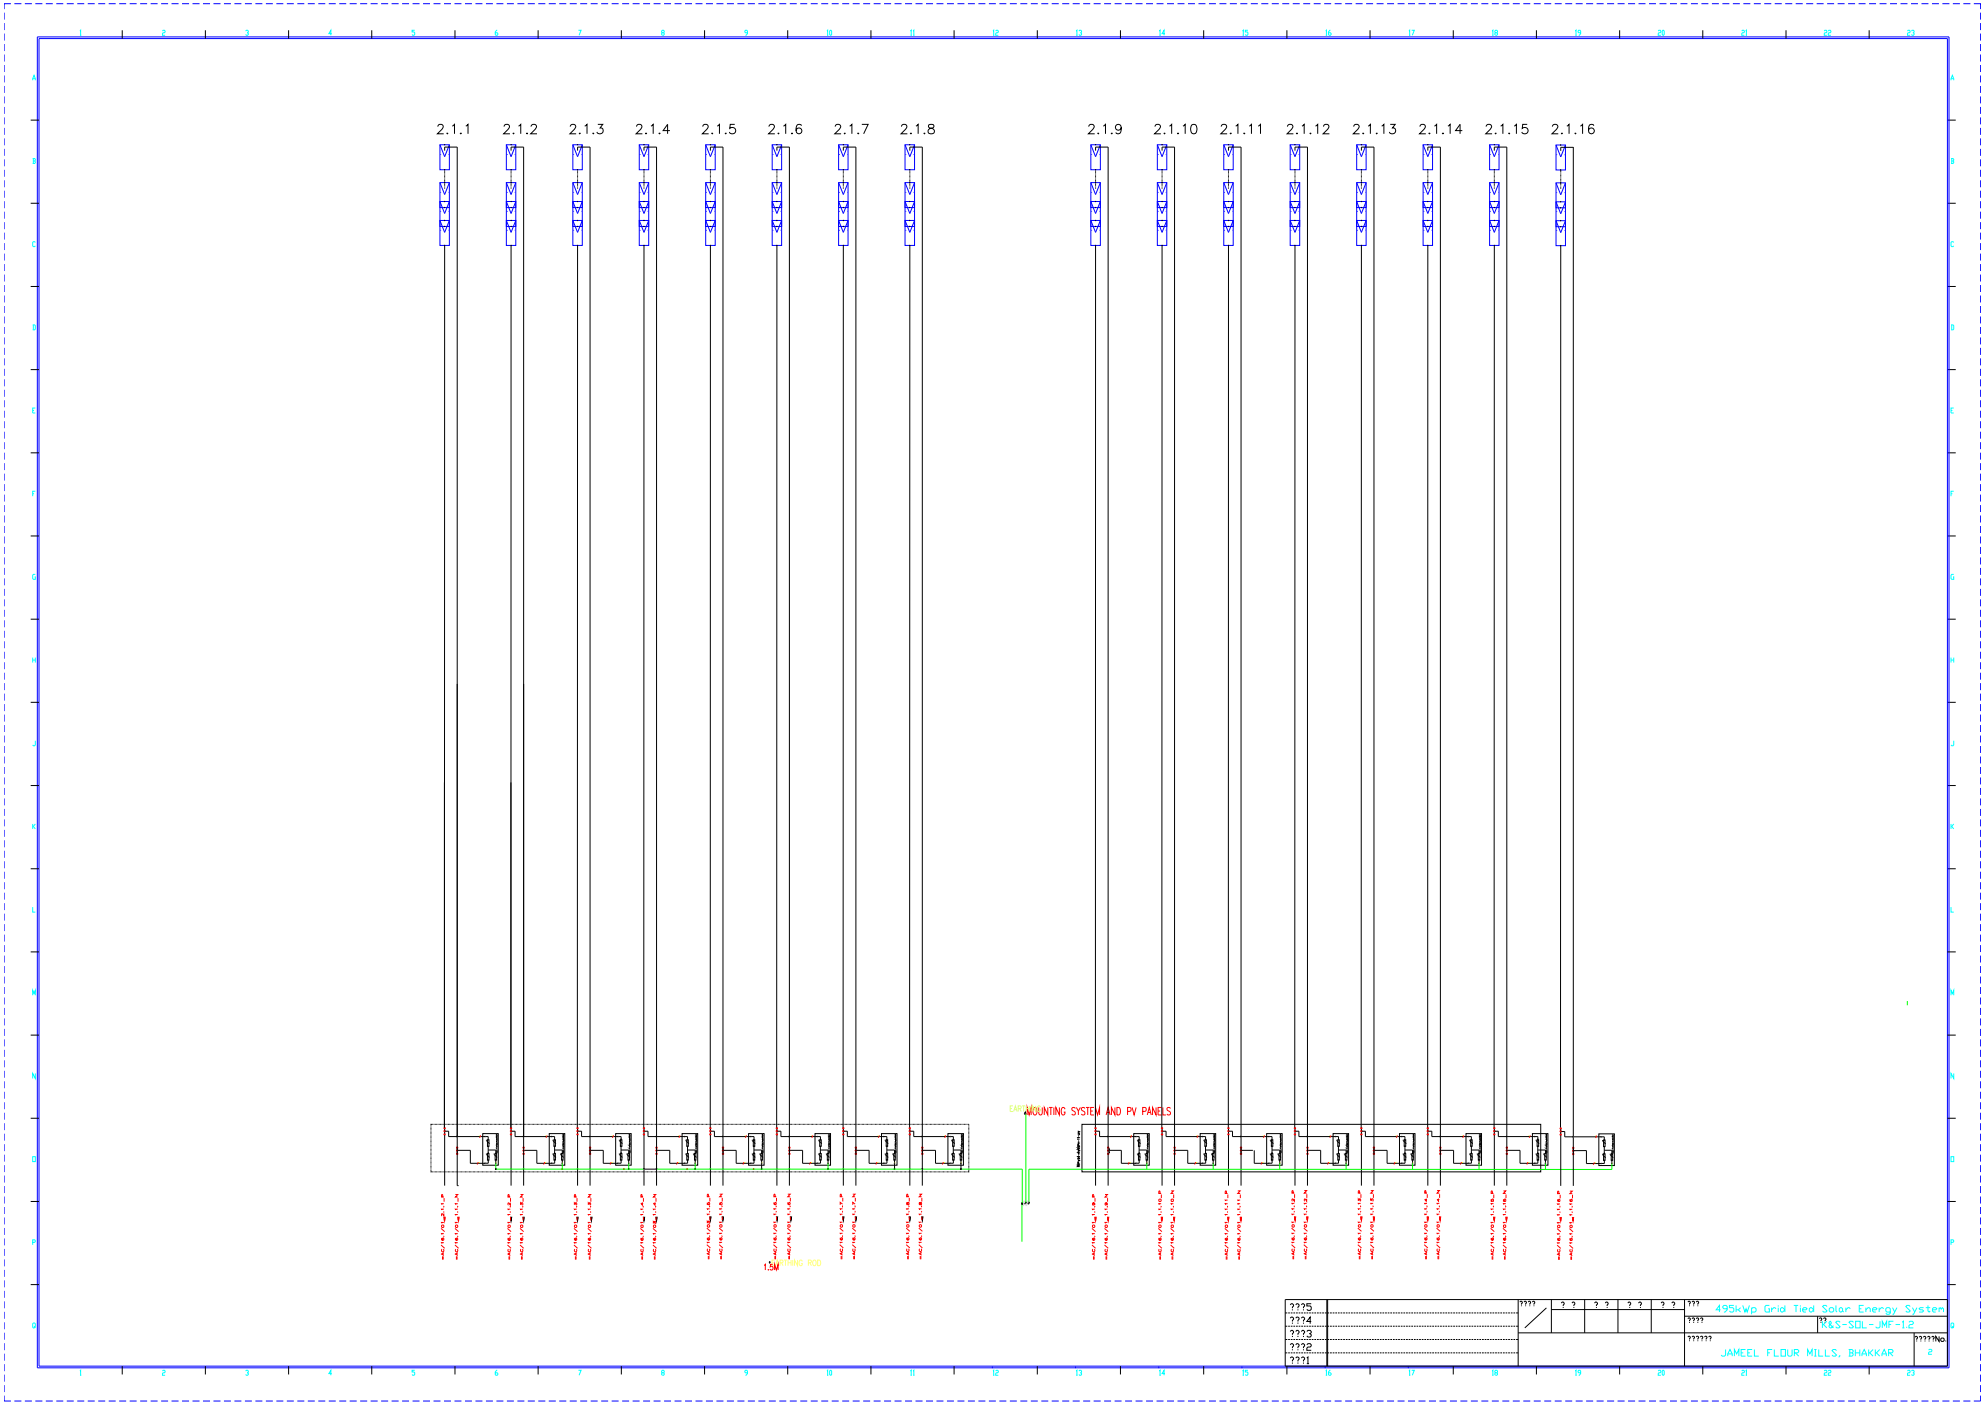

DC WIRING DIAGRAM

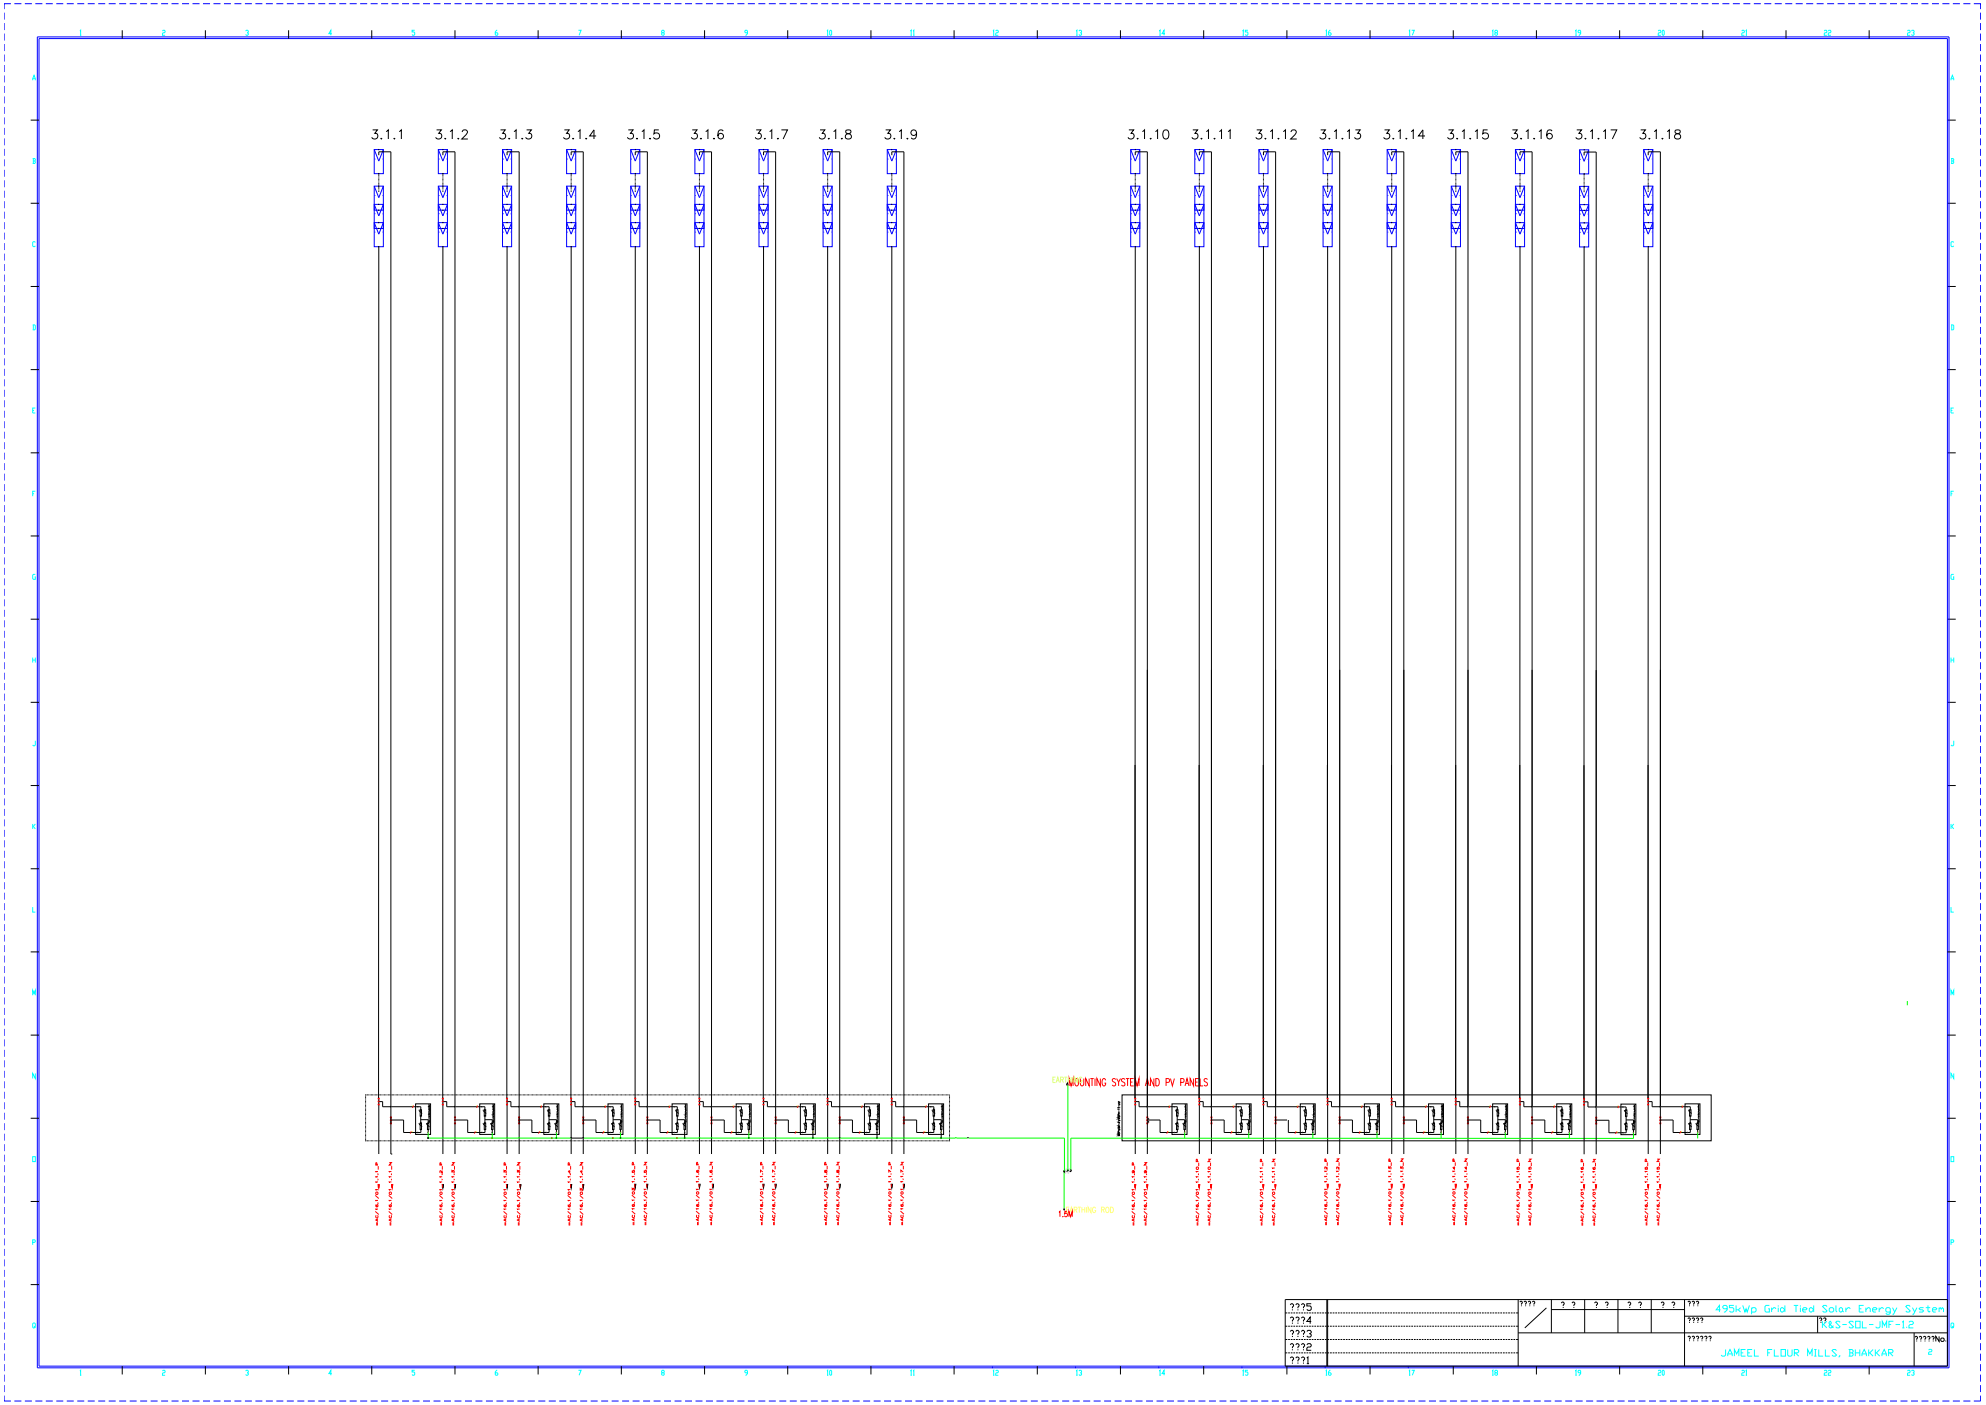

AC WIRING DIAGRAM

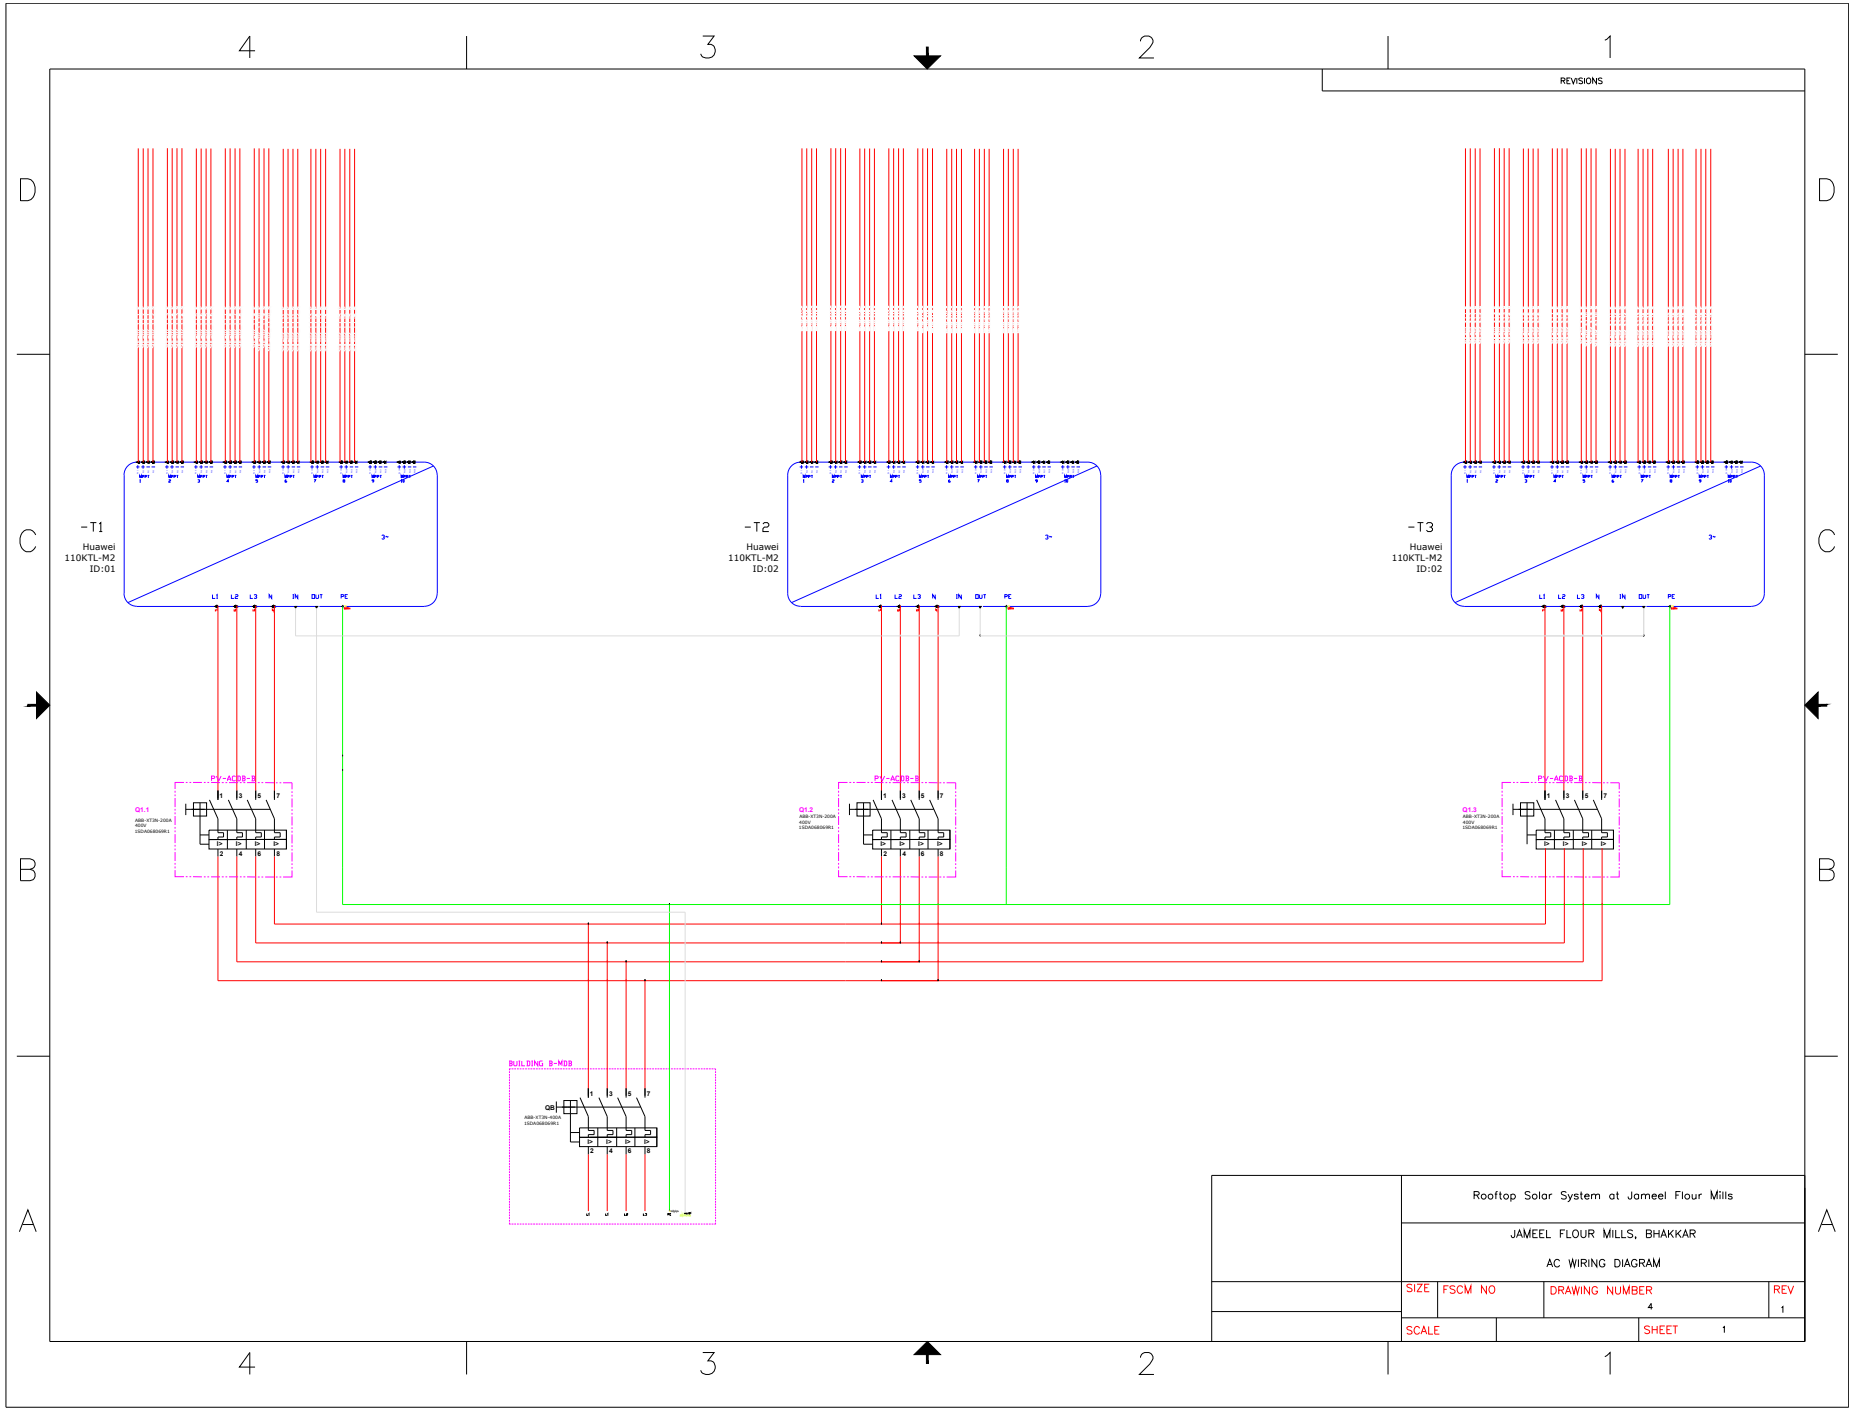

AC DISTRIBUTION AND GRID CONNECTION:

