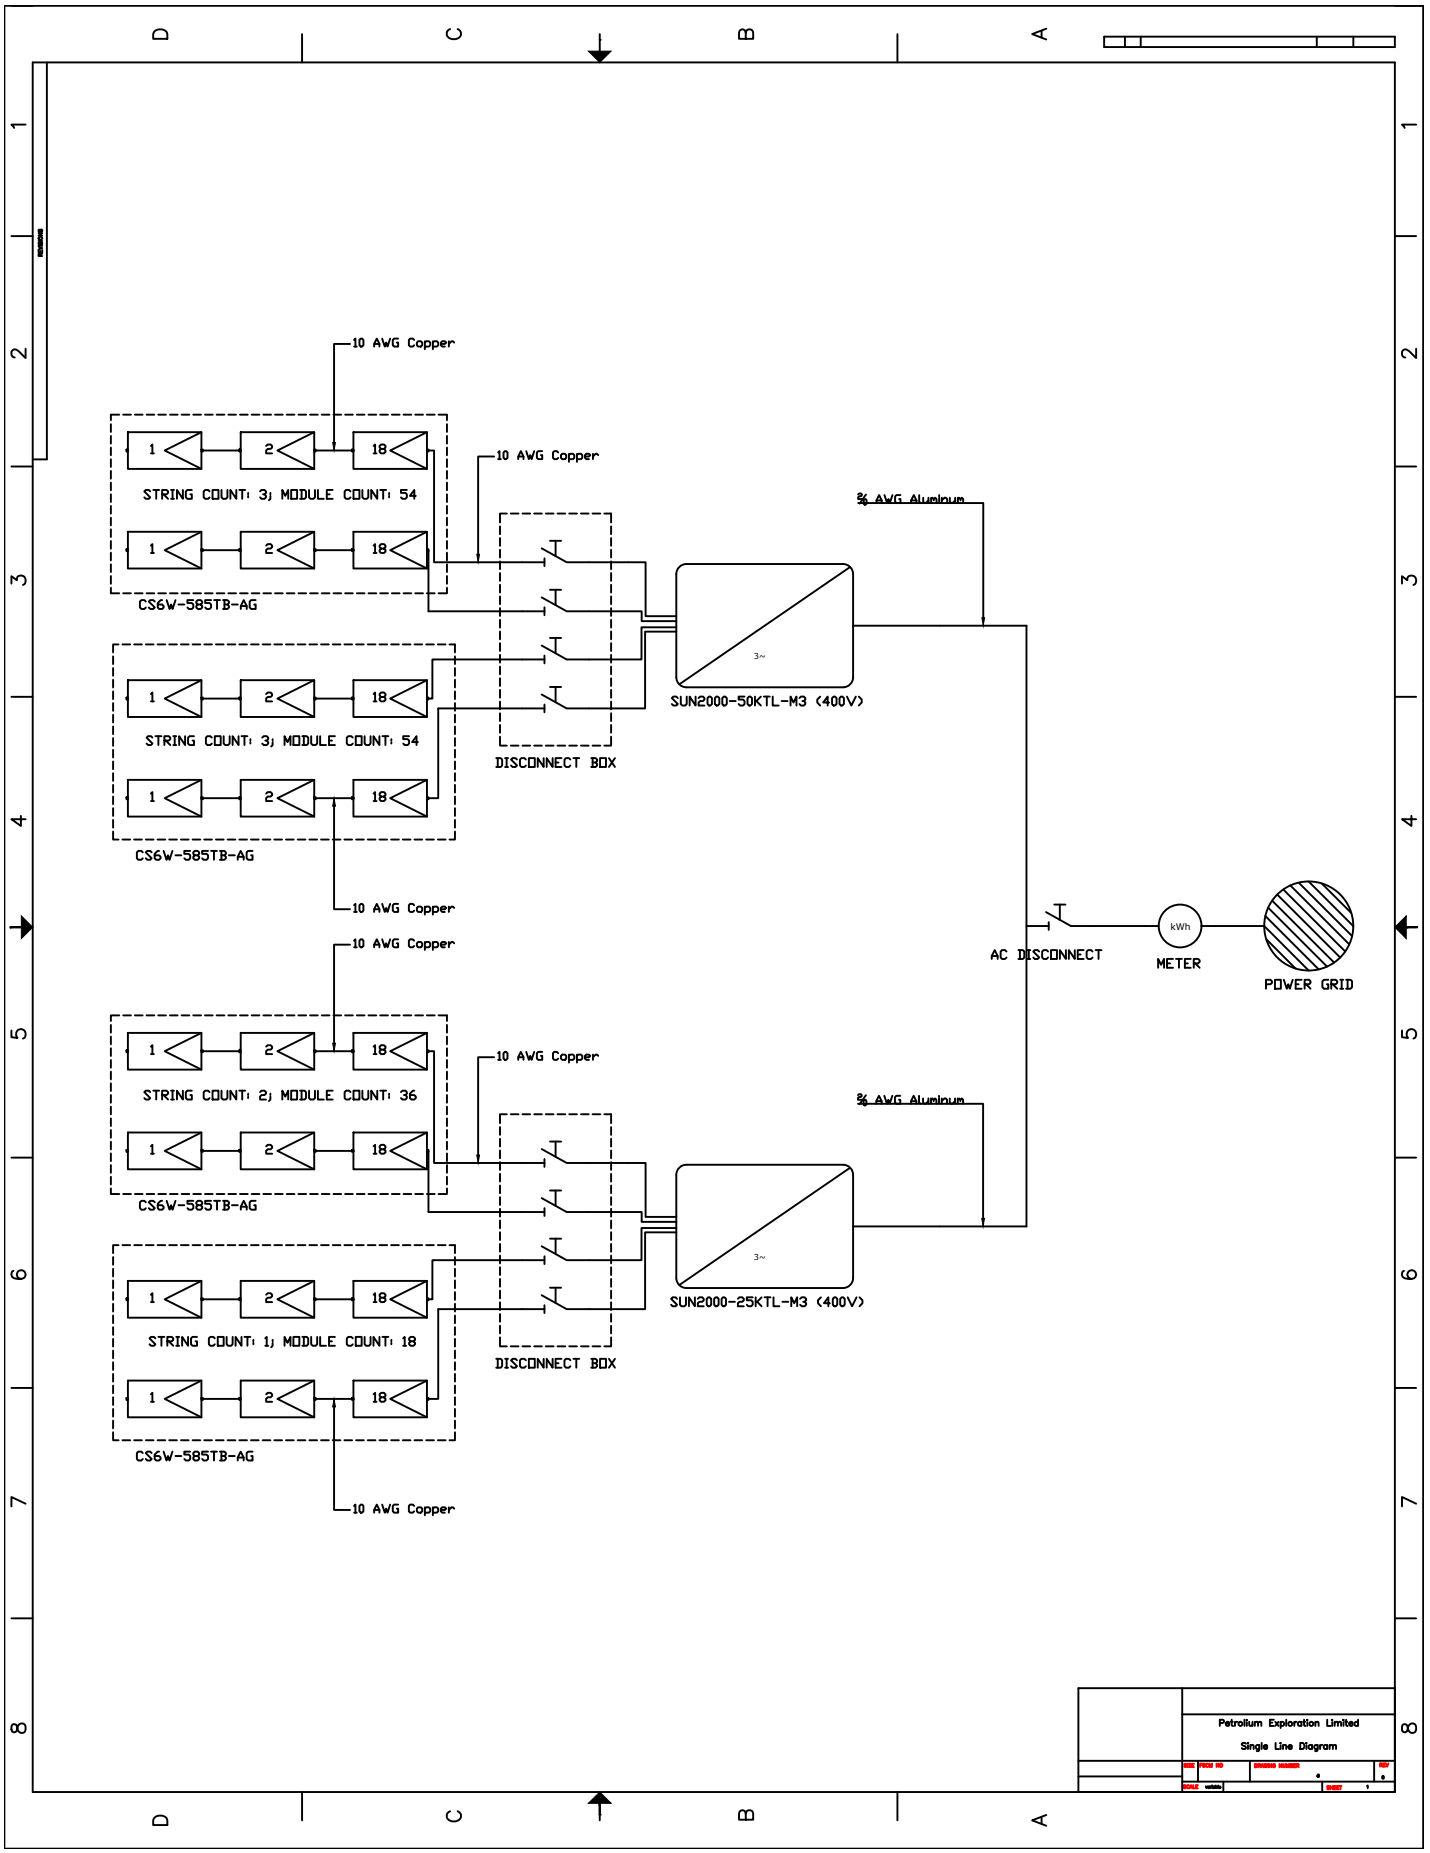

10 AWG Copper
1
2
18
STRING COUNT: 3; MODULE COUNT: 54
CS6W-585TB-AG
10 AWG Copper
8 AWG Aluminum
DISCONNECT BOX
SUN2000-50KTL-M3 (400V)
AC DISCONNECT
kWh
METER
POWER GRID
STRING COUNT: 2; MODULE COUNT: 36
STRING COUNT: 1; MODULE COUNT: 18
SUN2000-25KTL-M3 (400V)
Petroleum Exploration Limited
Single Line Diagram